



	Calitatea	Nume	Semnatura	Scara 1:50	Plan armare placă	Plansa nr. R.1
	SEF PROIECT	conf. dr. ing. Bogdan Hegheș				
	PROIECTAT	Dulli Dávid Patrik		Data feb. 2025.		
	DESENAT	Dulli Dávid Patrik				


UNIVERSITATEA TEHNICA CLUJ-NAPOCA FACULTATEA DE CONSTRUCTII			Beton armat și precomprimat II Anul III, IUDR Grupa 3631 An univeristar 2024-2025		Proiect nr. 2/ 2025
--	--	--	--	--	-------------------------------

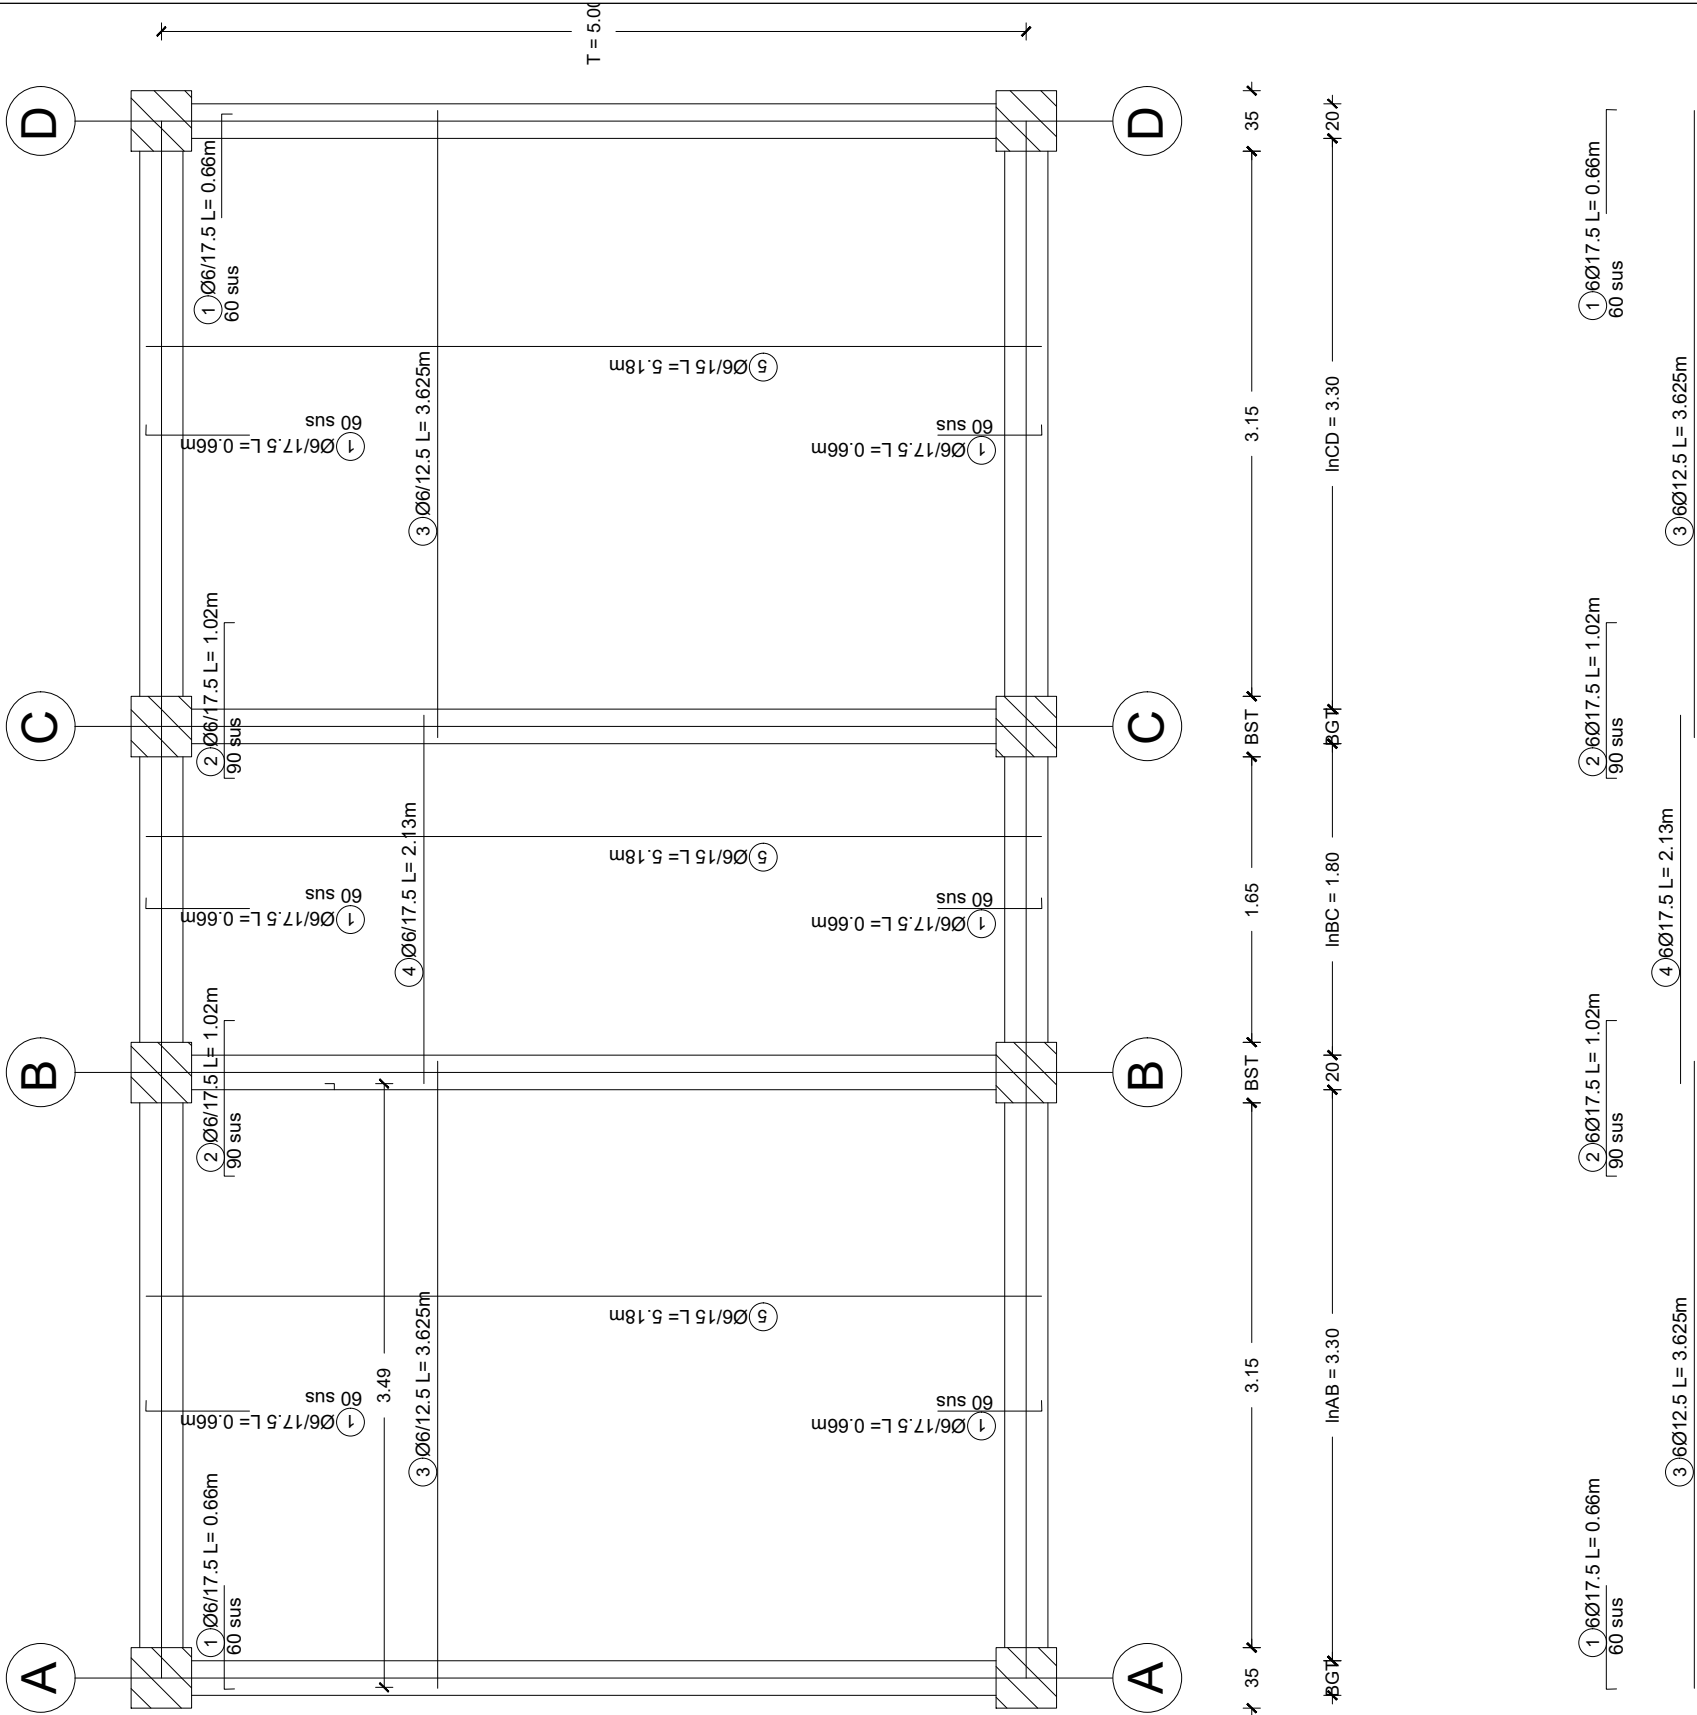

Plan armare și cofraj GL

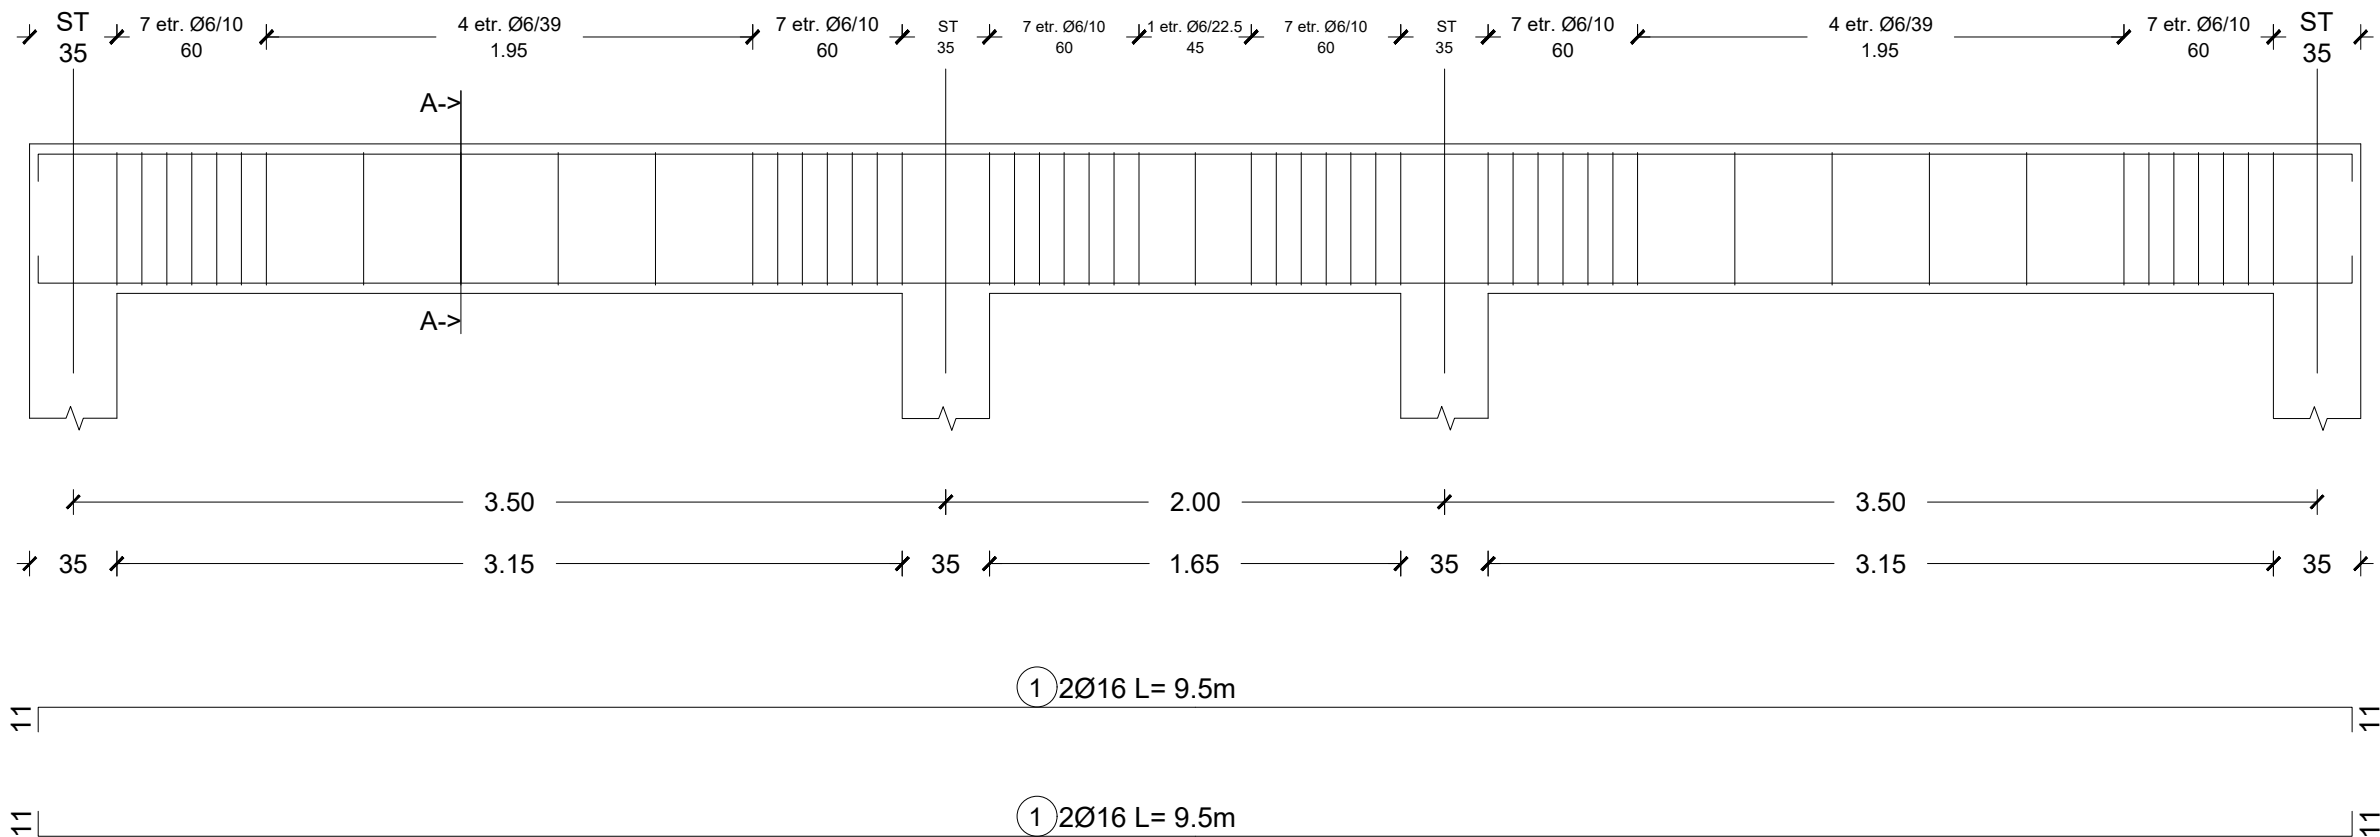

Secțiunea
A-A

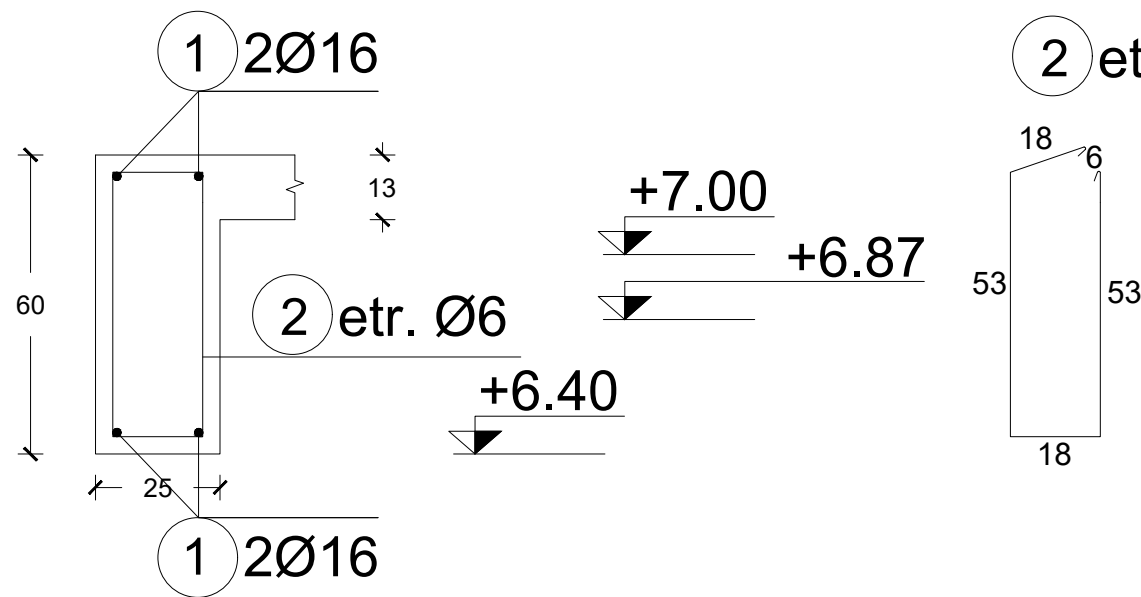


Clasă beton:
C25/30 XC2
A/C = max 0.6, agr. max. 16mm
Oțel:
B500
Acoperire cu beton cnom = 35mm
Clasă ductilitate M

25 1 2Ø16	UNIVERSITATEA TEHNICA CLUJ-NAPOCA FACULTATEA DE CONSTRUCTII			Beton armat și precomprimat II Anul III, IUDR Grupa 3631 An univeristar 2024-2025		Proiect nr. 2/ 2025
	Calitatea	Nume	Semnatura	Scara 1:50	Plan armare și plan cofraj GL	Plansa nr. R.3
	SEF PROIECT	conf. dr. ing. Bogdan Hegheș				
	PROIECTAT	Dulli Dávid Patrik		Data feb. 2025.		
	DESENAT	Dulli Dávid Patrik				

Plansa nr. R.4

Plan cofraj placă 1:50

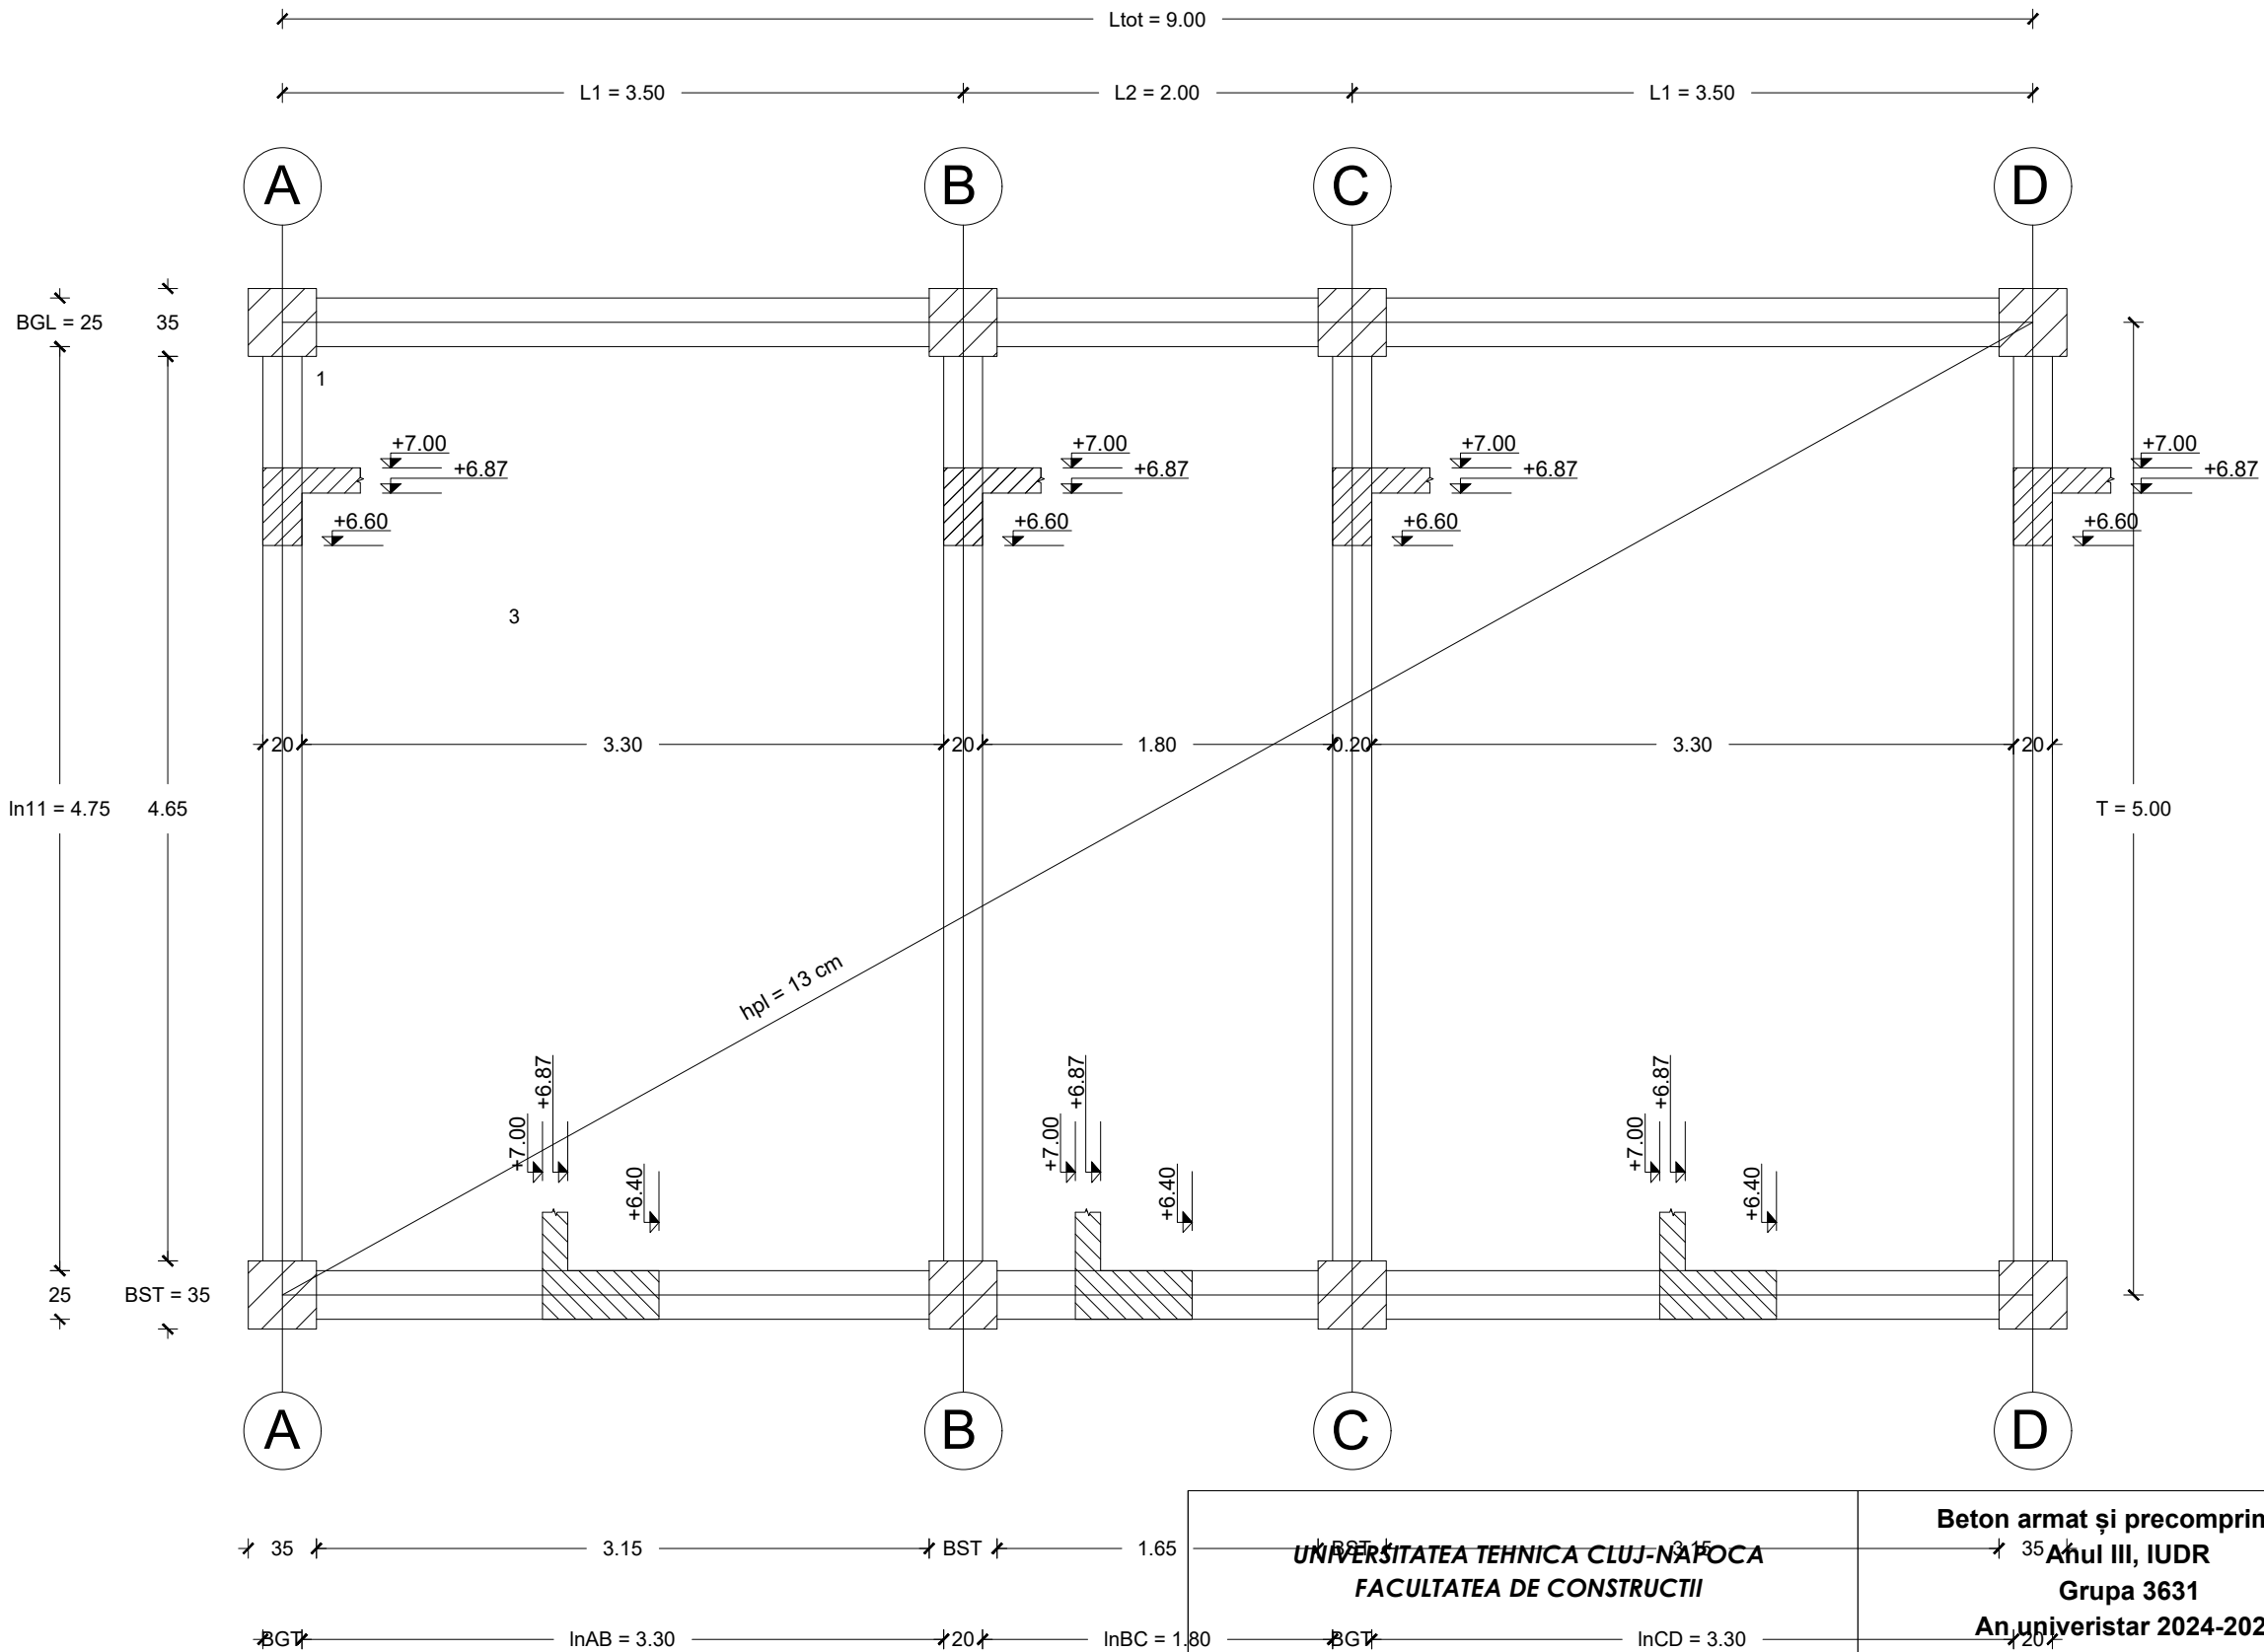

UNIVERSITATEA TEHNICA CLUJ-NAPOCA FACULTATEA DE CONSTRUCTII			Beton armat și precomprimat II Anul III, IUDR Grupa 3631 Anul universitar 2024-2025		Proiect nr. 2/2025
Calitatea			Scara 1:50	Plan cofraj placă	Plansa nr. R.2
SEF PROIECT					
PROIECTAT			Data feb. 2025.		
DESENAT					