



SECȚIUNE TRANSVERSALĂ
SCARA 1:20

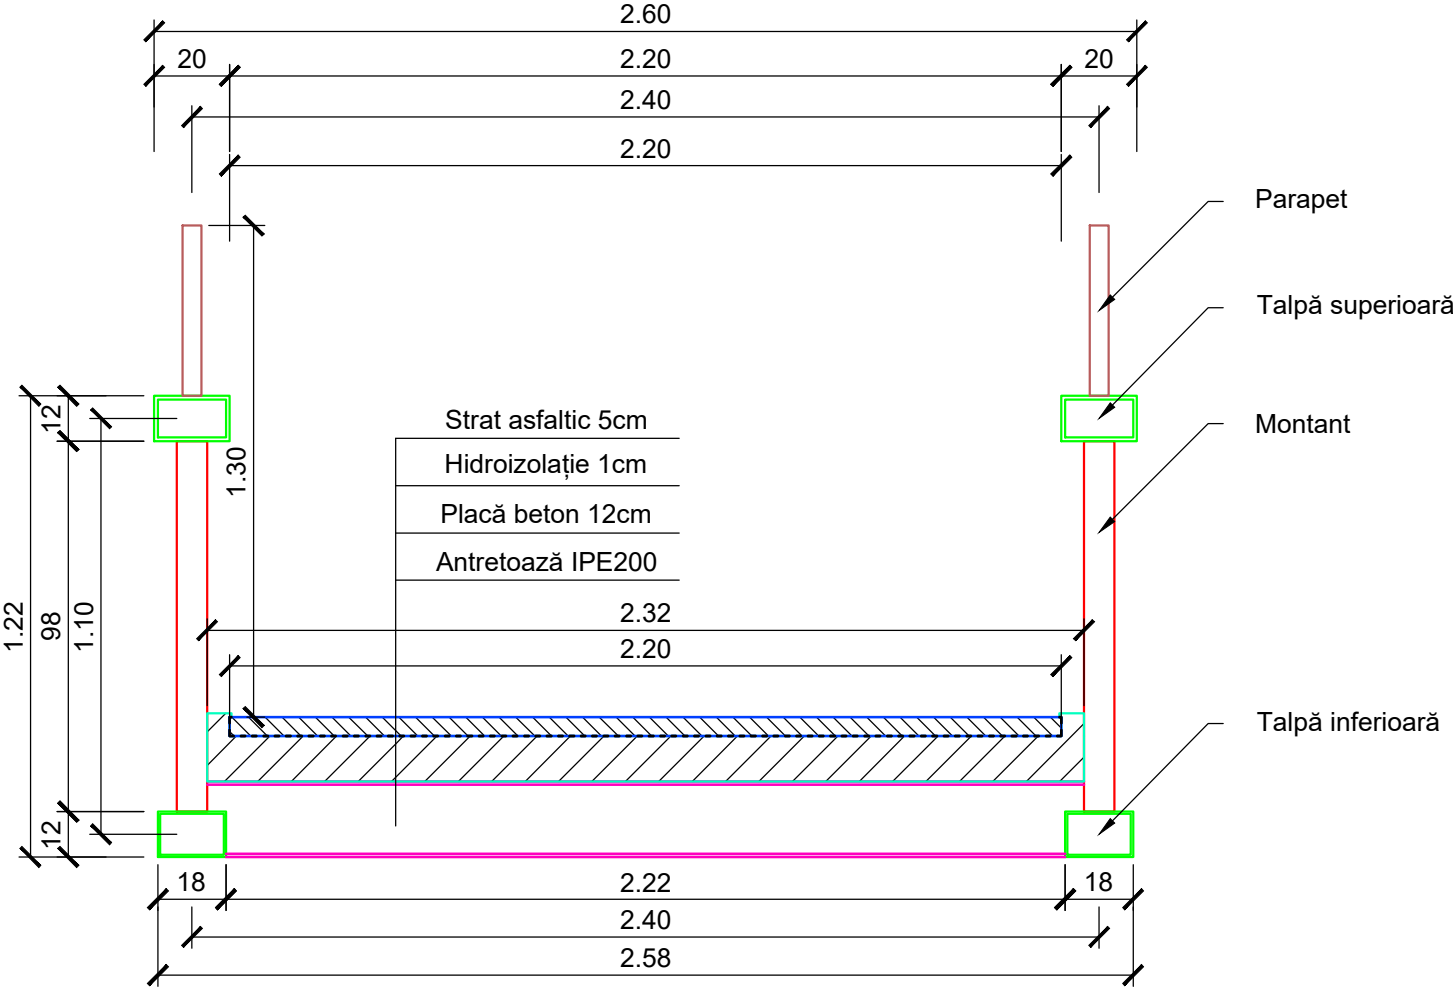


DETALII ELEMENTE
SCARA 1:5


TALPĂ SUPERIOARĂ

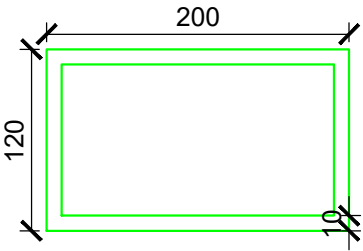


ANTRETOAZĂ IPE 200

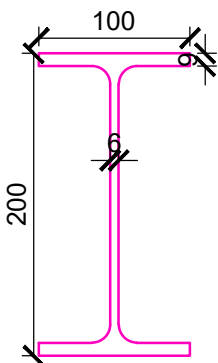


TALPĂ INFERIOARĂ

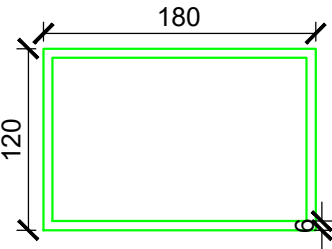


PARAPET

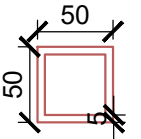

DIAGONALĂ

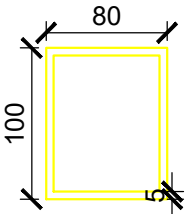


MONTANT

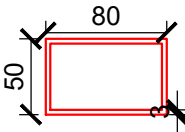


UNIVERSITATEA TENICĂ CLUJ-NAPOCA FACULTATEA DE CONSTRUCȚII			CONSTRUCȚII METALICE		NR. PL.
			ANUL IV	GRUPA 3641	1
	NUME	SEMN.	SCARA 1:5 1:20	DETALII ELEMENTE PROFIL TRANSVERSAL	
DESENAT	DULLI DAVID PATRIK				
VERIFICAT	Conf. Dr. Ing. Danciu Alexandra Denisa		DATA MAI 2026		

VEDERE LATERALĂ/
SECȚIUNE LONGITUDINALĂ
SCARA 1:100

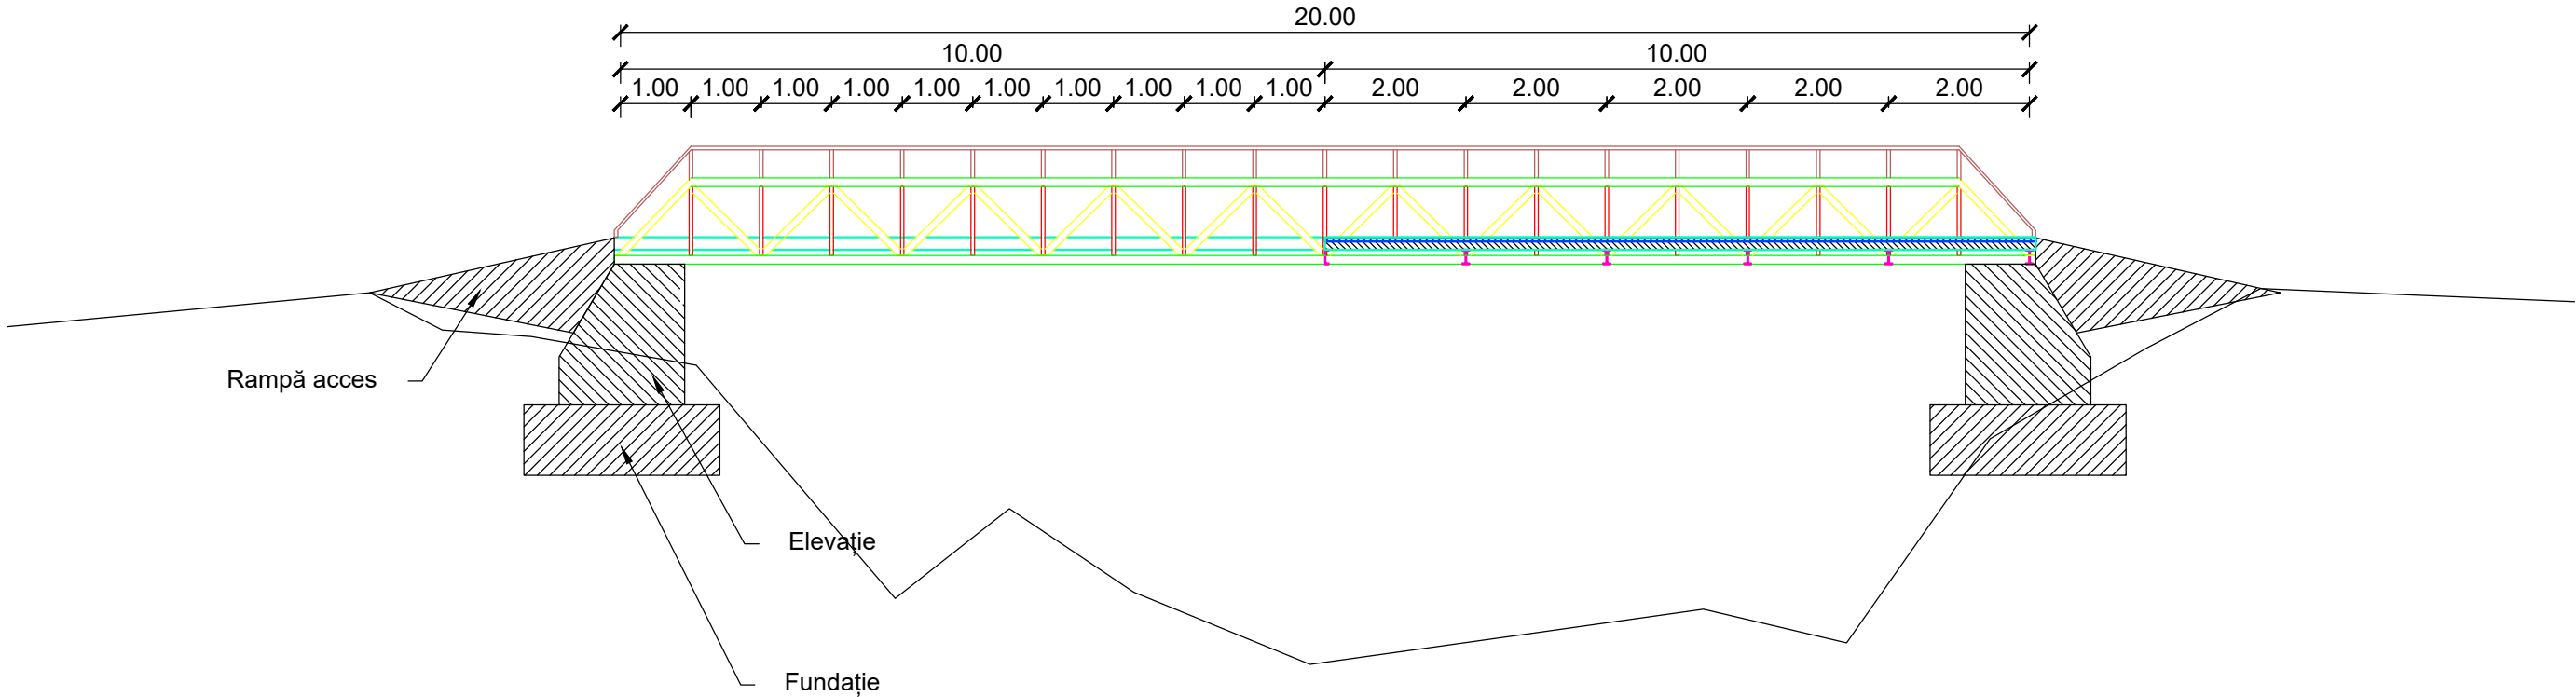

UNIVERSITATEA TENICĂ CLUJ-NAPOCA FACULTATEA DE CONSTRUCȚII			CONSTRUCȚII METALICE		NR. PL .
			ANUL IV	GRUPA 3641	2
	NUME	SEMN.	SCARA	VEDERE LATERALĂ SECȚIUNE LONGITUDINALĂ	
DESENAT	DULLI DAVID PATRIK		1:100		
VERIFICAT	Conf. Dr. Ing. Danciu Alexandra Denisa		DATA MAI 2026		

VEDERE PLANĂ/
SECȚIUNE ORIZONTALĂ
SCARA 1:100

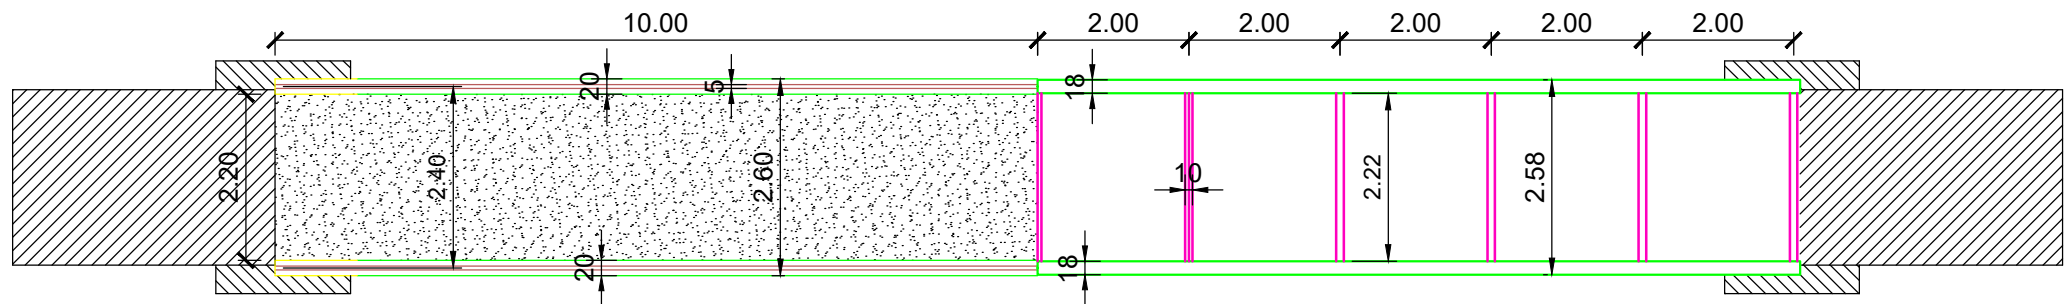

UNIVERSITATEA TENICĂ CLUJ-NAPOCA FACULTATEA DE CONSTRUCȚII			CONSTRUCȚII METALICE		NR. PL .
			ANUL IV	GRUPA 3641	3
	NUME	SEMN.	SCARA	VEDERE PLANĂ SECȚIUNE ORIZONTALĂ	
DESENAT	DULLI DAVID PATRIK		1:100		
VERIFICAT	Conf. Dr. Ing. Danciu Alexandra Denisa		DATA MAI 2026		