




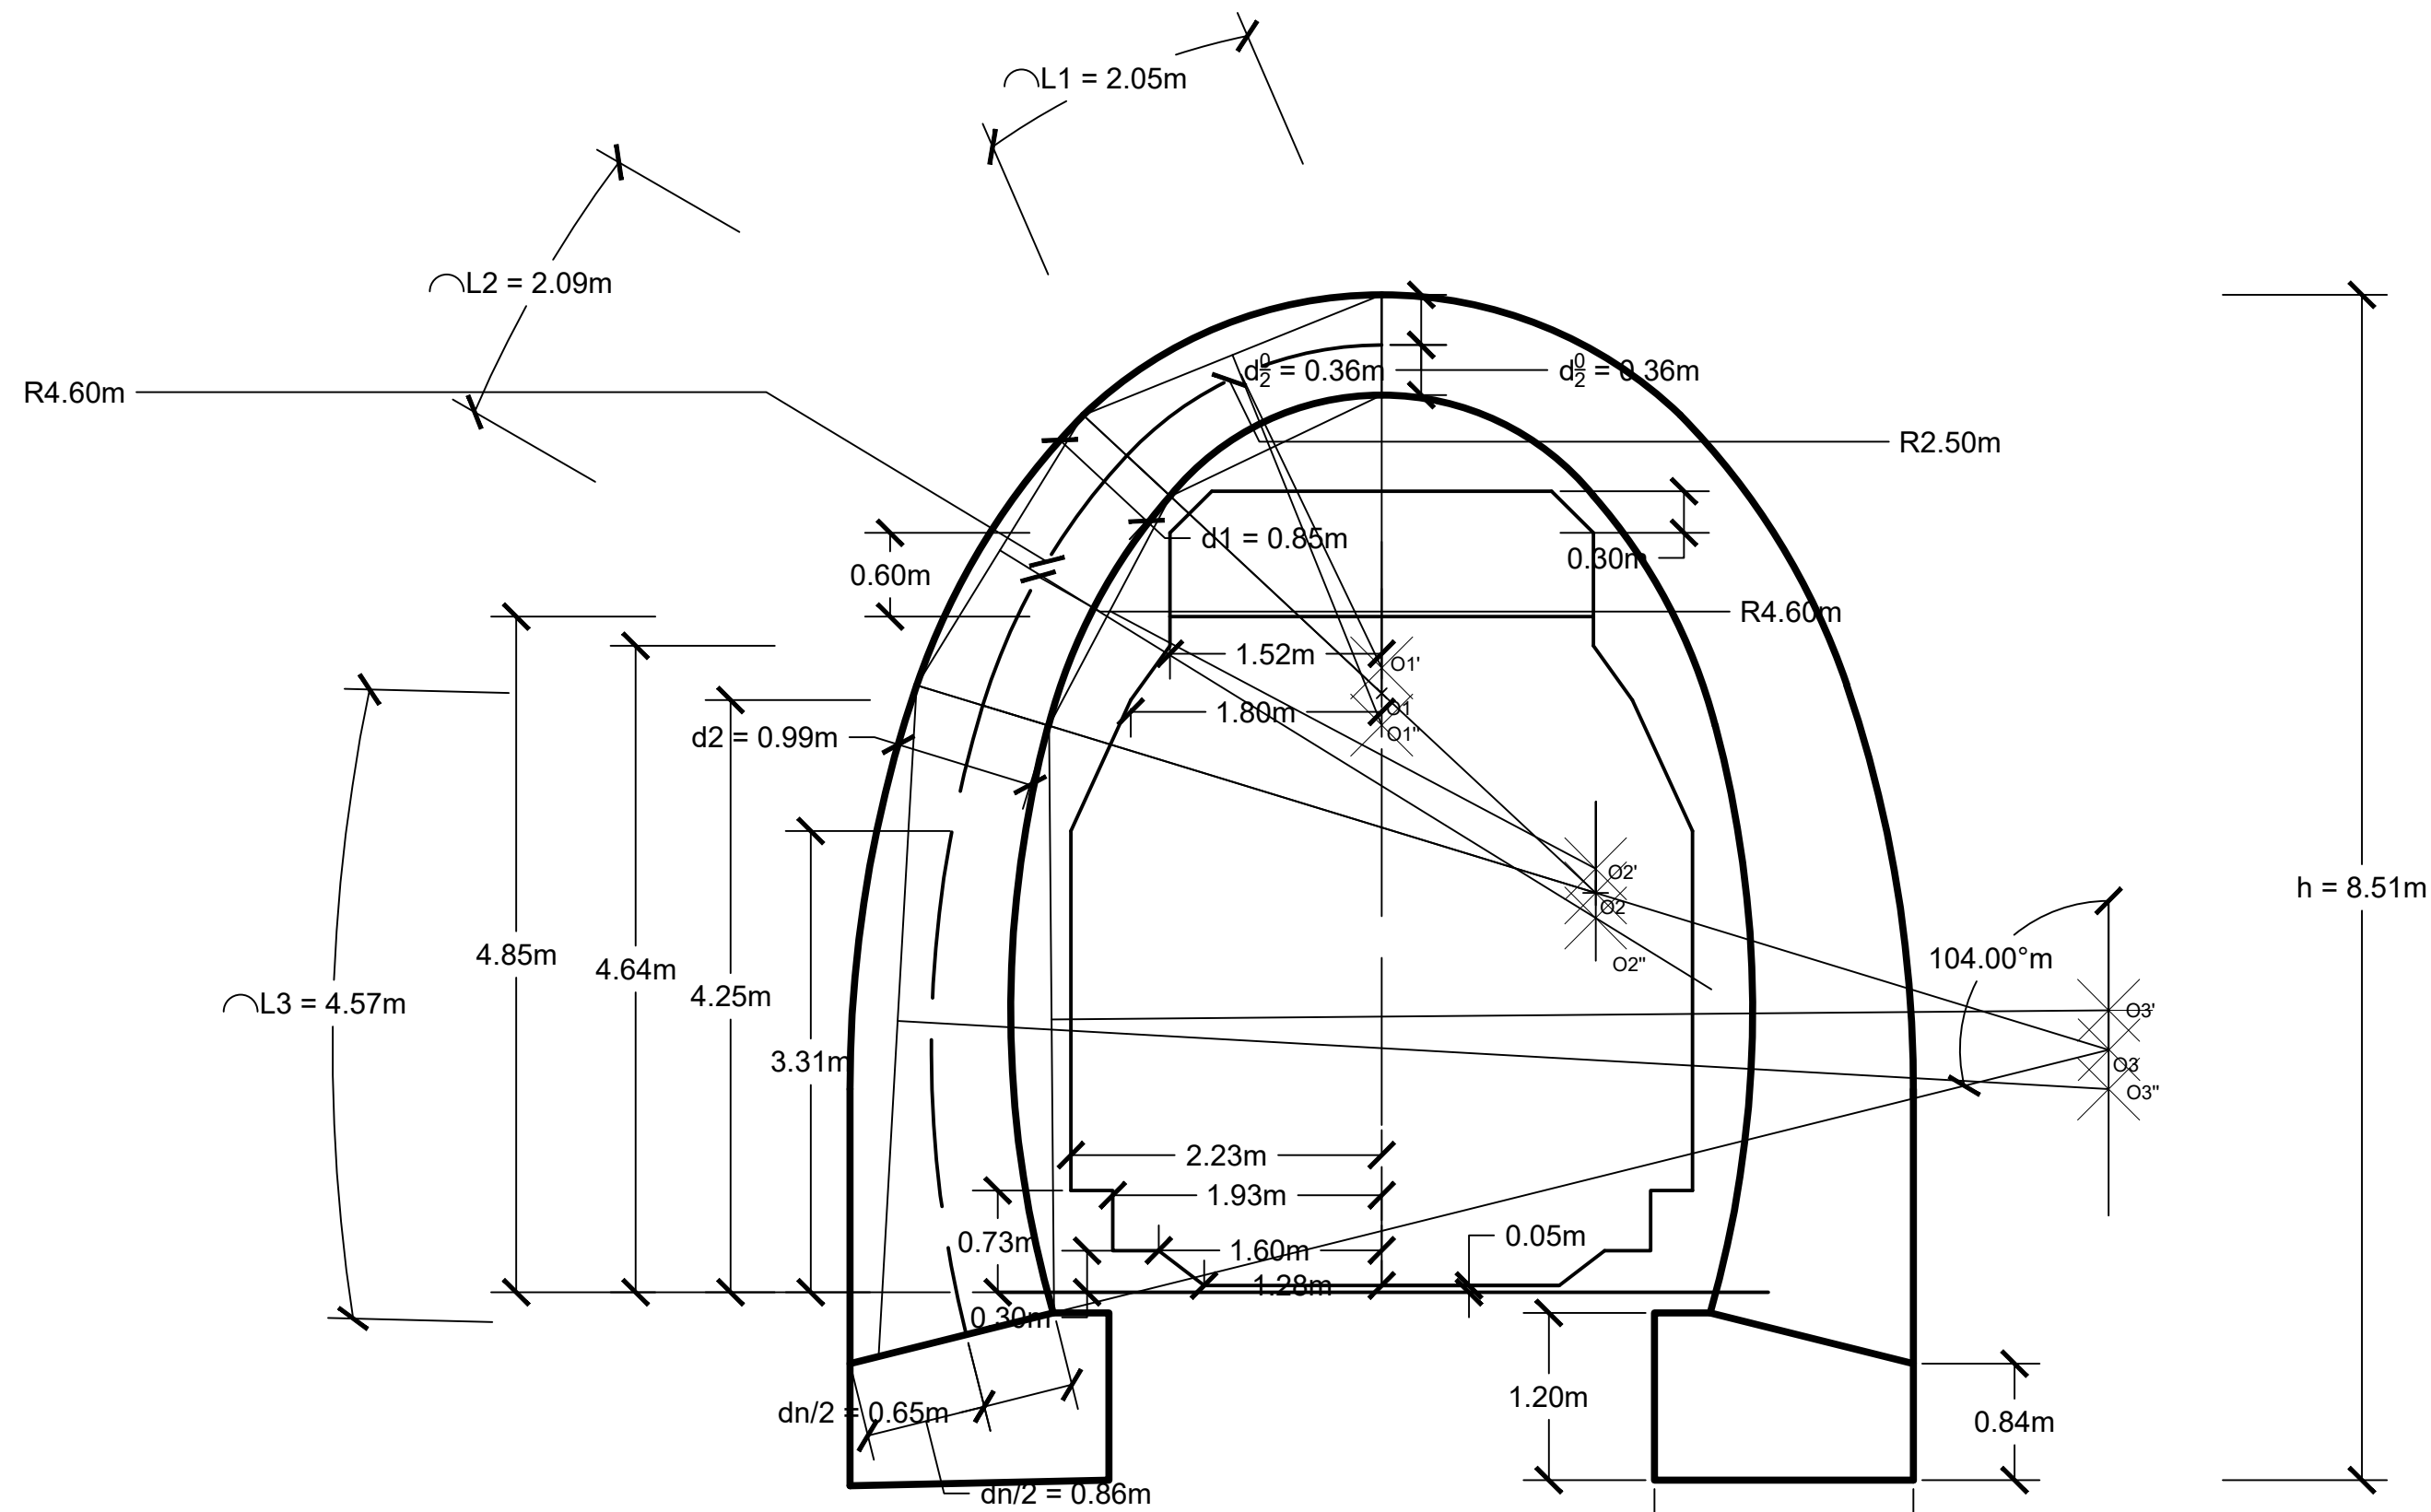


UNIVERSITATEA TEHNICA CLUJ-NAPOCA
FACULTATEA DE CONSTRUCTII

Construcții Subterane Urbane
Anul III, Secția IUDR
Grupa 3631
An univeristar 2024-2025

Proiect nr.
1/2025

Calitatea	Nume	Semnatura	Scara 1:50	Secțiune pentru gabarit dat	Plansa nr. 1
SEF PROIECT	Feneșan Crina-Ioana				
PROIECTAT	Dulli Dávid Patrik		Data mai. 2025		
DESENAT	Dulli Dávid Patrik				

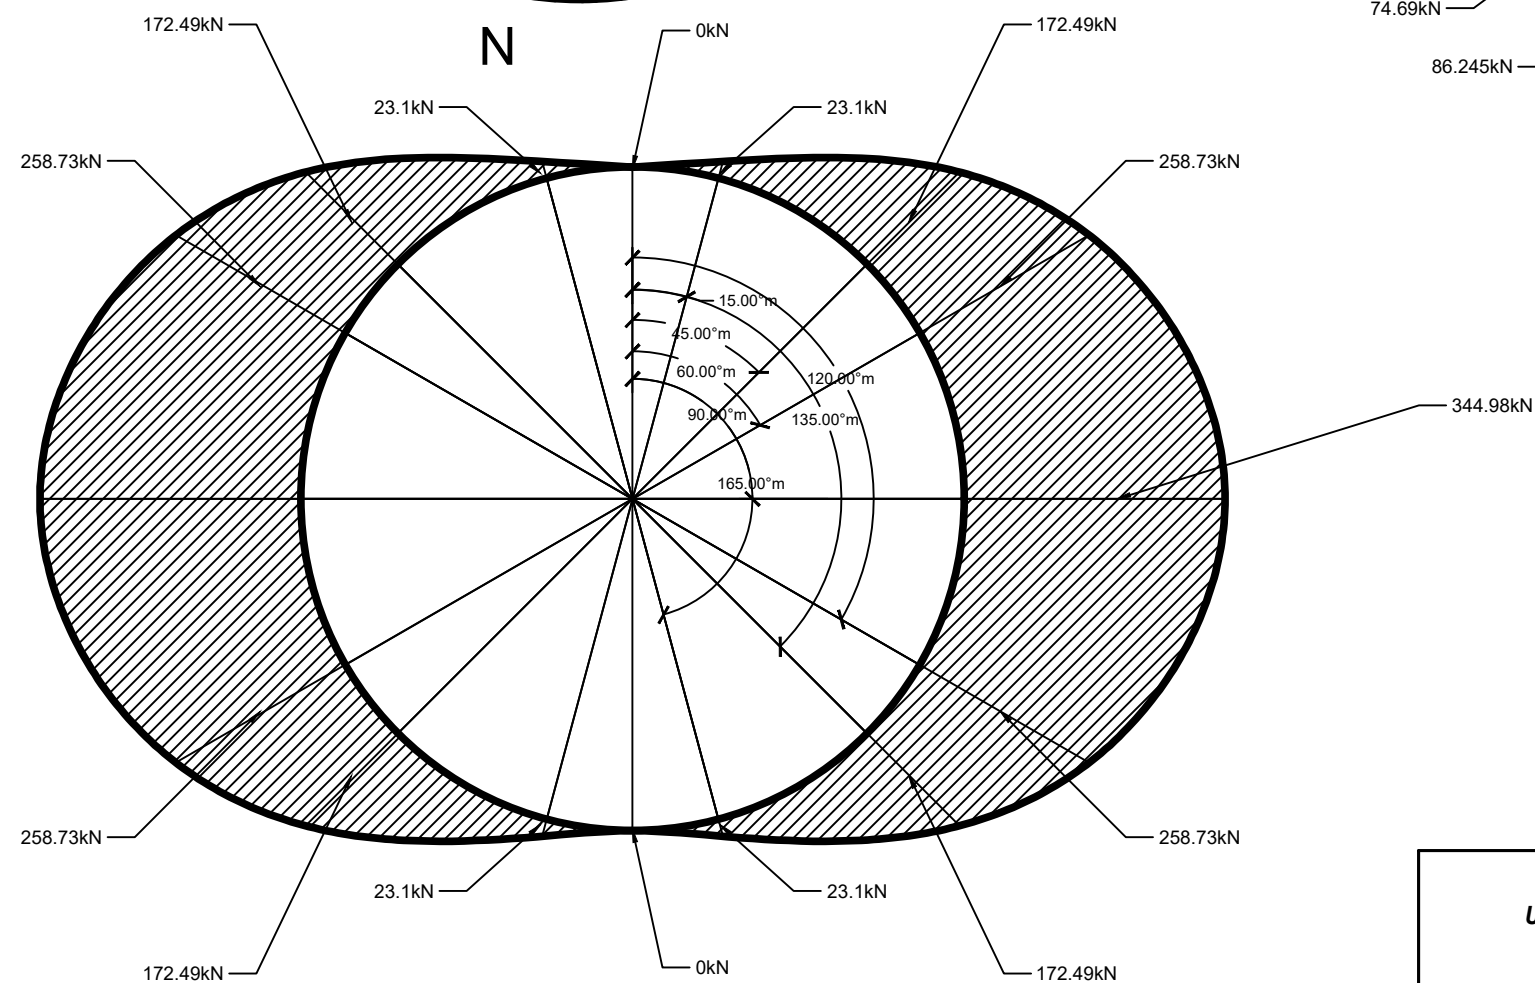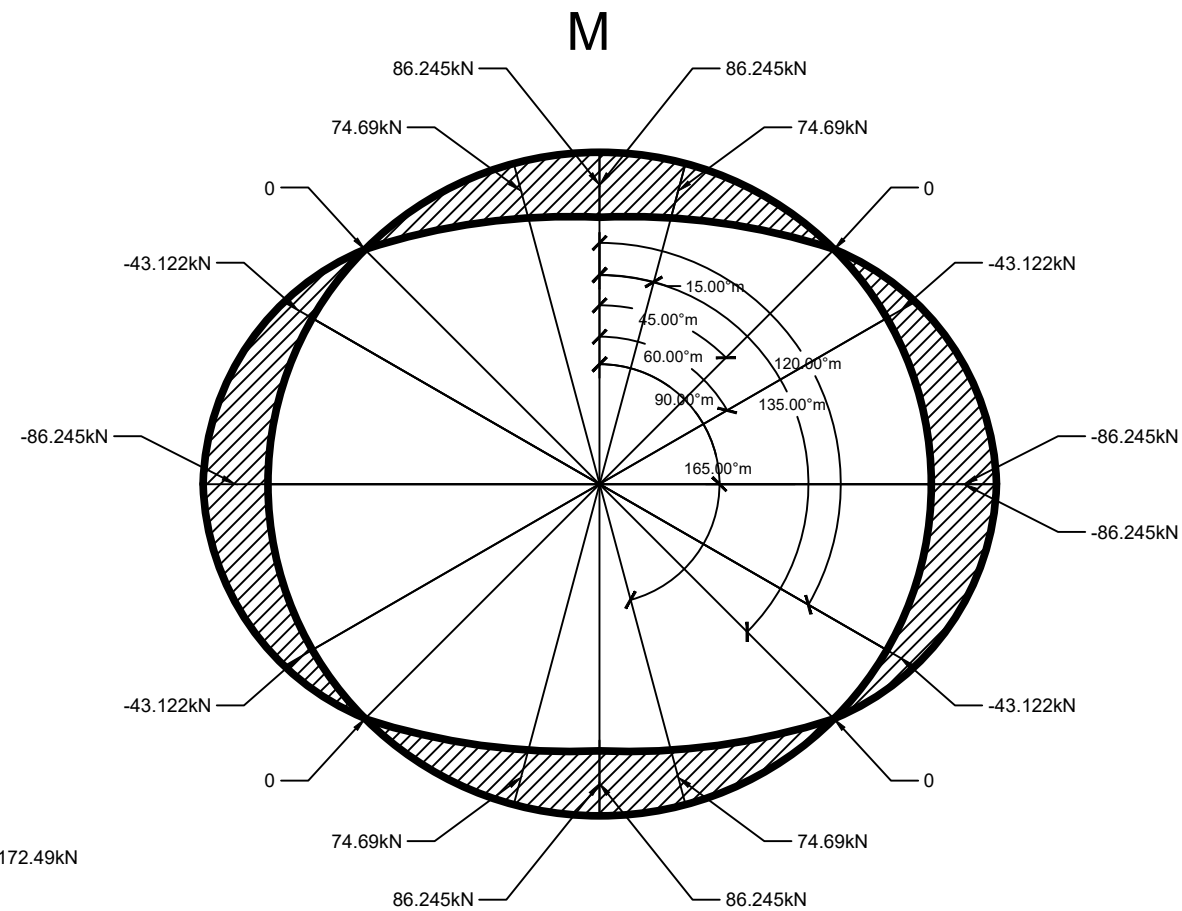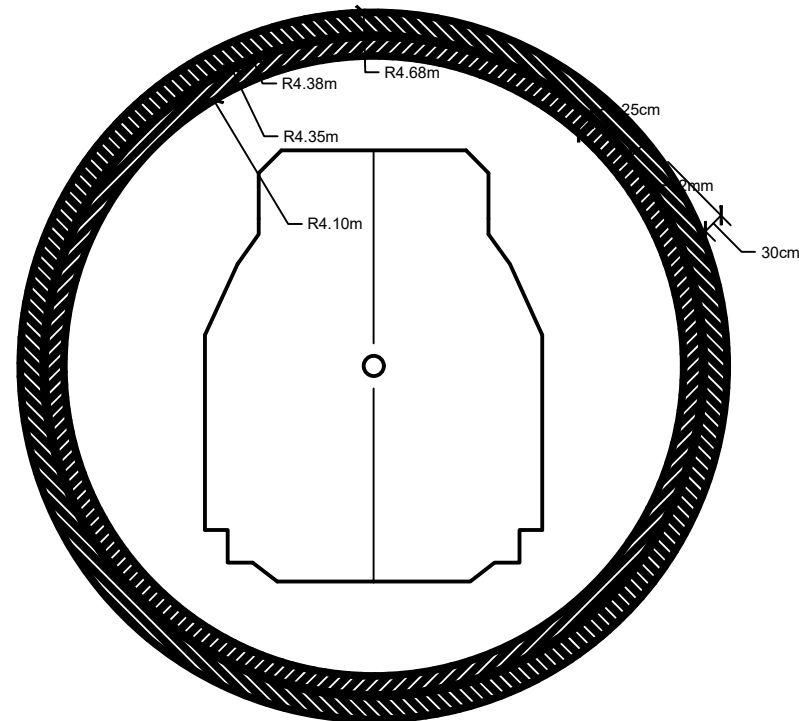

UNIVERSITATEA TEHNICA CLUJ-NAPOCA FACULTATEA DE CONSTRUCTII			Construcții Subterane Urbane Anul III, Sectia IUDR Grupa 3631 An univeristar 2024-2025		Proiect nr. 1/2025
Calitatea	Nume	Semnatura	Scara 1:100	Secțiune tunel circular	
SEF PROIECT	Feneșan Crina-Ioana				
PROIECTAT	Dulli Dávid Patrik		Data mai. 2025		Plansa nr. 2
DESENAT	Dulli Dávid Patrik				