



Vedere plană/ secțiune orizontală

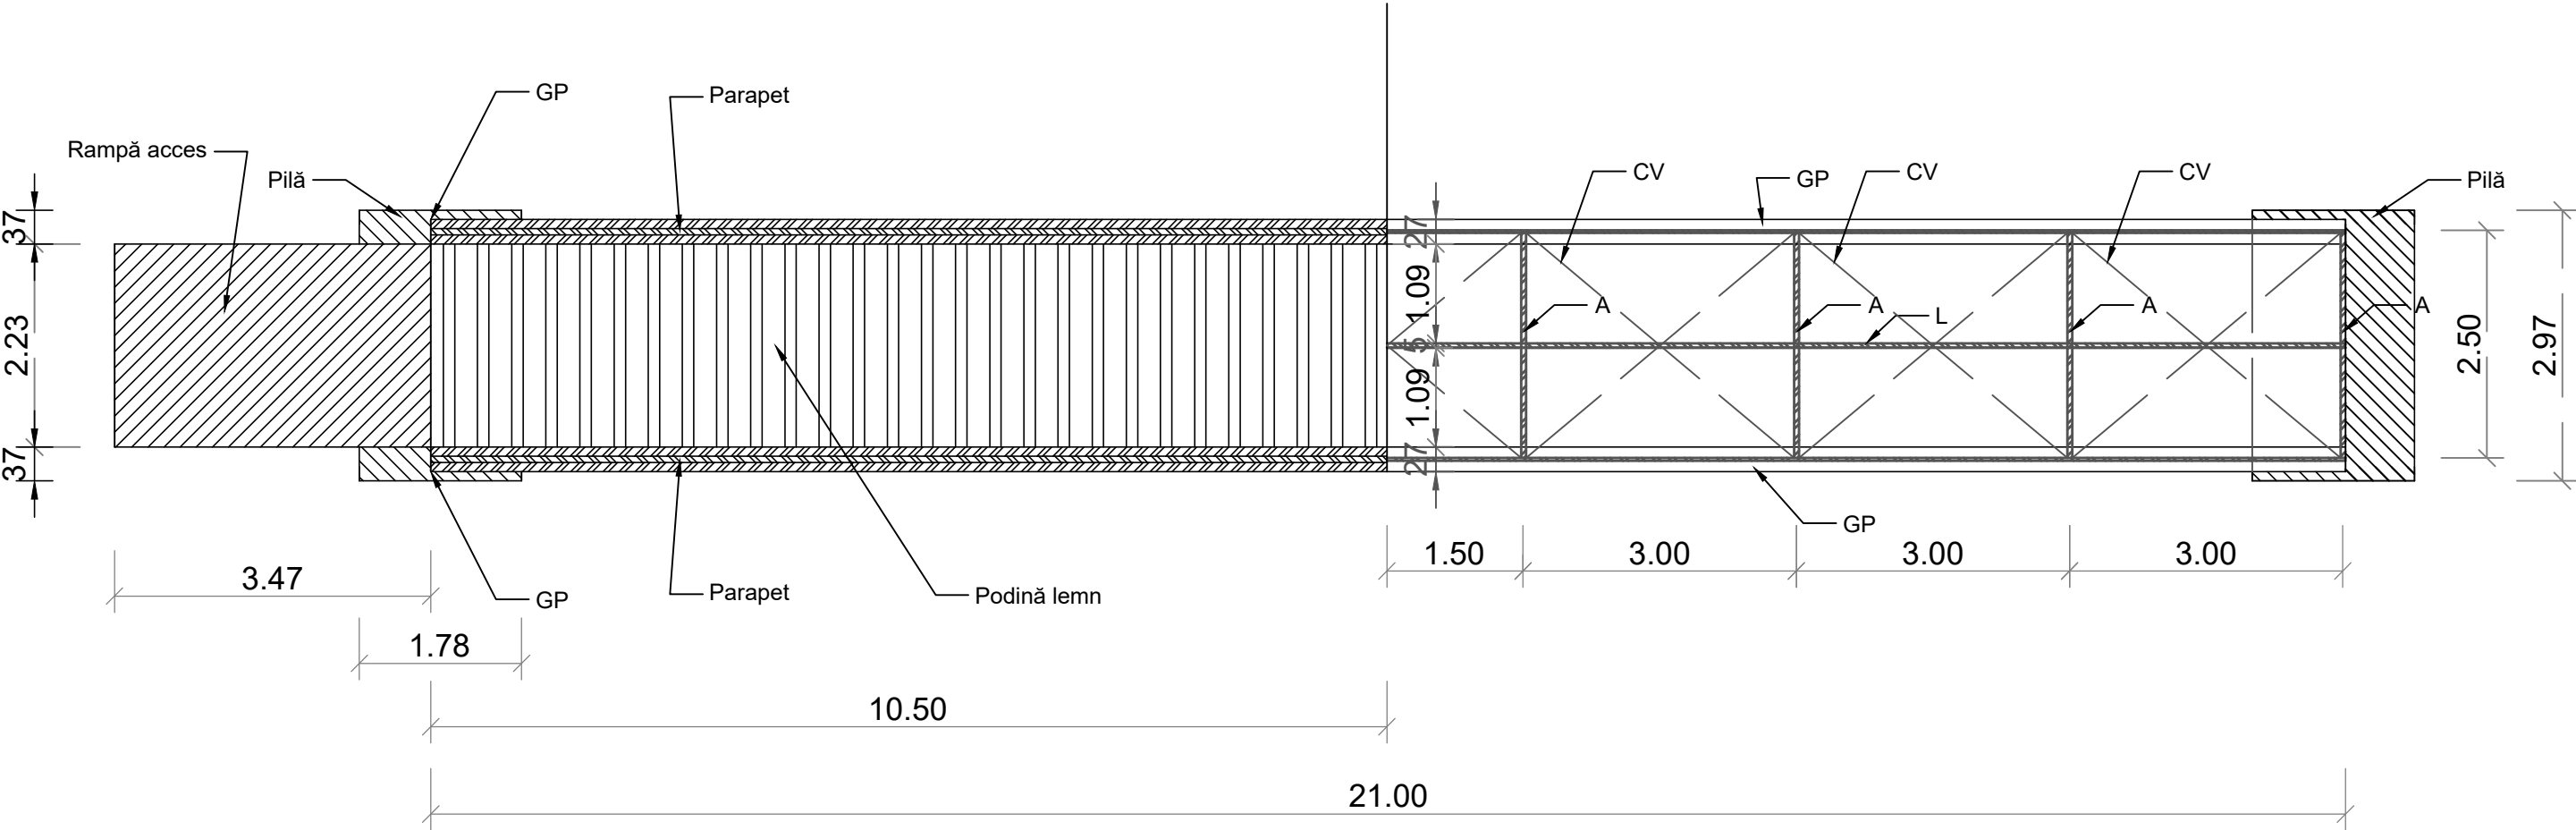


UNIVERSITATEA TEHNICA CLUJ-NAPOCA FACULTATEA DE CONSTRUCTII			Elemente de proiectare a podurilor Anul III, IUDR Grupa 3631 An univeristar 2024-2025		Proiect nr. 1/ 2025
Calitatea	Nume	Semnatura	Scara 1:100	Vedere plană/ Secțiune orizontală	Plansa nr. R.01
SEF PROIECT	Ing. Ionuț Chindriș				
PROIECTAT	Dulli Dávid Patrik				
DESENAT	Dulli Dávid Patrik				
			Data ian. 2025.		

Elevație/Secțiune longitudinală

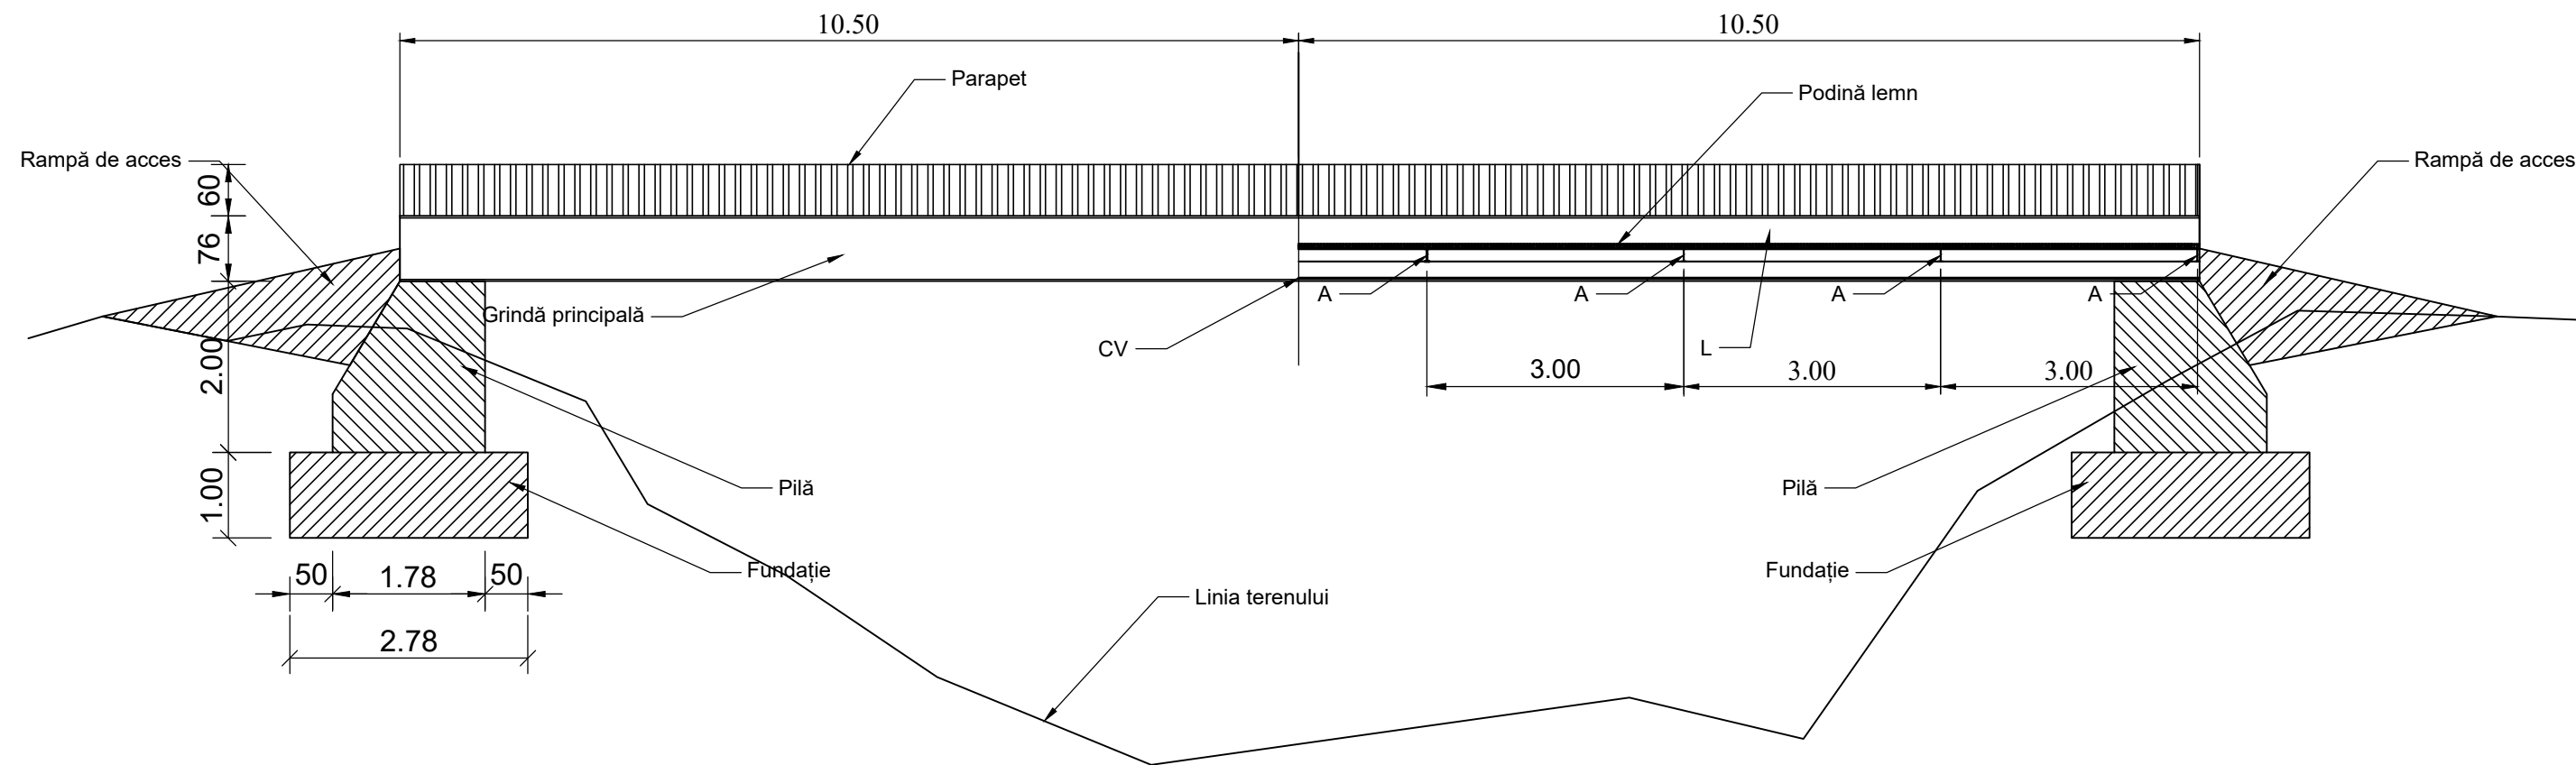

UNIVERSITATEA TEHNICA CLUJ-NAPOCA FACULTATEA DE CONSTRUCTII			Elemente de proiectare a podurilor Anul III, IUDR Grupa 3631 An univeristar 2024-2025		Proiect nr. 1/ 2025
Calitatea	Nume	Semnatura	Scara 1:100	Vedere laterală/ Secțiune longitudinală	Plansa nr. R.02
SEF PROIECT	Ing. Ionuț Chindriș				
PROIECTAT	Dulli Dávid Patrik		Data ian. 2025.		
DESENAT	Dulli Dávid Patrik				

Secțiune transversală B-B

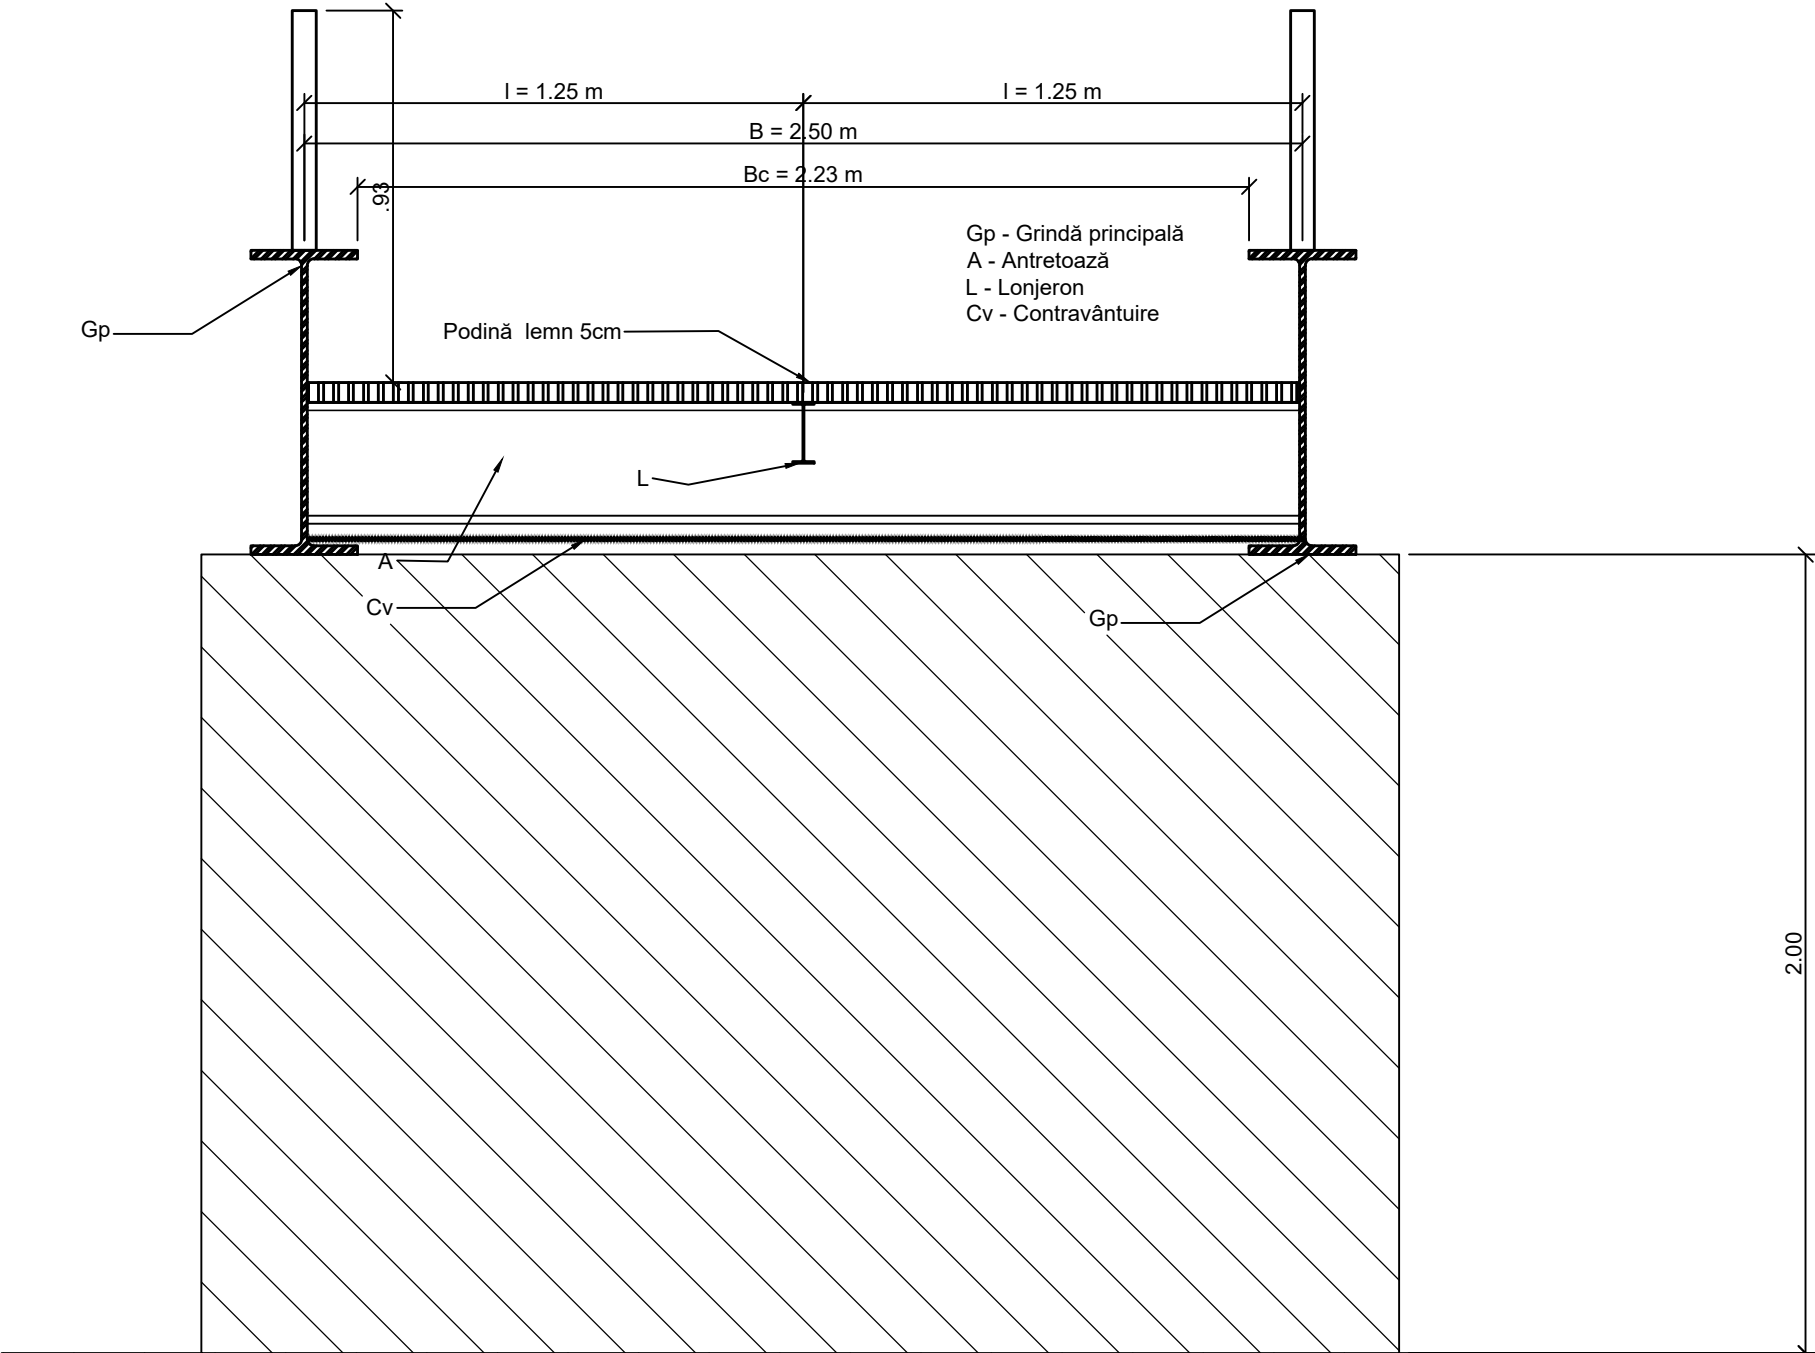

UNIVERSITATEA TEHNICA CLUJ-NAPOCA FACULTATEA DE CONSTRUCȚII			1.00		Elemente de proiectare a podurilor Anul III, IUDR Grupa 3631 An univeristar 2024-2025	Proiect nr. 1/ 2025
Calitatea	Nume	Semnatura	Scara 1:100	Secțiune transversală	Plansa nr. R.03	
ȘEF PROIECT	Ing. Ionuț Chindriș					
PROIECTAT	Dulli Dávid Patrik		Data			
DESENAT	Dulli Dávid Patrik		ian. 2025.			