


Plan fundații

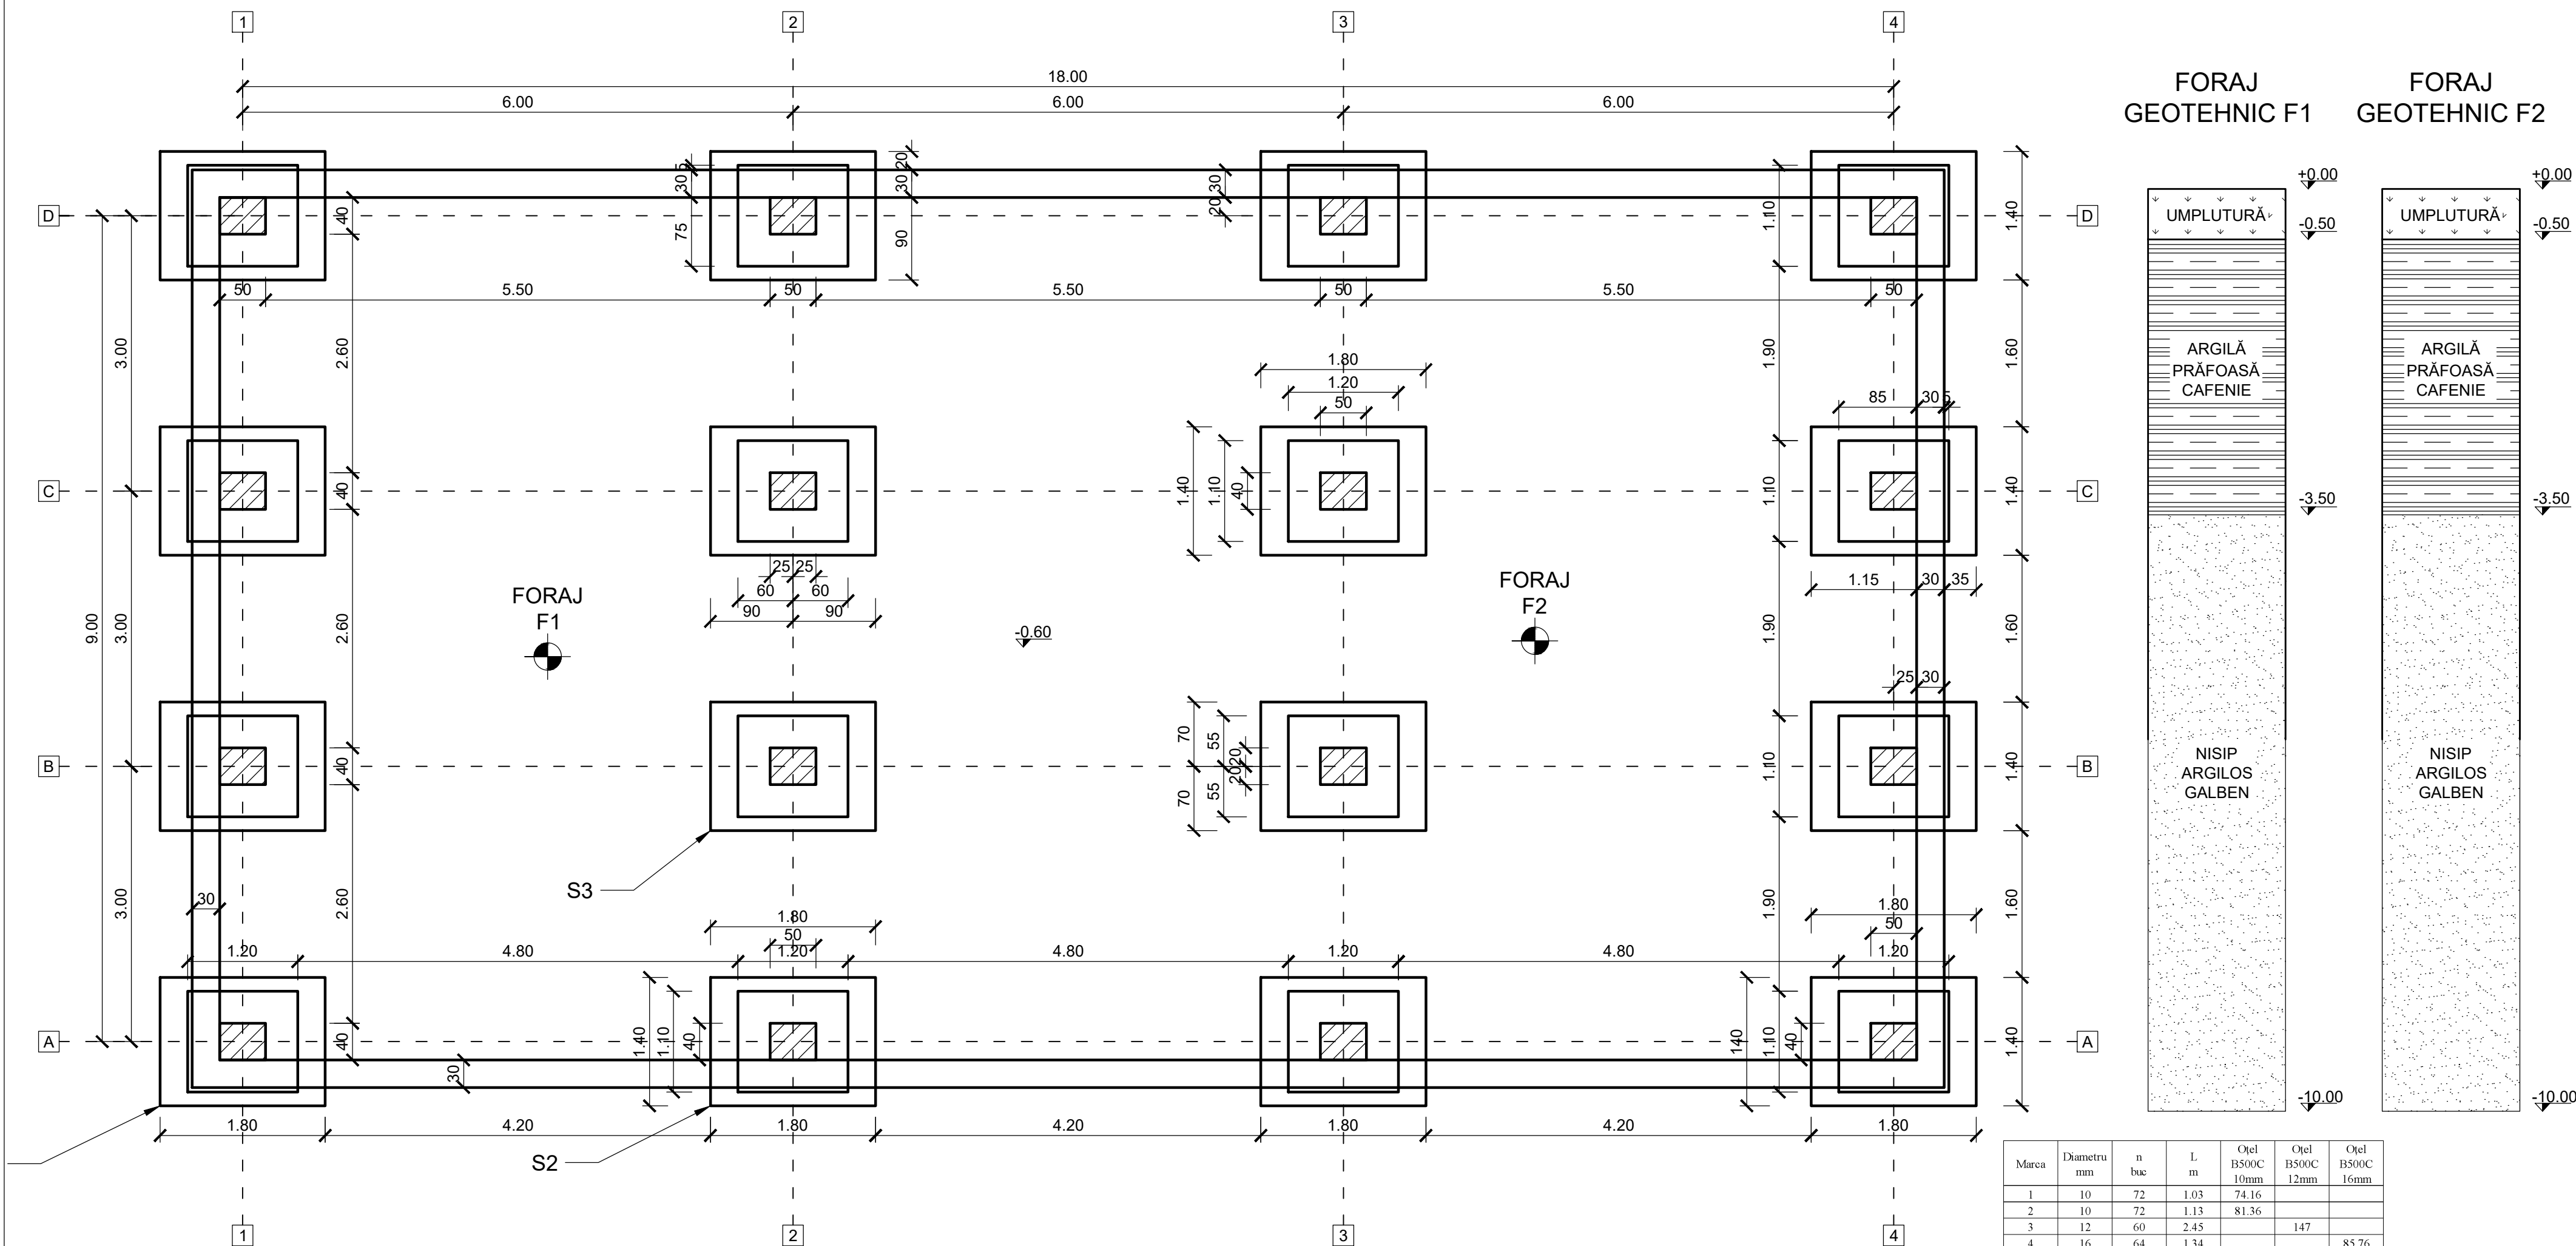




Materiale
C4/5 beton egalizare sub fundație
C30/37 fundații și pereți subsol
Clasă de expunere XA1
A/C max: 0.55
Dozaj ciment minim: 300kg/m³
Conform NE-012-1-2022

Note generale
1.Cotele sunt exprimate în m și cm.
2.Încărcările de calcul sunt cele regăsite în notele de calcul.
3.Riscul geotehnic asociat este de Categoria Geotehnică 1 conform SR-EN-1997-1.
4.Seismicitate: ag=0.1g
5.Calculul fundațiilor s-a realizat conform NP112-2022

Marca	Diametru mm	n buc	L m	Oțel B500C 10mm	Oțel B500C 12mm	Oțel B500C 16mm
1	10	72	1.03	74.16		
2	10	72	1.13	81.36		
3	12	60	2.45		147	
4	16	64	1.34			85.76
5	16	128	4.6			588.8
6	16	64	1.94			124.16
7	10	320	1.6	512		
8	10	320	1.16	371.2		
9	10	180	1.57	282.6		
10	10	40	1.43	57.2		
11	12	48	1.73		83.04	
Total lungime pe diametru (m)				1378.52	230.04	798.72
Greutate pe metru (kg/m)				0.617	0.88	1.503
Greutate pe diametru (kg)				850.3468	202.4352	1200.476
Greutate totala				2253.4582		



UNIVERSITATEA TEHNICA CLUJ-NAPOCA FACULTATEA DE CONSTRUCTII			Fundații Anul IV, Sectia IUDR Grupa 3641 An univeristar 2025-2026		Proiect nr. 1/2026
Calitatea	Nume	Semnatura	Scara 1:20	Plan fundații	Plansa nr. 1
SEF PROIECT	Ing. Iulia C. Prodan				
PROIECTAT	Dulli David Patrik		Data ian. 2026		
DESENAT	Dulli David Patrik				

SECȚIUNE 2-2

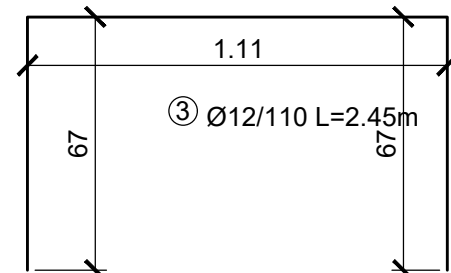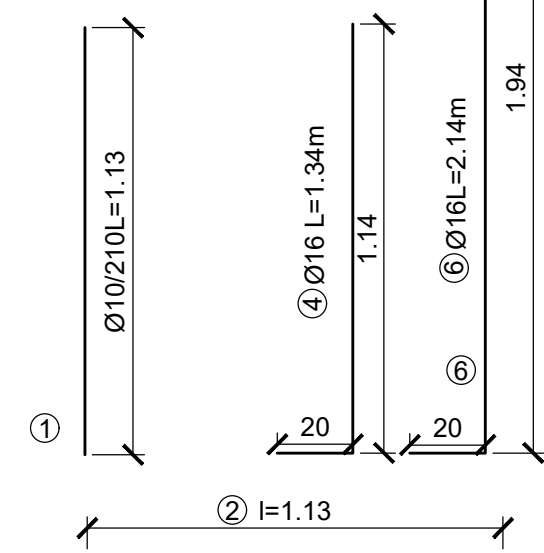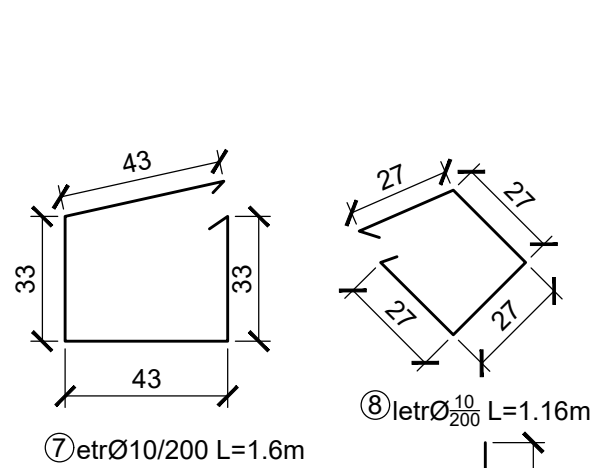


Materiale
C4/5 beton egalizare sub fundație
C30/37 fundații și pereți subsol
Clasă de expunere XA1
A/C max: 0.55
Dozaj ciment minim: 300kg/m³
Conform NE-012-1-2022

Note generale
1.Cotele sunt exprimate în m și cm.
2.Încărcările de calcul sunt cele regăsite în notele de calcul.
3.Riscul geotehnic asociat este de Categoria Geotehnică 1 conform SR-EN-1997-1.
4.Seismicitate: ag=0.1g
5.Calculul fundațiilor s-a realizat conform NP112-2022.

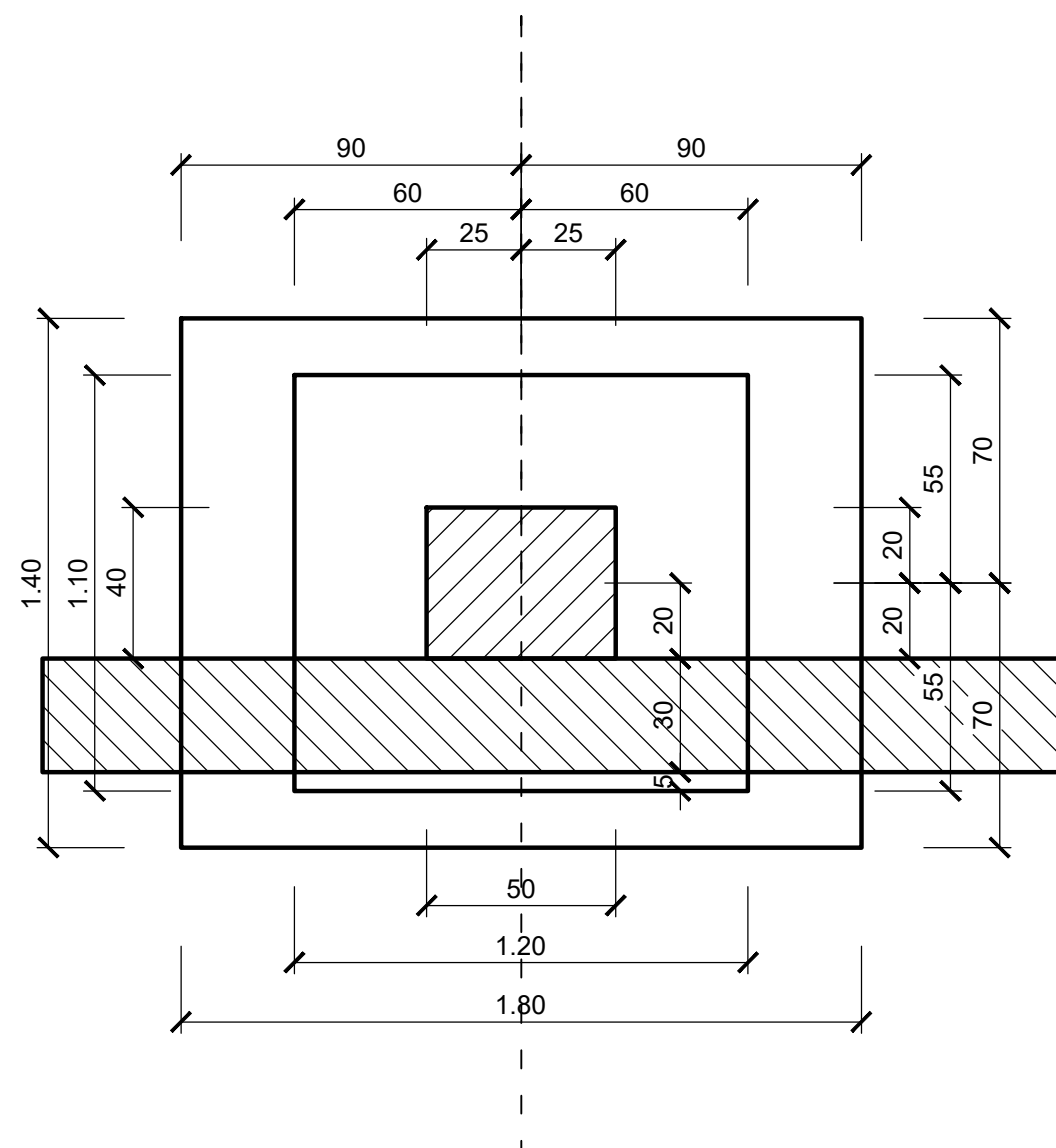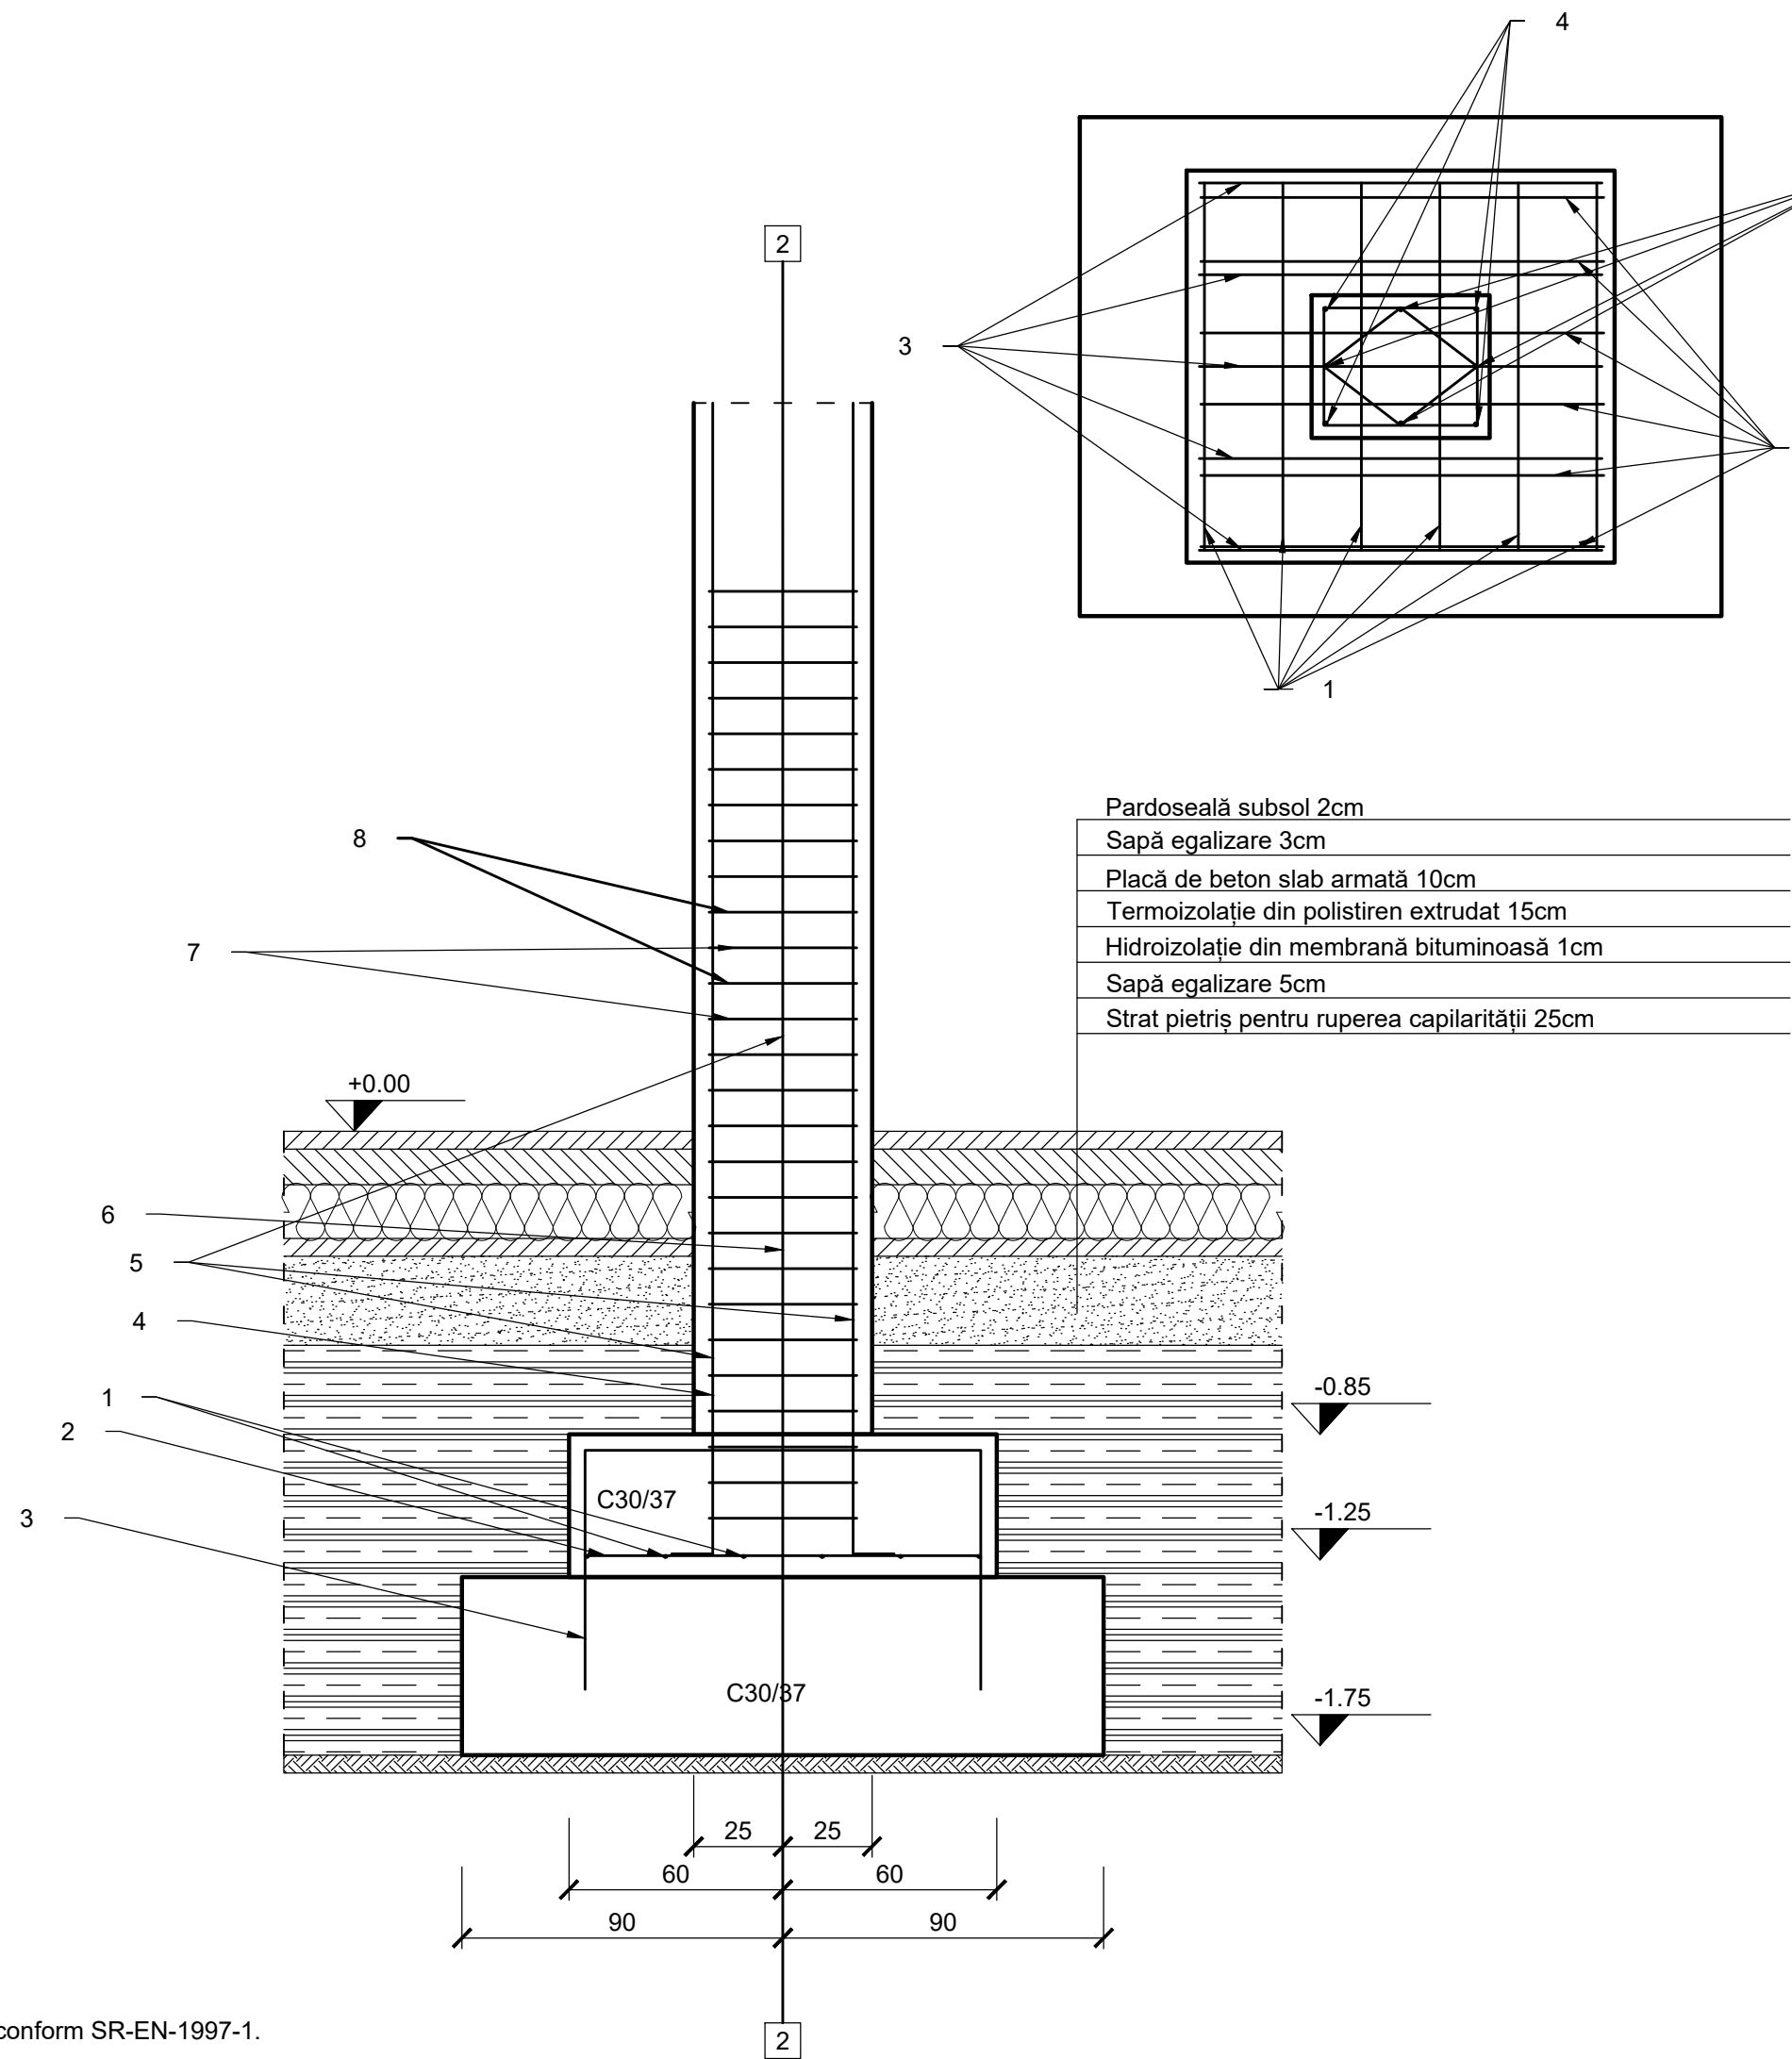

UNIVERSITATEA TEHNICA CLUJ-NAPOCA FACULTATEA DE CONSTRUCȚII			Fundații Anul IV, Secția IUDR Grupa 3641 An universitar 2025-2026		Proiect nr. 1/2026
Calitatea	Nume	Semnatura	Scara 1:20	Detaliu 2-2	Planșa nr. 2
SEF PROIECT	Ing. Iulia C. Prodan				
PROIECTAT	Dulli David Patrik				
DESENAT	Dulli David Patrik		Data ian. 2026		

SECȚIUNE 1-1



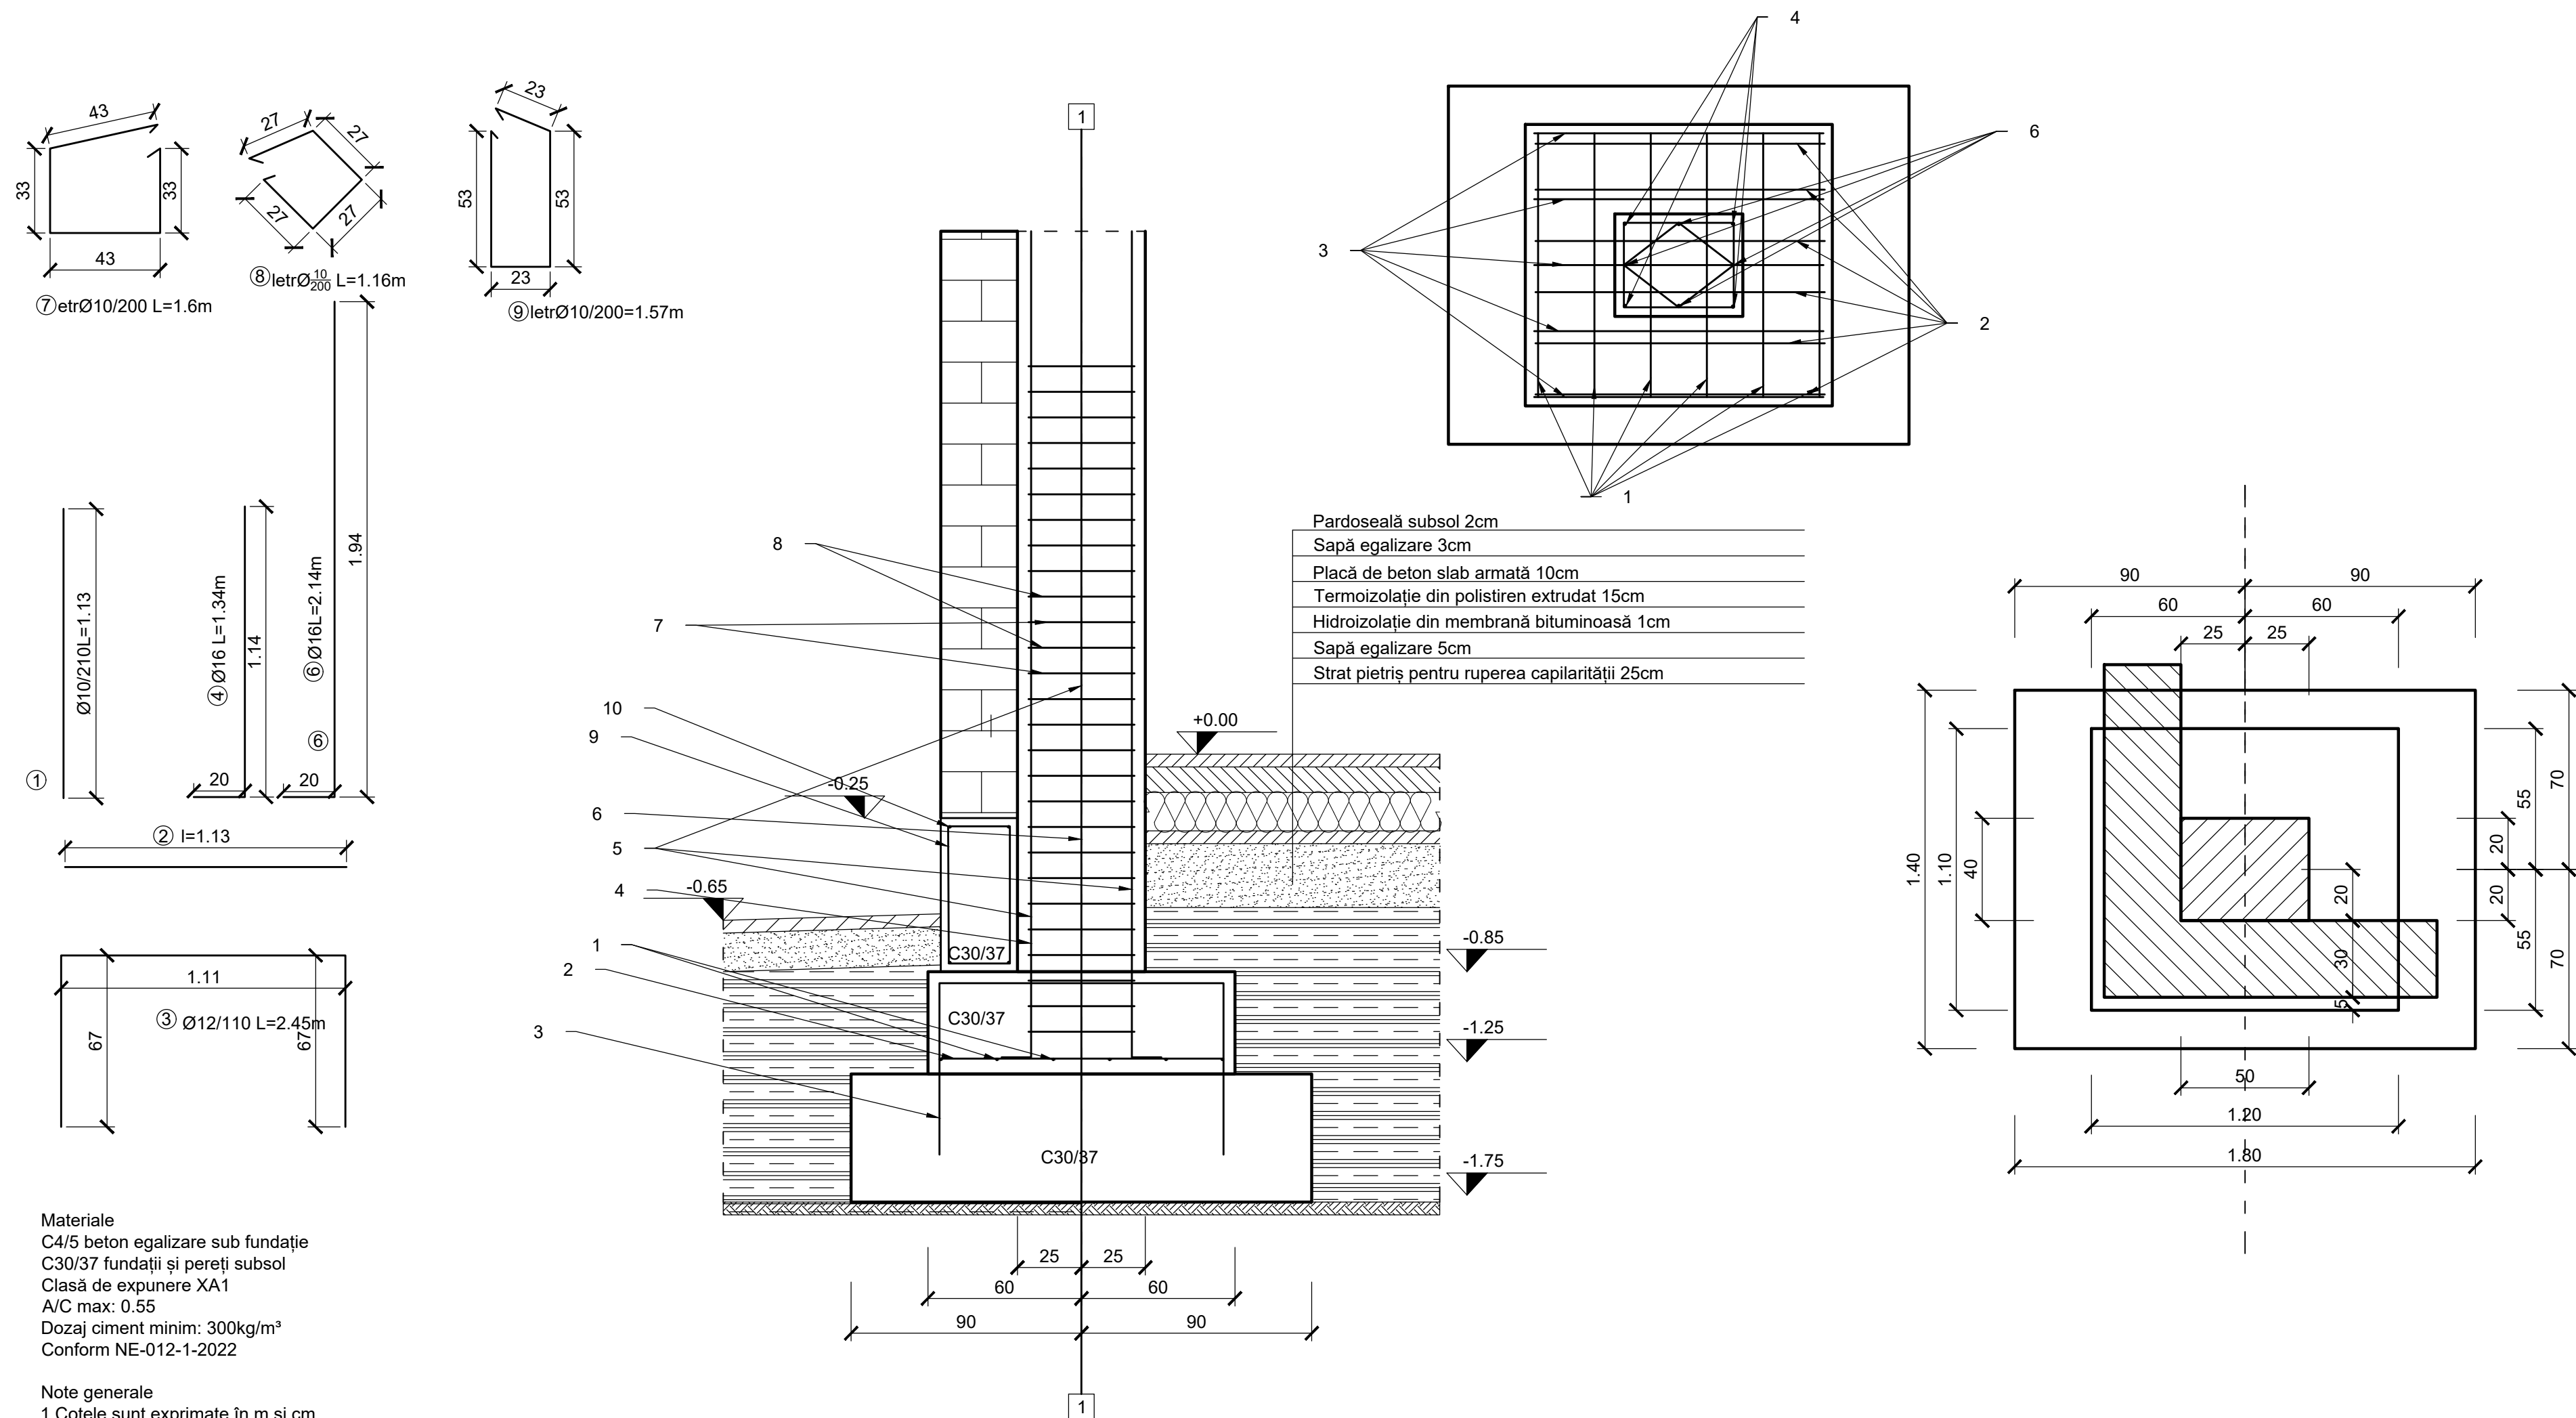


Materiale
C4/5 beton egalizare sub fundație
C30/37 fundații și pereți subsol
Clasă de expunere XA1
A/C max: 0.55
Dozaj ciment minim: 300kg/m³
Conform NE-012-1-2022

Note generale
1.Cotele sunt exprimate în m și cm.
2.Încărcările de calcul sunt cele regăsite în notele de calcul.
3.Riscul geotehnic asociat este de Categoria Geotehnică 1 conform SR-EN-1997-1.
4.Seismicitate: ag=0.1g
5.Calculul fundațiilor s-a realizat conform NP112-2022.

UNIVERSITATEA TEHNICA CLUJ-NAPOCA FACULTATEA DE CONSTRUCTII			Fundații Anul IV, Secția IUDR Grupa 3641 An universitar 2025-2026		Proiect nr. 1/2026
Calitatea	Nume	Semnatura	Scara 1:20	Detaliu 1-1	Plansa nr. 3
SEF PROIECT	Ing. Iulia C. Prodan				
PROIECTAT	Dulli David Patrik		Data ian. 2026		
DESENAT	Dulli David Patrik				



SECȚIUNE 3-3

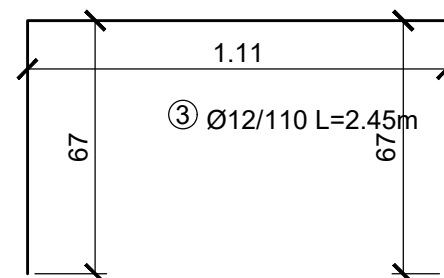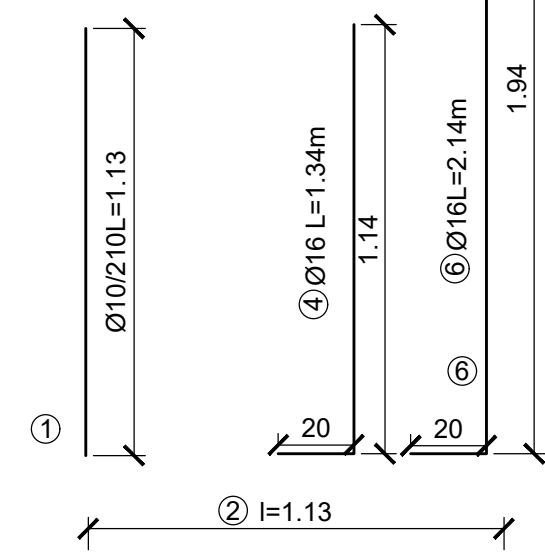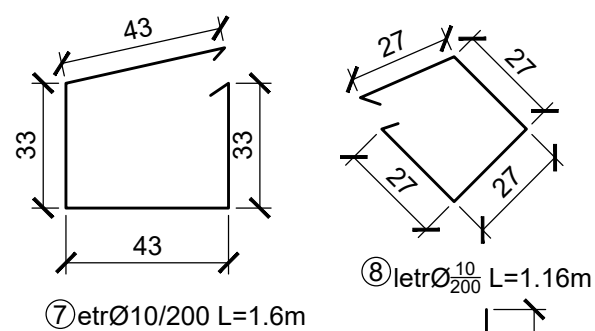

Materiale
C4/5 beton egalizare sub fundație
C30/37 fundații și pereți subsol
Clasă de expunere XA1
A/C max: 0.55
Dozaj ciment minim: 300kg/m³
Conform NE-012-1-2022

Note generale

- 1.Cotele sunt exprimate în m și cm.
- 2.Încărcările de calcul sunt cele regăsite în notele de calcul.
- 3.Riscul de geotehnic asociat este de Categoria Geotehnică 1 conform SR-EN-1997-1.
- 4.Seismicitate: $a_g=0,1g$
- 5.Calculul fundațiilor s-a realizat conform NP112-2022.

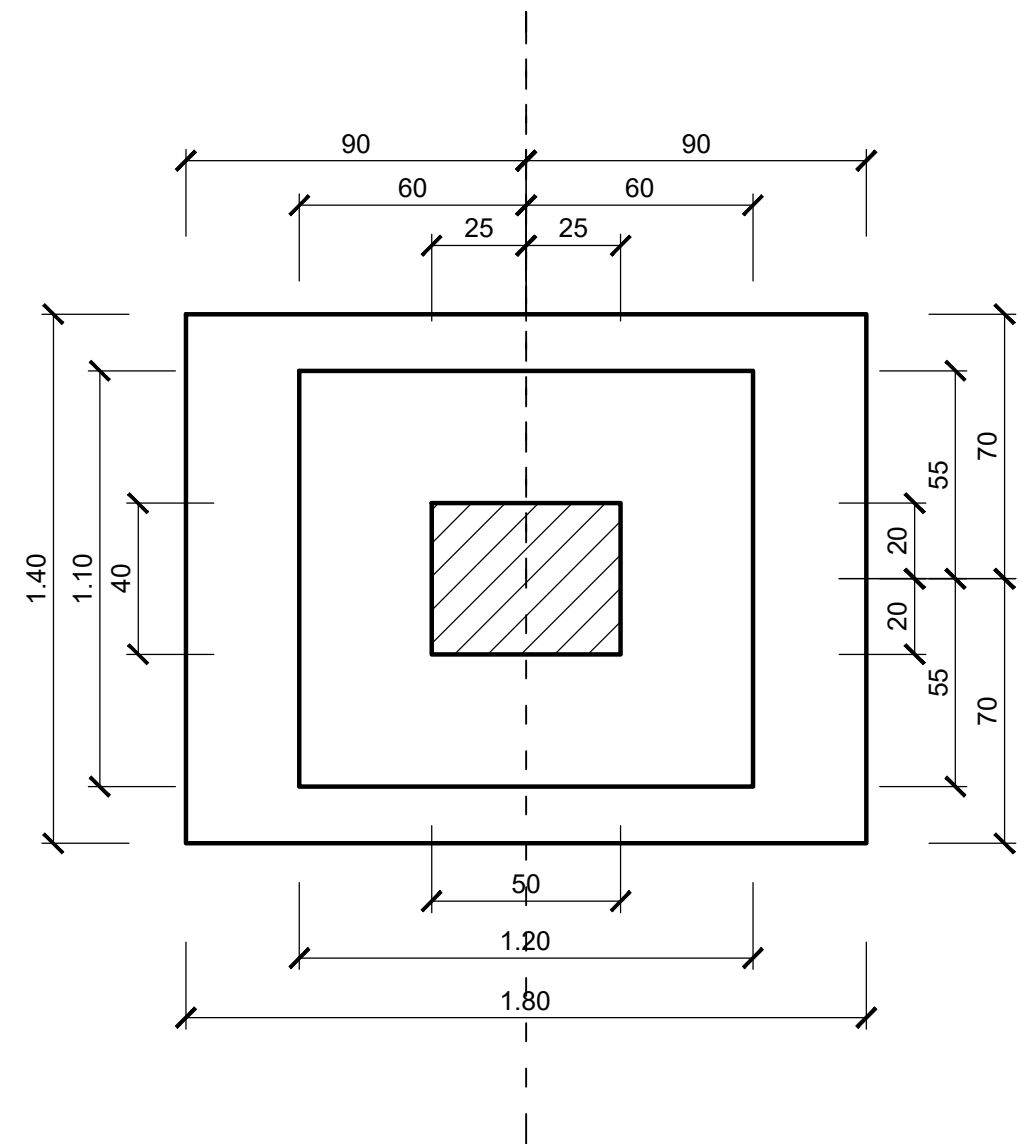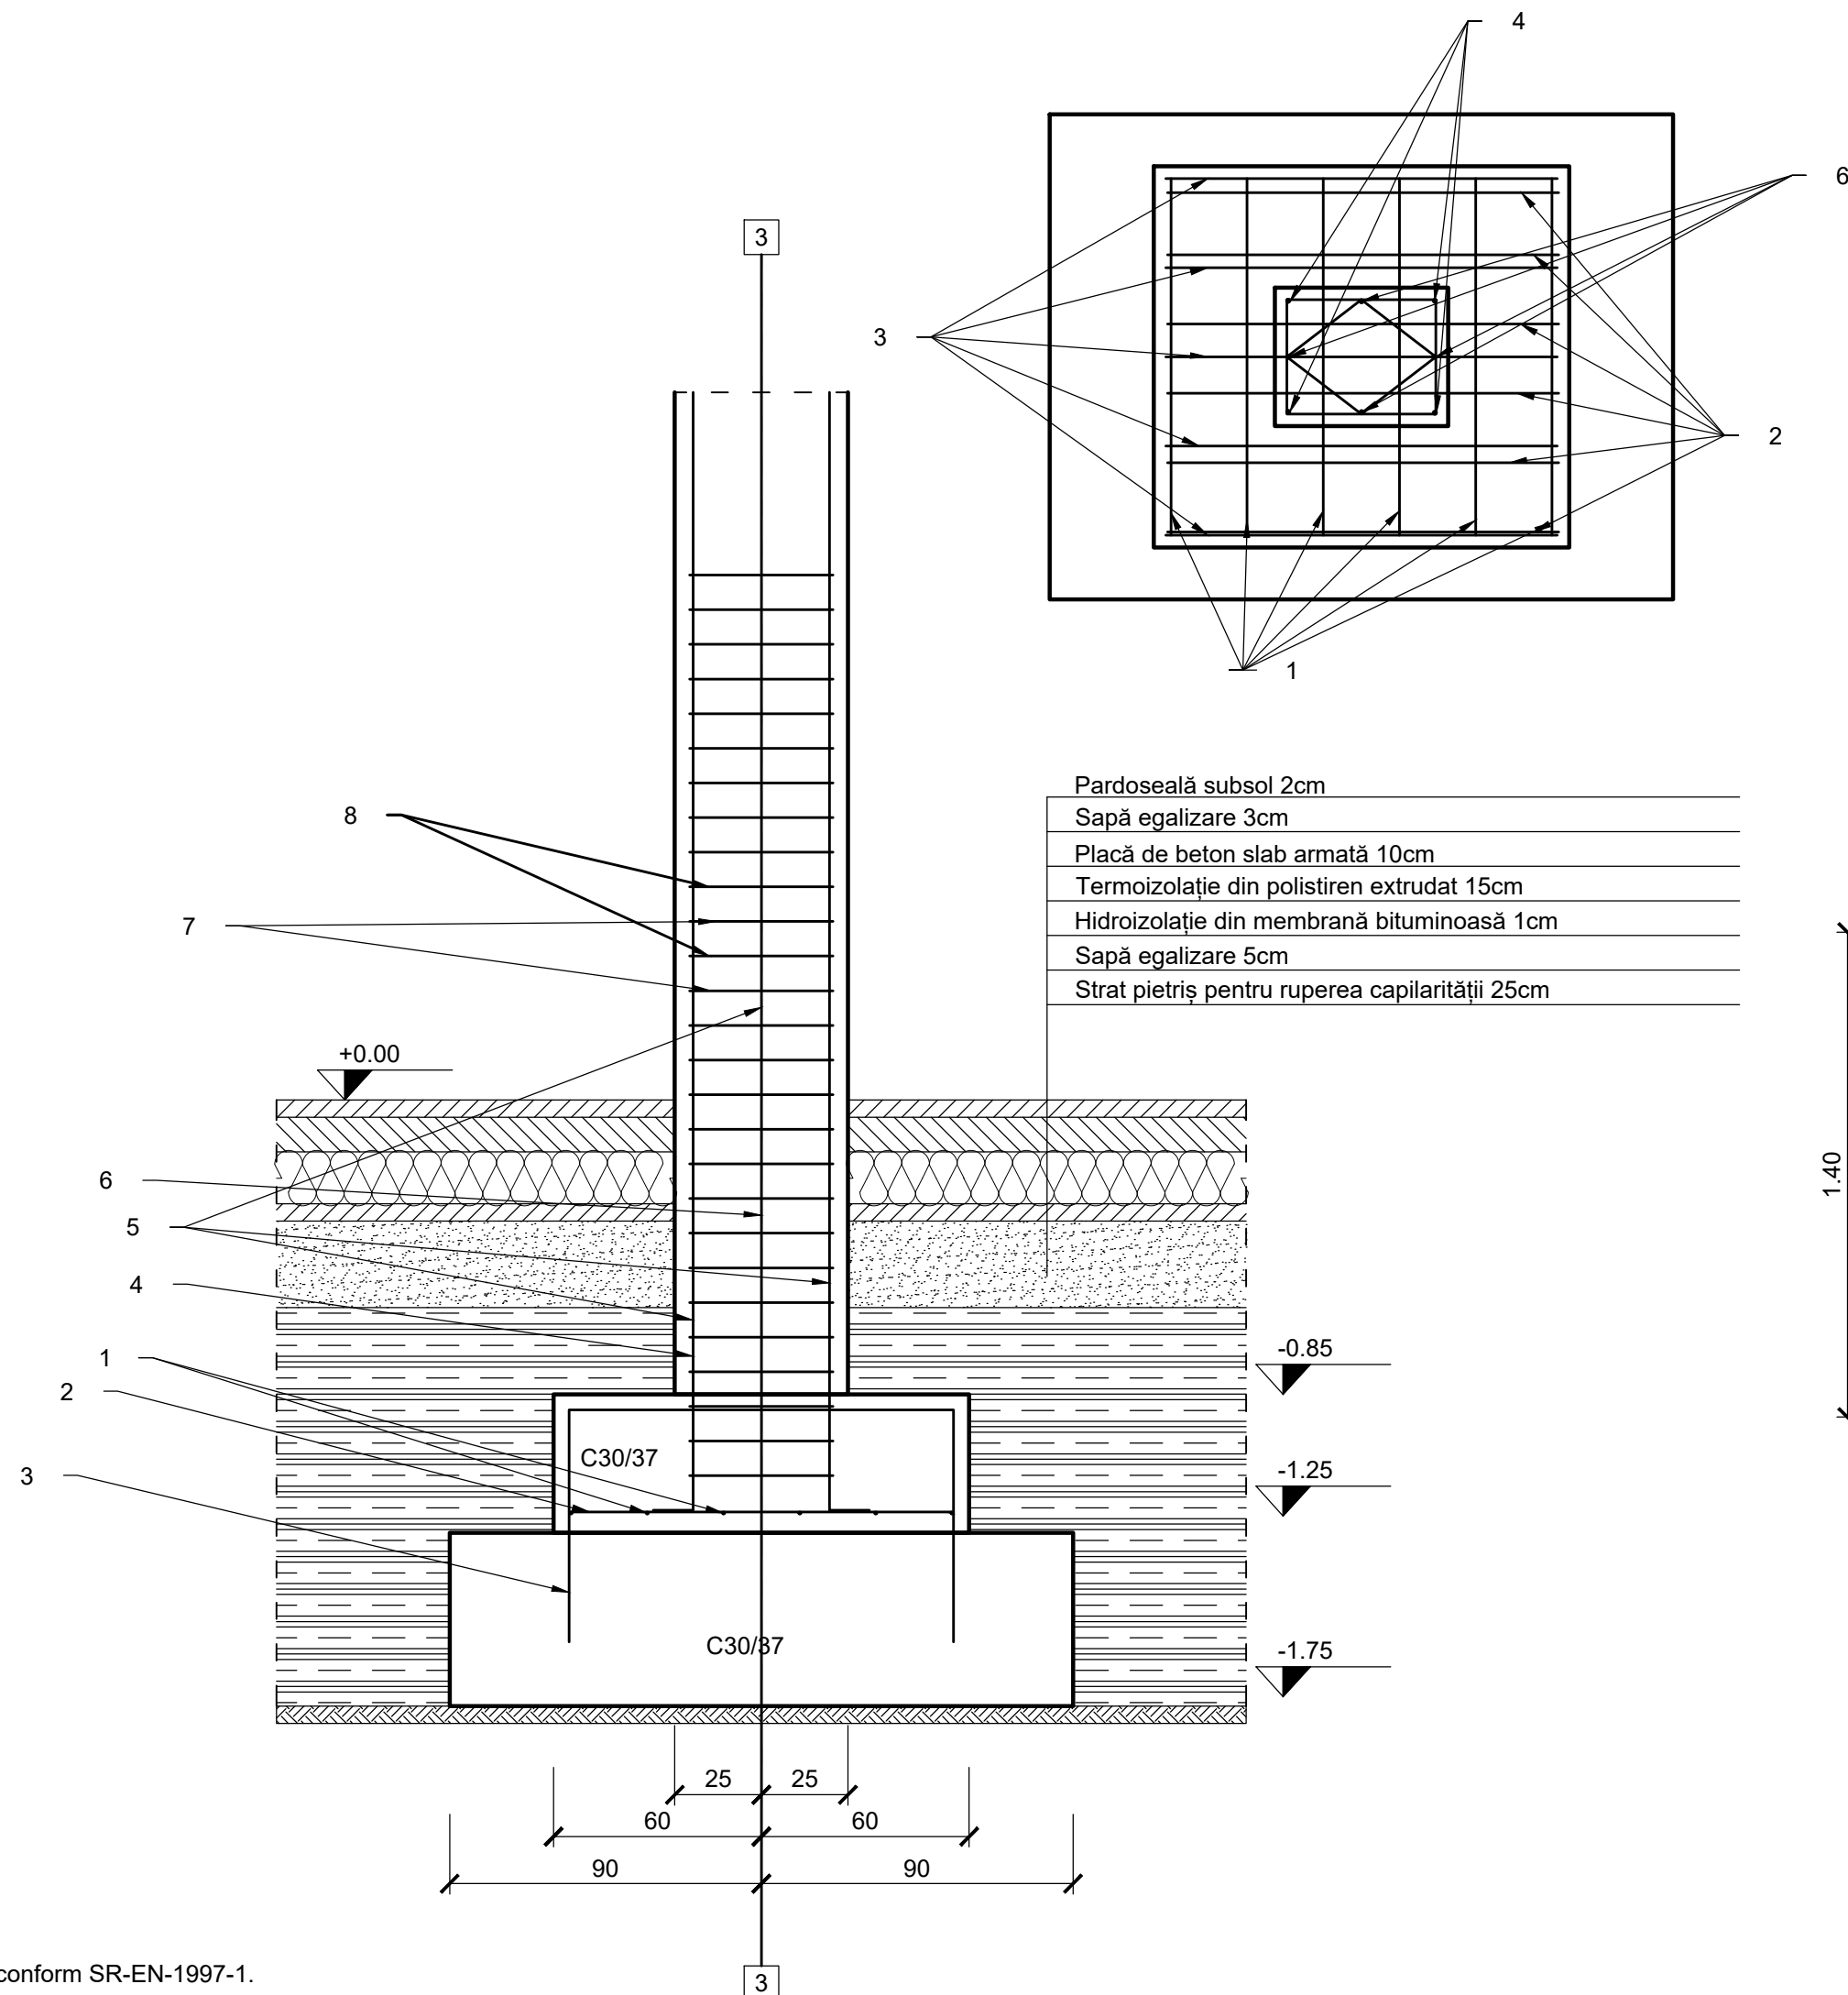

UNIVERSITATEA TEHNICA CLUJ-NAPOCA FACULTATEA DE CONSTRUCTII			Fundații Anul IV, Sectia IUDR Grupa 3641 An univeristar 2025-2026		Proiect nr. 1/2026
Calitatea	Nume	Semnatura	Scara 1:20	Detaliiu 3-3	
ȘEF PROIECT	Ing. Iulia C. Prodan				
PROIECTAT	Dulli David Patrik		Data ian. 2026		Plansa nr. 4
DEȘENAT	Dulli David Patrik				