

ZID DE SPRIJIN ÎN DEBLEU DIN ZIDĂRIE DE PIATRĂ

Secțiune transversală 1:25

Proces tehnologic de execuție

Zidul de sprijin de debleu se execută pe tronsoane alternative de 5 m lungime;

Săpăturile pentru tronsoanele zidului se vor executa cu sprijiniri;

Prezența geotehnicianului este obligatorie, înainte de începerea betonării, în vederea confirmării prezentei stratului bun de fundare;

NU se vor ține săpăturile deschise; betonul de fundație se va turna bine vibrat, aderent la peretii gropii de fundație;

Demontarea sprijinirilor se va realiza pe măsura executării betonării;

Nu se va trece la săpătura tronsonului următor, decât după terminarea completă a tronsonului adiacent anterior;

Zidăria din elevație NU se va întrerupe pe strat de beton, și se vor lăsa pietre în relief, spre a se realiza în continuare zidăria;

Concomitent cu aceasta se va realiza drenul din spatele zidului;


Evacuarea apelor din spatele zidului se va face prin barbacane din tuburi de PVC Ø110 mm;

Pe tot timpul execuției lucrărilor, zona de lucru se va marca cu parapeti de semnalizare și dirijare a circulației, asigurându-se vizibilitatea, atât ziua cât și noaptea;

Se vor respecta toate normele, în vigoare la data execuției lucrărilor, privind semnalizarea lucrărilor de drumuri și de protecția muncii.

Fundație zid de sprijin


Beton C16/20
Oțel PC52/OB37
Clasa de expunere: XC1
Valoare maximă A/C: 0.65
Dozaj minim ciment(kg/m³): 260

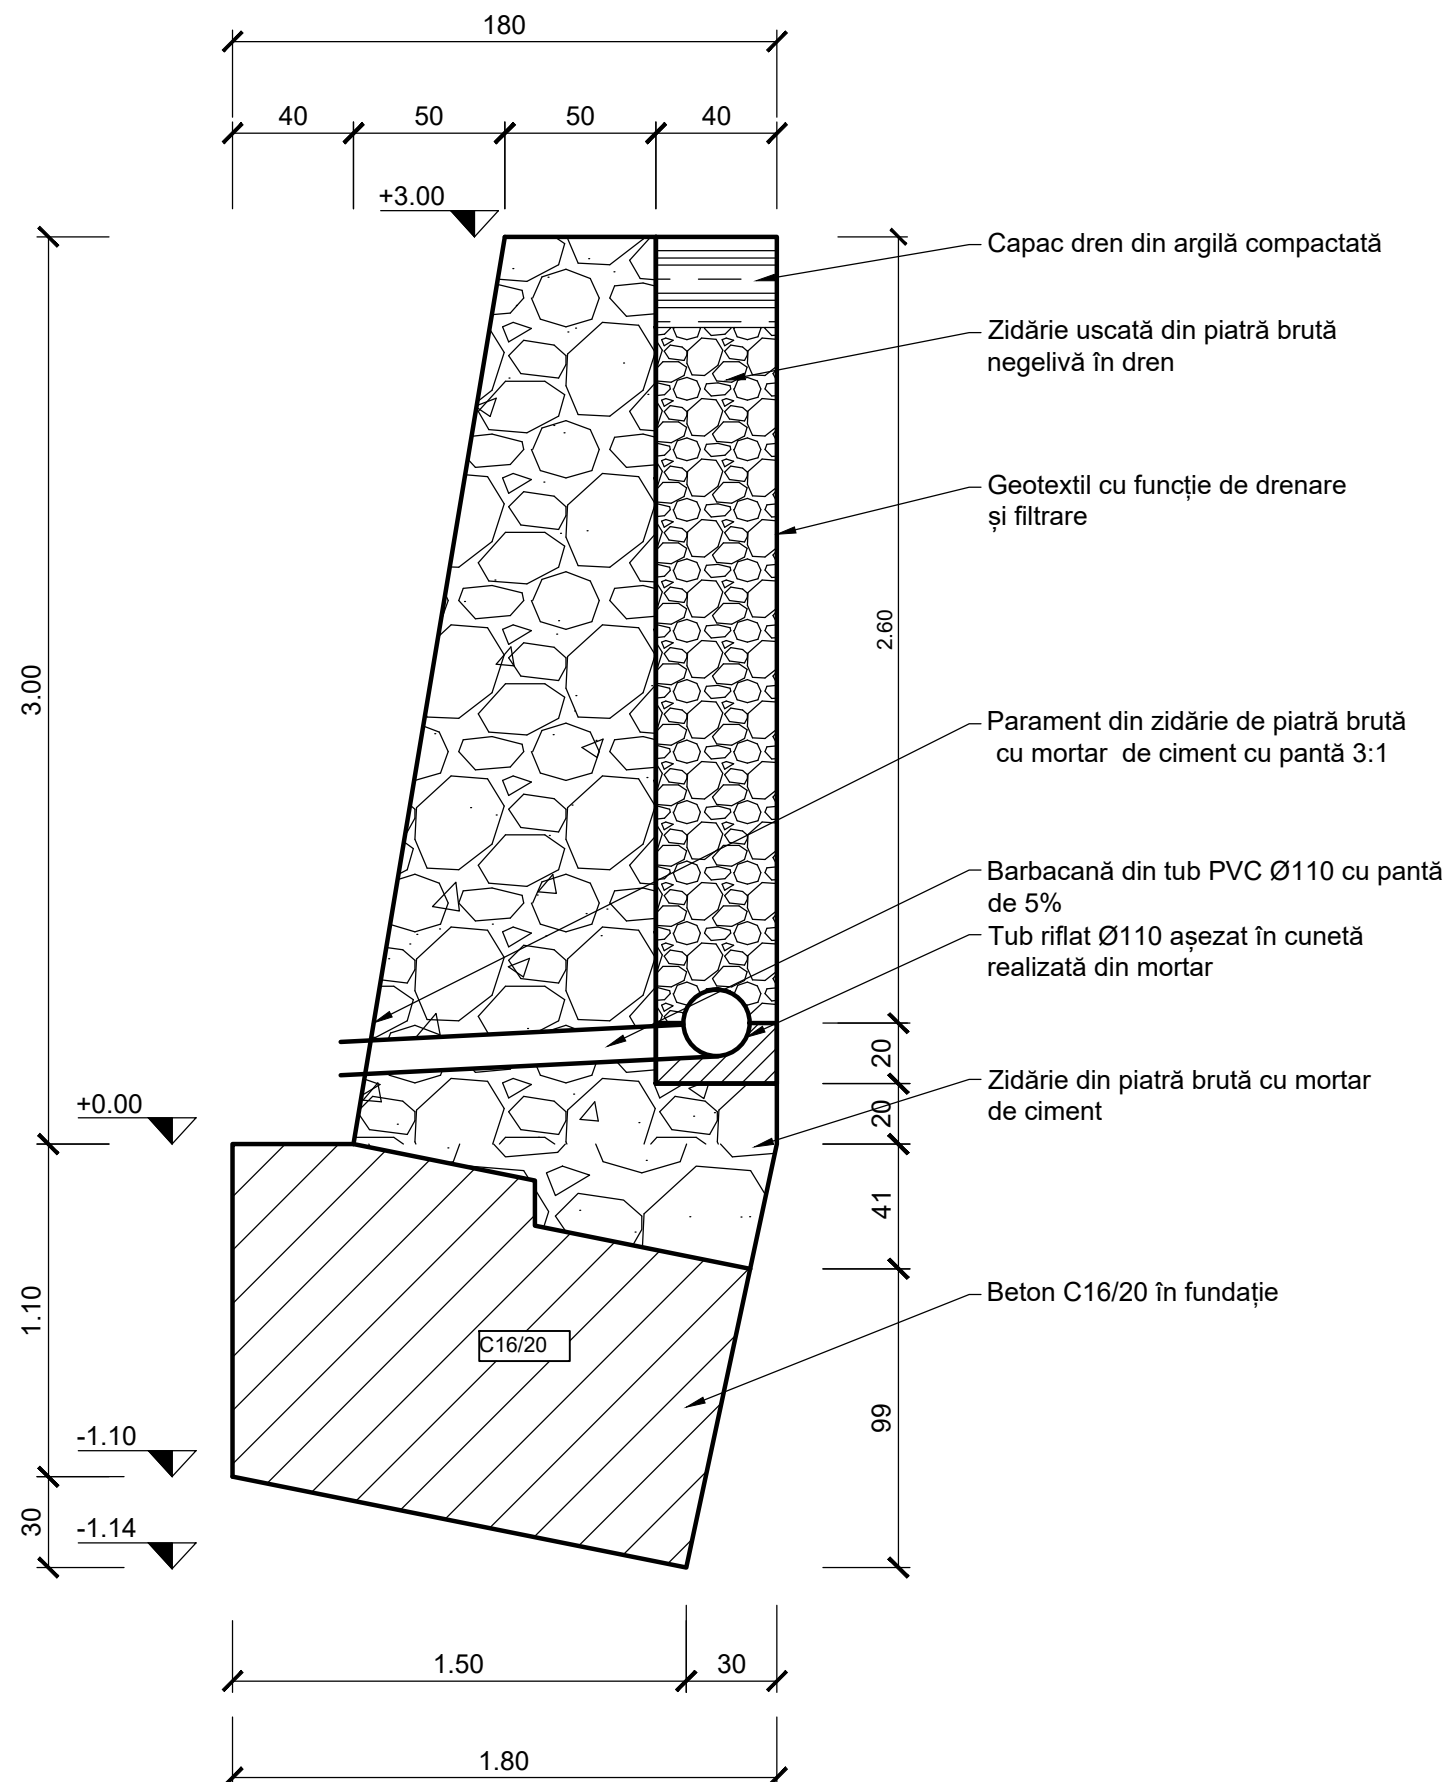

UNIVERSITATEA TEHNICĂ DIN CLUJ-NAPOCA FACULTATEA DE CONSTRUCȚII			FUNDAȚII Anul IV, Specializarea IUDR Grupa 3641 An univeristar 2025-2026		Proiect nr. 1/2025
Calitatea	Nume	Semnătura	Scara 1:25 Data oct. 2025	Secțiune transversală zid de sprijin din zidărie de piatră	Plansa nr. 1
VERIFICAT	Ing. Iulia C. Prodan				
PROIECTAT	Dulli David Patrik				
DESENAT	Dulli David Patrik				

ZID DE SPRIJIN ÎN DEBLEU DIN ZIDĂRIE DE PIATRĂ


Elevație(vederea din față) 1:50

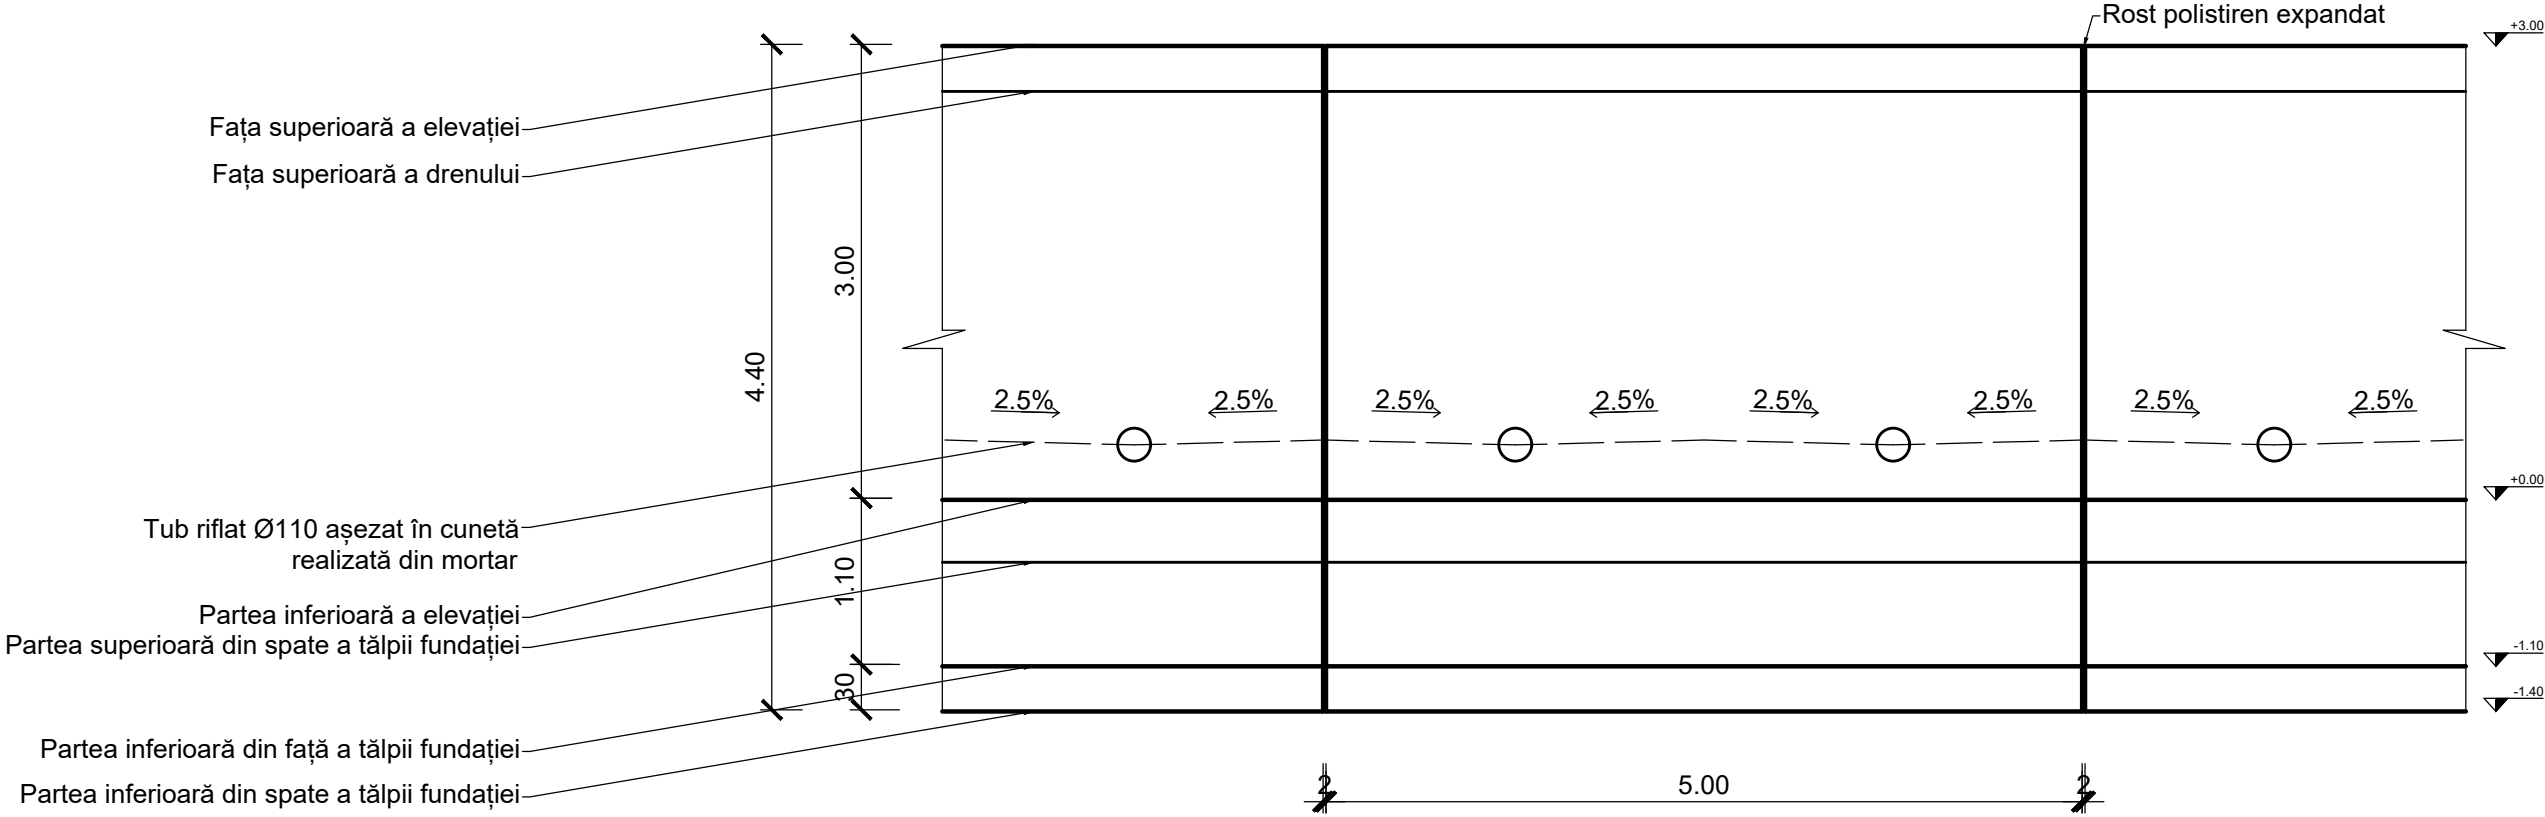

UNIVERSITATEA TEHNICĂ DIN CLUJ-NAPOCA FACULTATEA DE CONSTRUCȚII			FUNDAȚII Anul IV, Specializarea IUDR Grupa 3641 An univeristar 2025-2026		Proiect nr. 1/2025
Calitatea	Nume	Semnătura	Scara 1:50	Profil longitudinal zid de sprijin din zidărie de piatră	
VERIFICAT	Ing. Iulia C. Prodan				
PROIECTAT	Dulli David Patrik		Data oct. 2025		Plansa nr. 2
DESENAT	Dulli David Patrik				

ZID DE SPRIJIN ÎN DEBLEU DIN ZIDĂRIE DE PIATRĂ

Elevație(vederea din față) 1:50

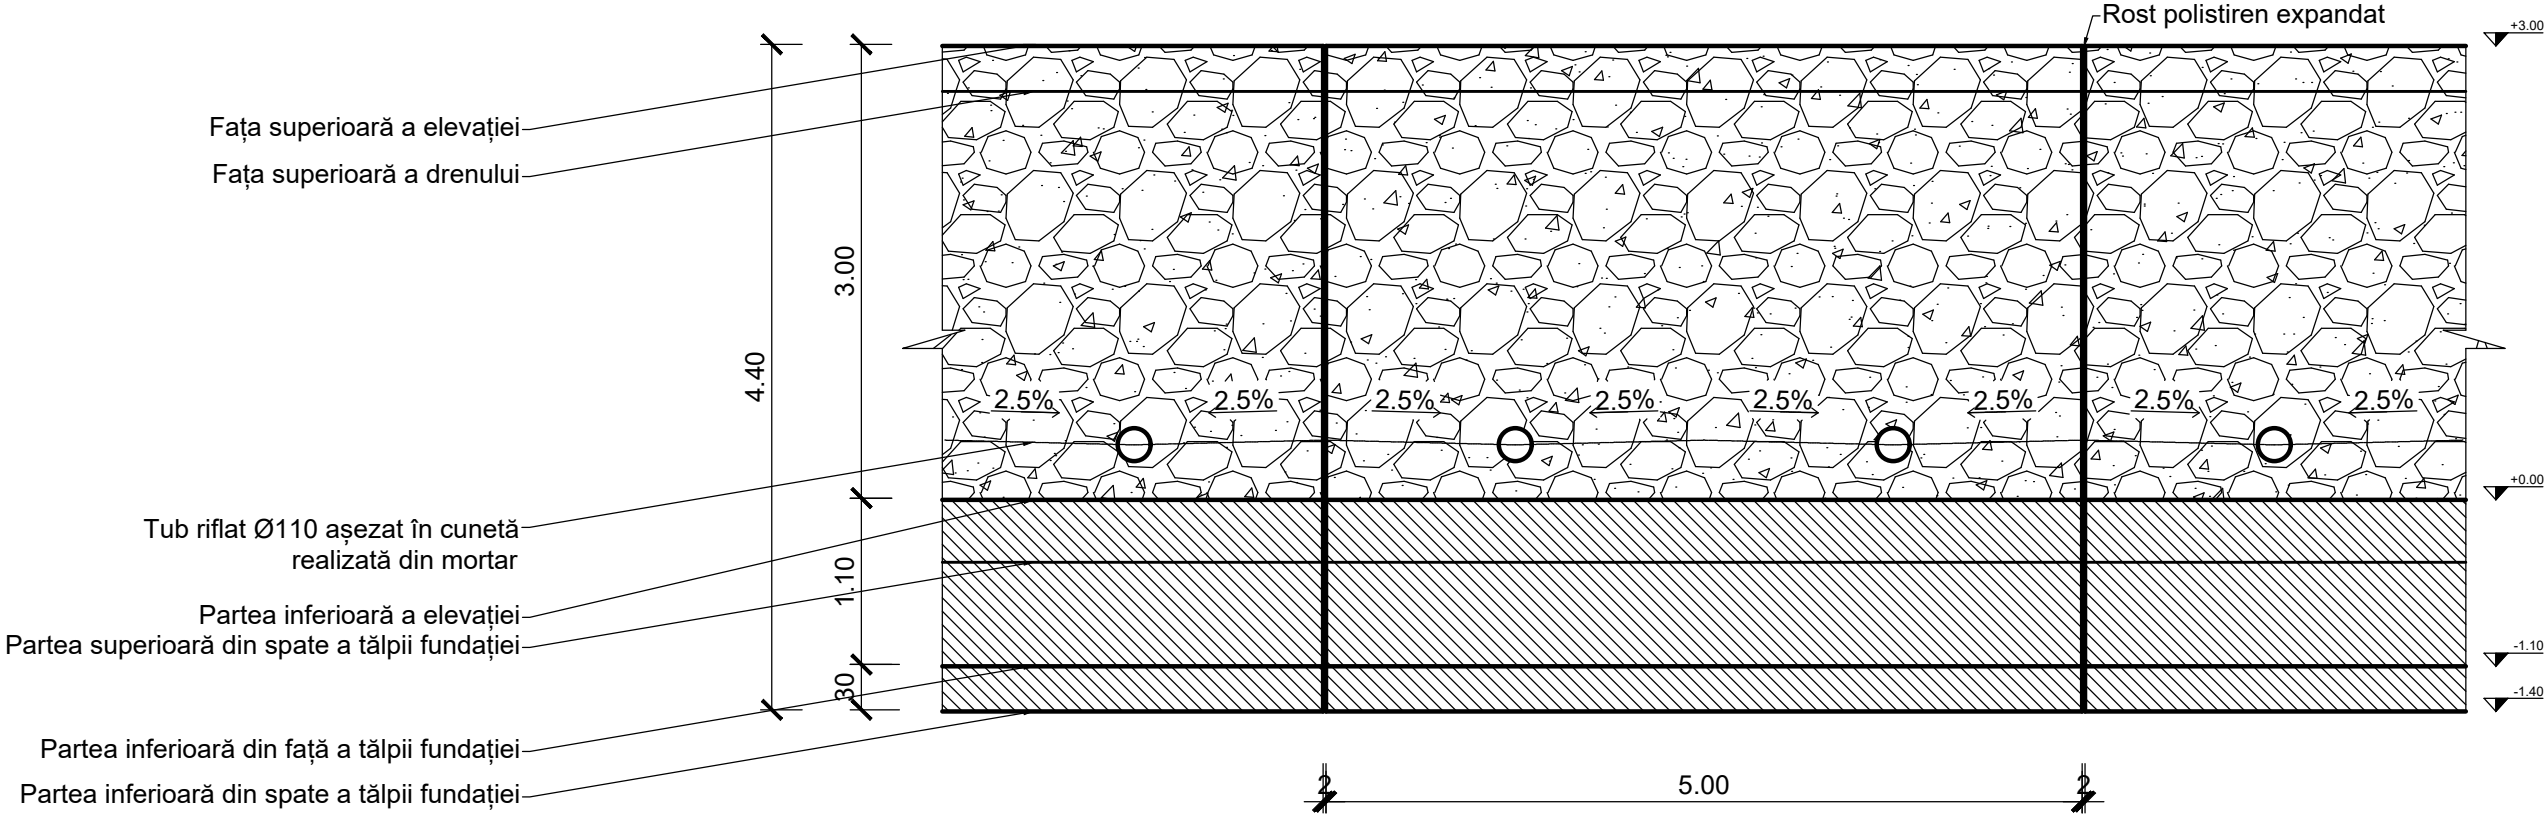

UNIVERSITATEA TEHNICĂ DIN CLUJ-NAPOCA FACULTATEA DE CONSTRUCȚII			FUNDAȚII Anul IV, Specializarea IUDR Grupa 3641 An univeristar 2025-2026		Proiect nr. 1/2025
Calitatea	Nume	Semnătura	Scara 1:50	Elevație zid de sprijin din zidărie de piatră	Plansa nr. 2
VERIFICAT	Ing. Iulia C. Prodan				
PROIECTAT	Dulli David Patrik		Data oct. 2025		
DESENAT	Dulli David Patrik				