




PLAN CENTURI
SCARA 1:50

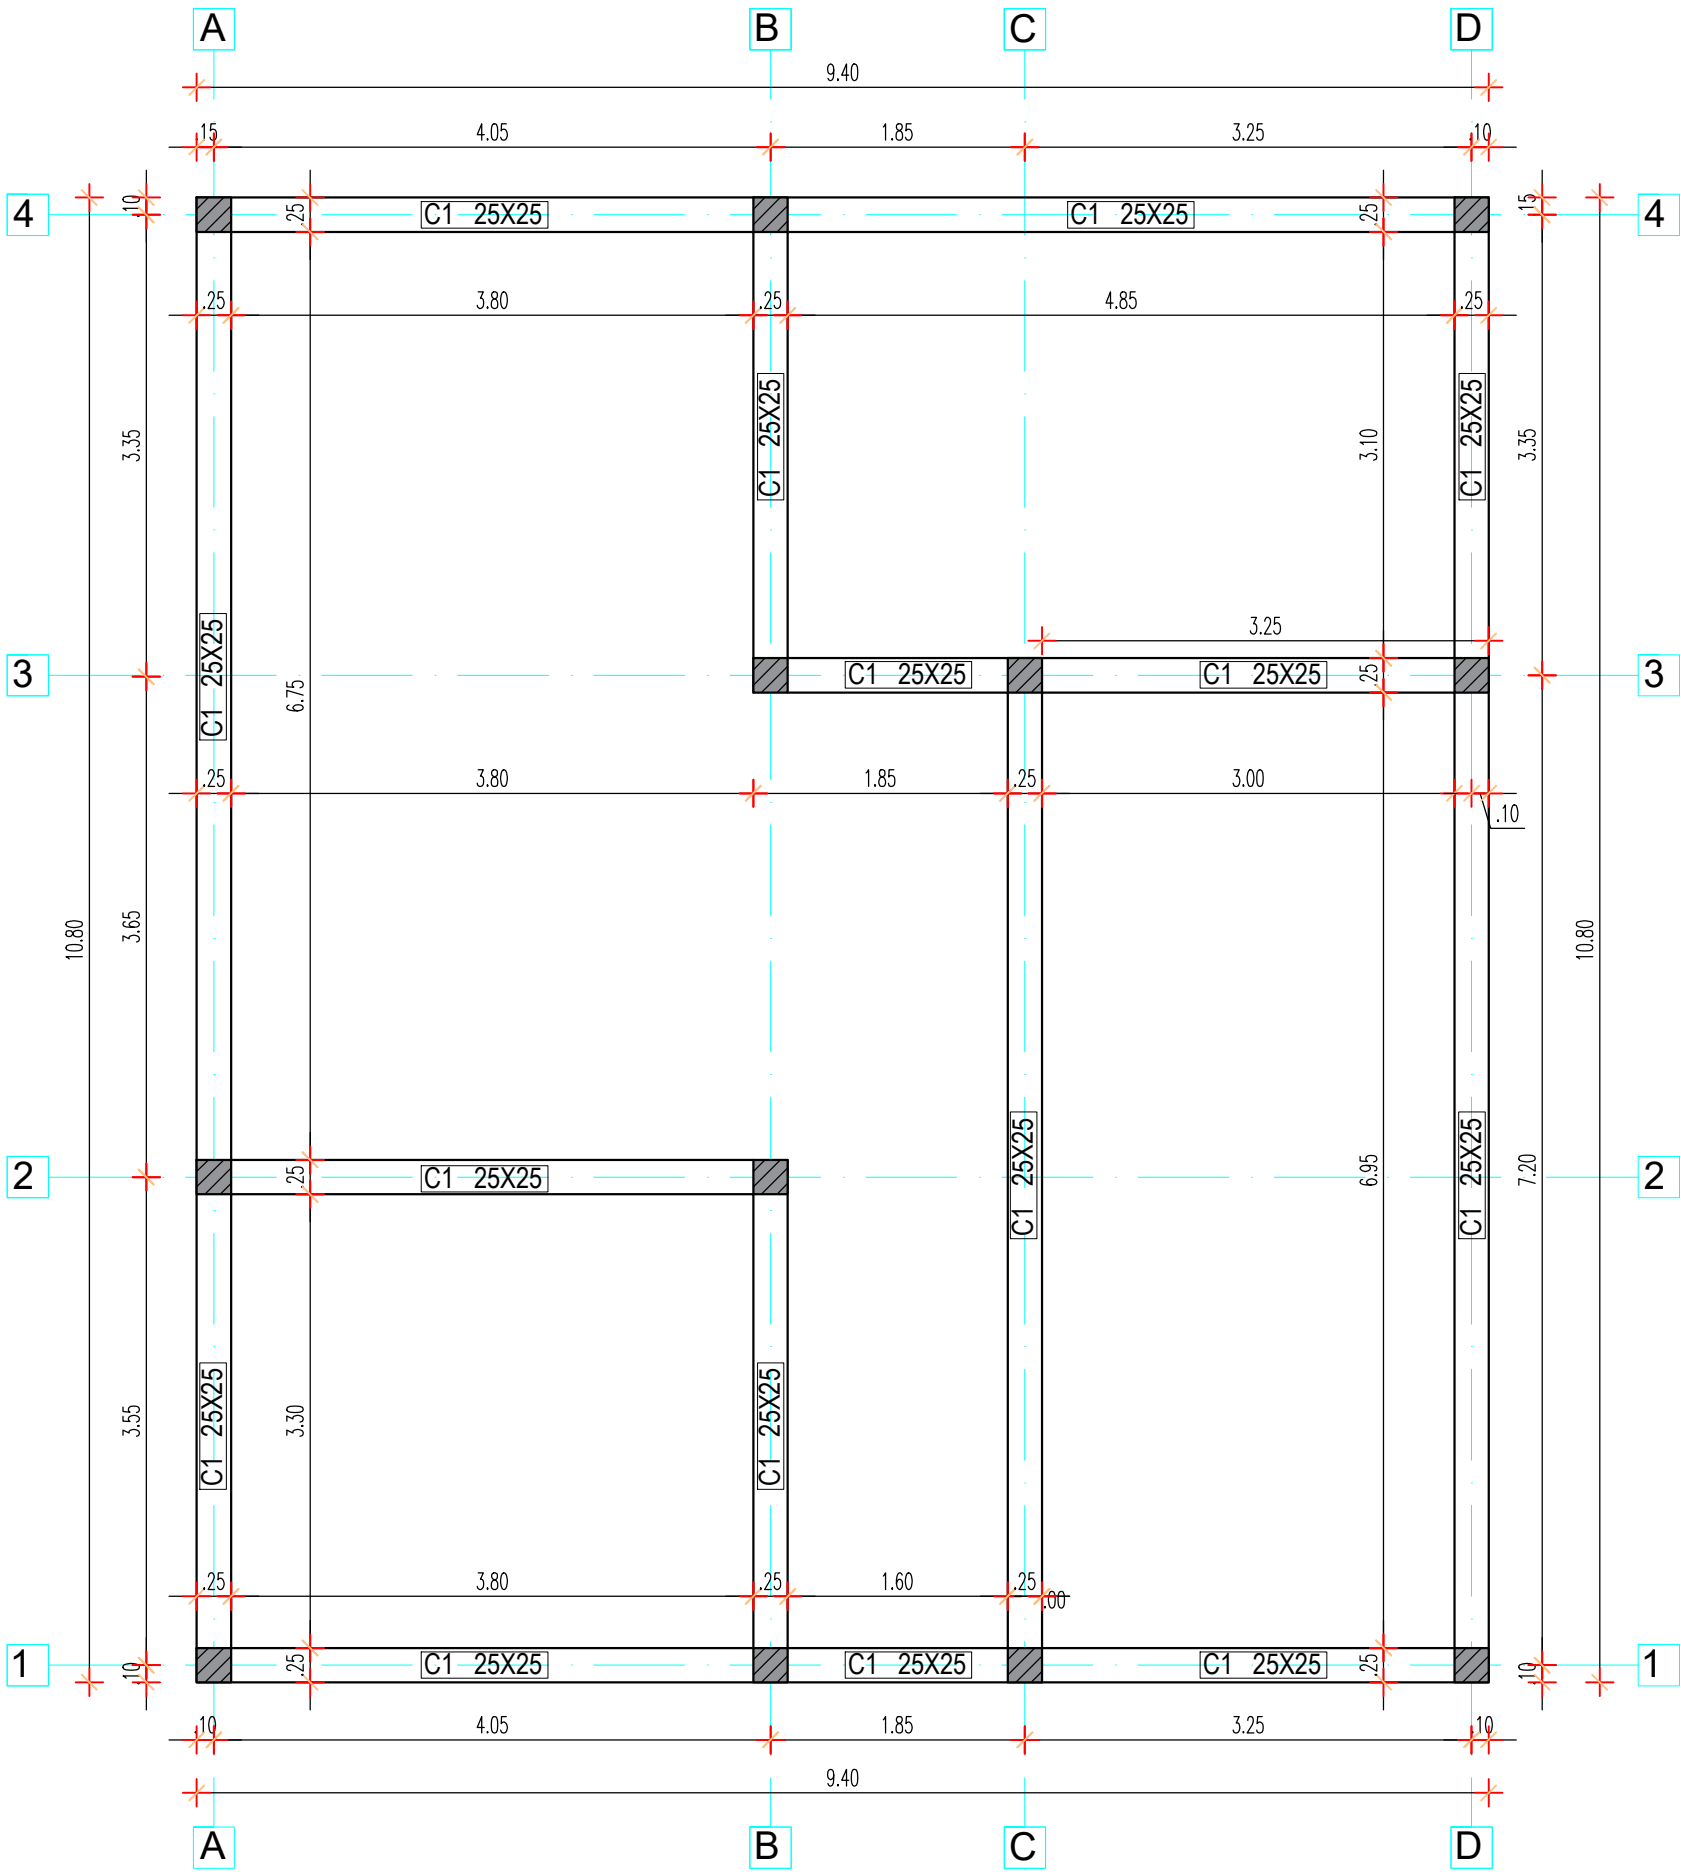

DETALIU ARMARE CENTURA 25x25
sc 1:25

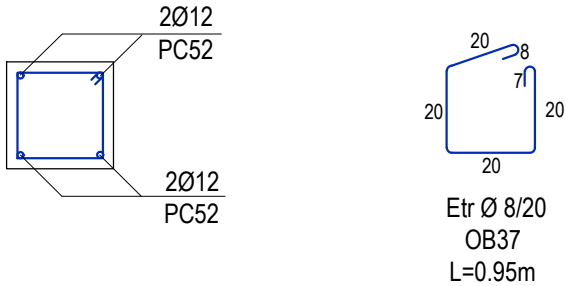

DETALIU STALPISOR S1 25x25
sc 1:25

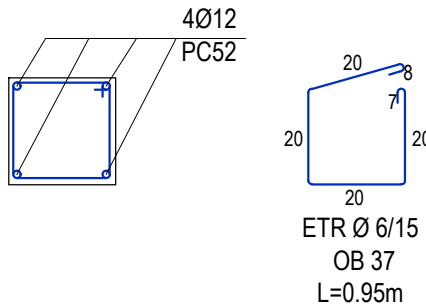

BETON C 25/30 XC1
Otel S500
Cnom=30 mm
Cv=24mm
Ciment CEMII A-S 32.5R


S teren = 825 mp
S construita = 105.60 mp
S desfasurata = 105.60 mp
S utila = 83.77 mp
Regim de inaltime P
P.O.T = 12.80 %
C.U.T = 0.128

Conform zonarii tarii, respectiv a normativelor in vigoare constructia a fost incadrata in:	
- Zona de vant	q _{ref} =0.4 daN/mp (CR1-1-4-2012)
- Zona de zapada	S _{sk} =1.5 kN/mp (CR1-1-3-2012)
- Zona de seismica de calcul	a _s =0.10 g (P100/1-2016)
- Clasa de importanta	IV (P100/1-2013)
- Categoria de importanta	D

Verificator Expert	Nume	Semantura	Cerinta	Referat /Expertiza nr./data	
				Beneficiar:	Proiect: nr:
				Obiectiv: CONSTRUIRE CASA FAMILIALA P, IMPREJMUIRE, BRANSAMENTE UTILITATI	Faza: DTAC
Sef proiect:			Scara: 1:50	PLAN CENTURI	
Proiectat:			Data:		
Desenat:					

FATADA N-E

SCARA 1:50

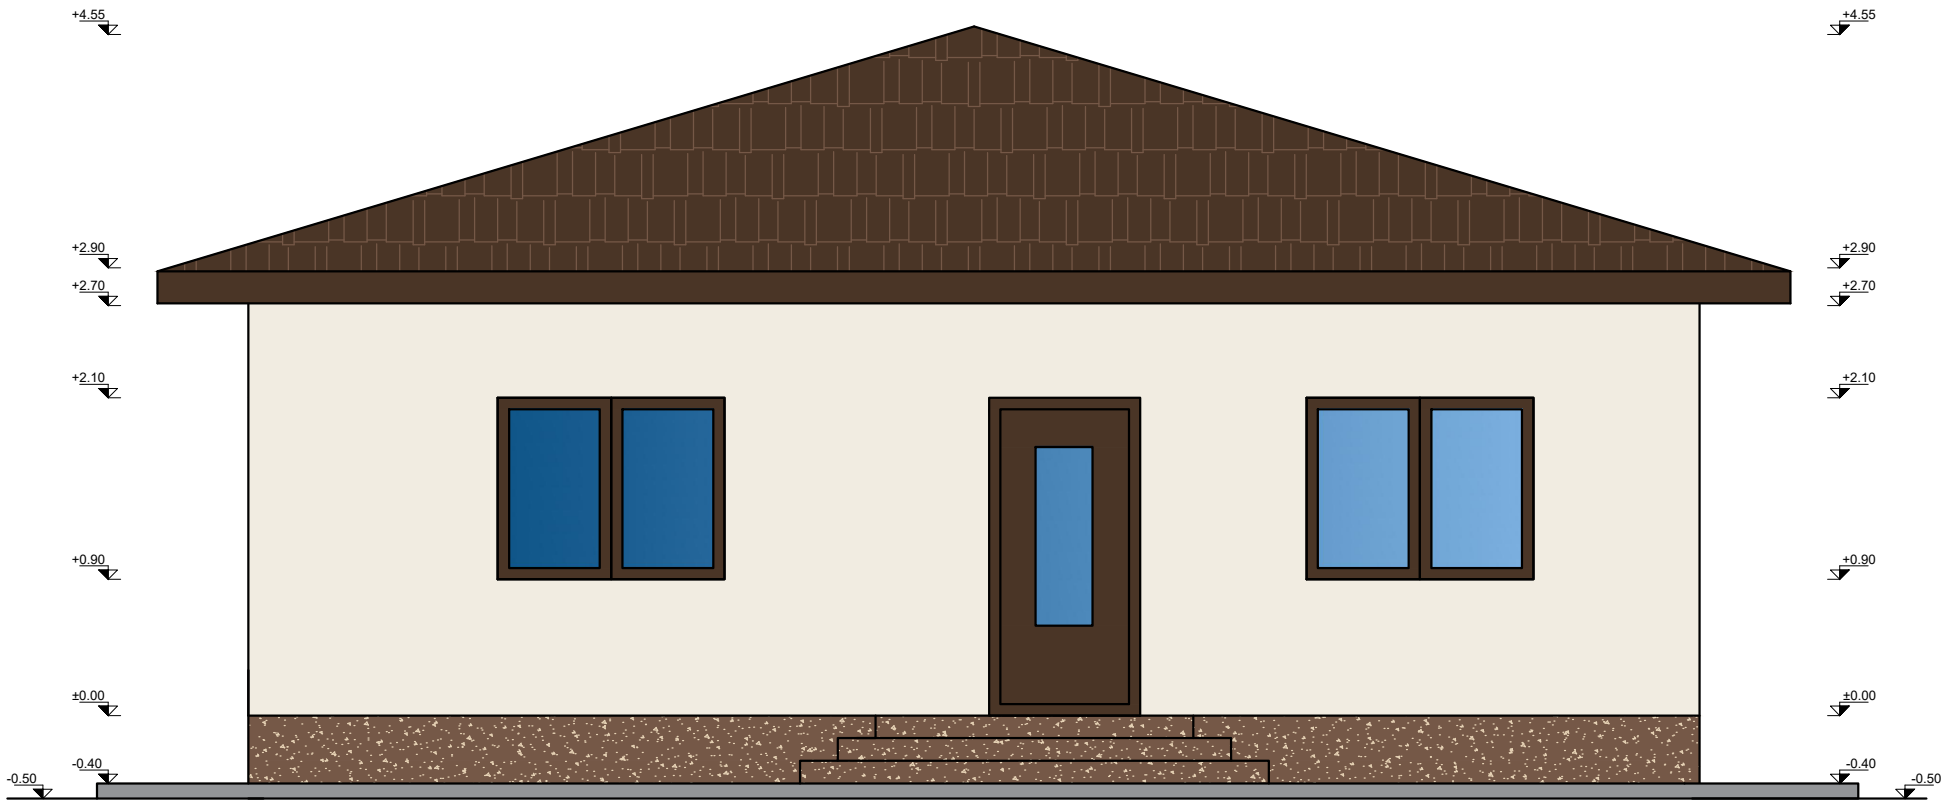


- Trotuar perimetral
- Tencuiala decorativa culoare crem
- Tencuiala decorativa
- Tamplarie PVC culoare maro, cu geam termopan
- Burlane si streasina
- Invelitoare din tabla profilata, culoare maro

Conform zonarii tarii, respectiv a normativelor in vigoare constructia a fost incadrata in:	
- Zona de vant	qref=0.4 daN/mp (CR1-1-4-2012)
- Zona de zapada	Sok=1.5 kN/mp (CR1-1-3-2012)
- Zona de seismica de calcul	ae=0.10 g (P100/1-2016)
- Clasa de importanta	IV (P100/1-2013)
- Categoria de importanta	D

S teren = 825 mp
S construita = 105.60 mp
S desfasurata = 105.60 mp
S utila = 83.77 mp
Regim de inaltime P
P.O.T = 12.80 %
C.U.T = 0.128

Verificator Expert	Nume	Semantura	Cerinta	Referat /Expertiza nr./data	
				Beneficiar:	Proiect: nr:
	Nume	Semnatura	Scara: 1:50	Obiectiv: CONSTRUIRE CASA FAMILIALA P, IMPREJMUIRE, BRANSAMENTE UTILITATI	Faza: DTAC
Sef proiect:					
Proiectat:			Data:	FATADA NORD-EST	Plansa: nr: A3
Desenat:					

FATADA SUD-VEST
SCARA 1:50

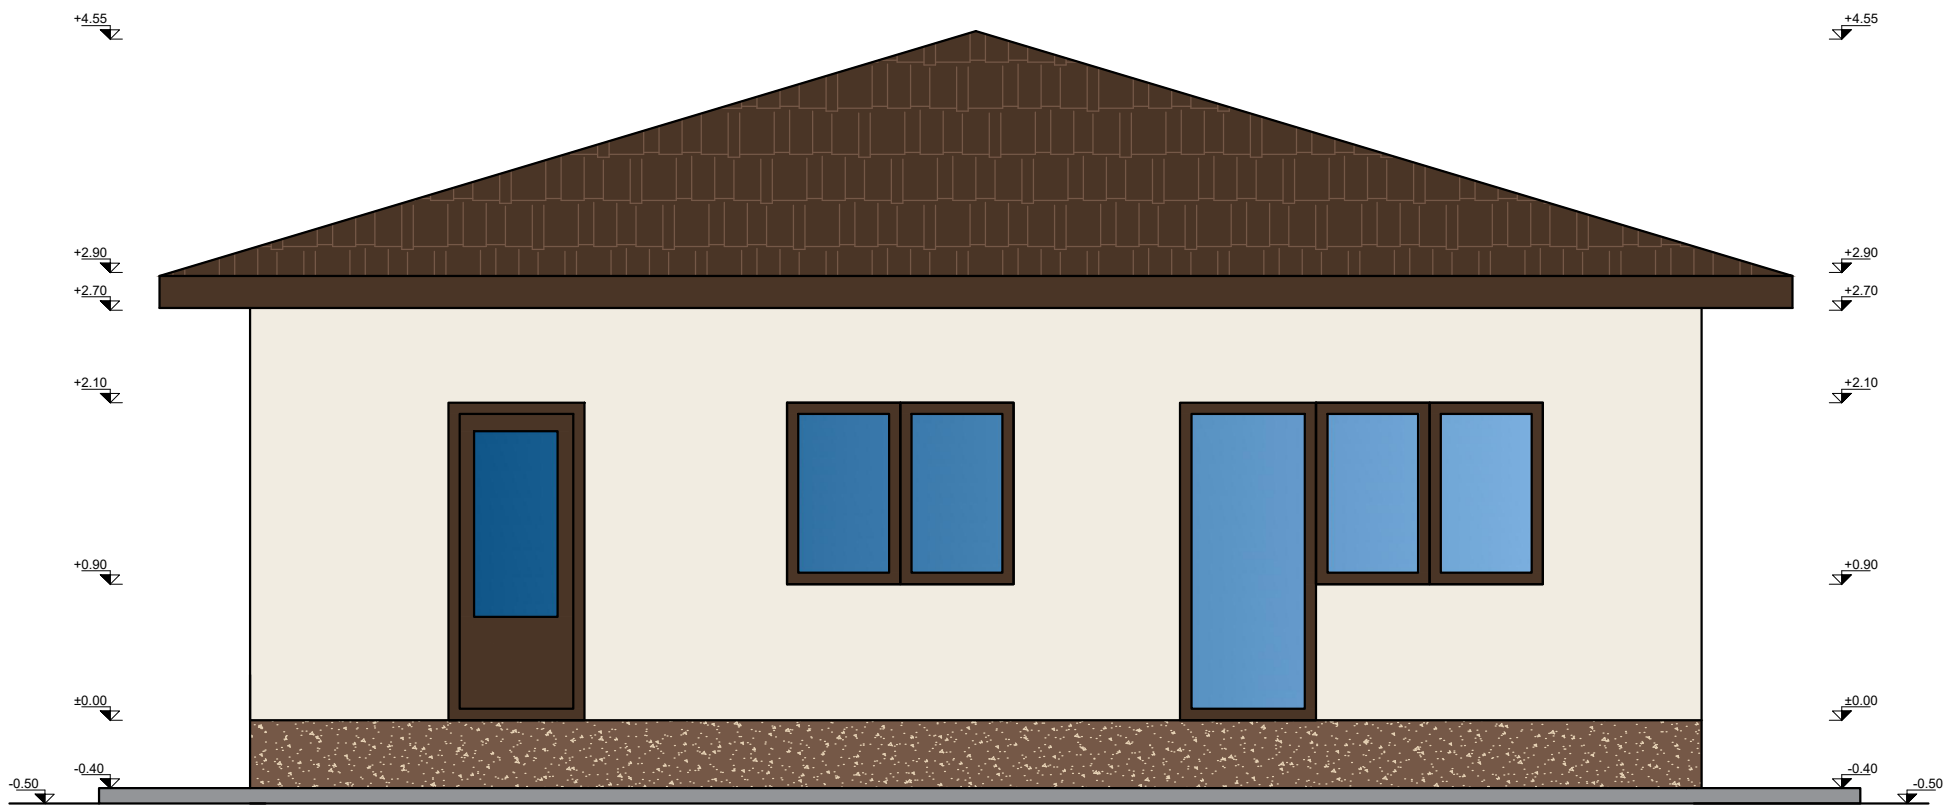

- Trotuar perimetral
- Tencuiala decorativa culoare crem
- Tencuiala decorativa
- Tamplarie PVC culoare maro, cu geam termopan
- Burlane si streasina
- Invelitoare din tabla profilata, culoare maro


Conform zonarii tarii, respectiv a normativelor in vigoare constructia a fost incadrata in:	
- Zona de vant	q _{ref} =0.4 daN/mp (CR1-1-4-2012)
- Zona de zapada	S _{0,k} =1.5 kN/mp (CR1-1-3-2012)
- Zona de seismica de calcul	a _g =0.10 g (P100/1-2016)
- Clasa de importanta	IV (P100/1-2013)
- Categoria de importanta	D

S teren = 825 mp
S construita = 105.60 mp
S desfasurata = 105.60 mp
S utila = 83.77 mp
Regim de inaltime P
P.O.T = 12.80 %
C.U.T = 0.128

Verificator Expert	Nume	Semantura	Cerinta	Referat /Expertiza nr./data	
				Beneficiar:	Proiect: nr:
	Nume	Semnatura	Scara: 1:50	Obiectiv: CONSTRUIRE CASA FAMILIALA P, IMPREJMUIRE, BRANSAMENTE UTILITATI	Faza: DTAC
Sef proiect:					
Proiectat:			Data:	FATADA SUD-VEST	Plansa: nr:
Desenat:					A4

FATADA NORD-VEST

SCARA 1:50

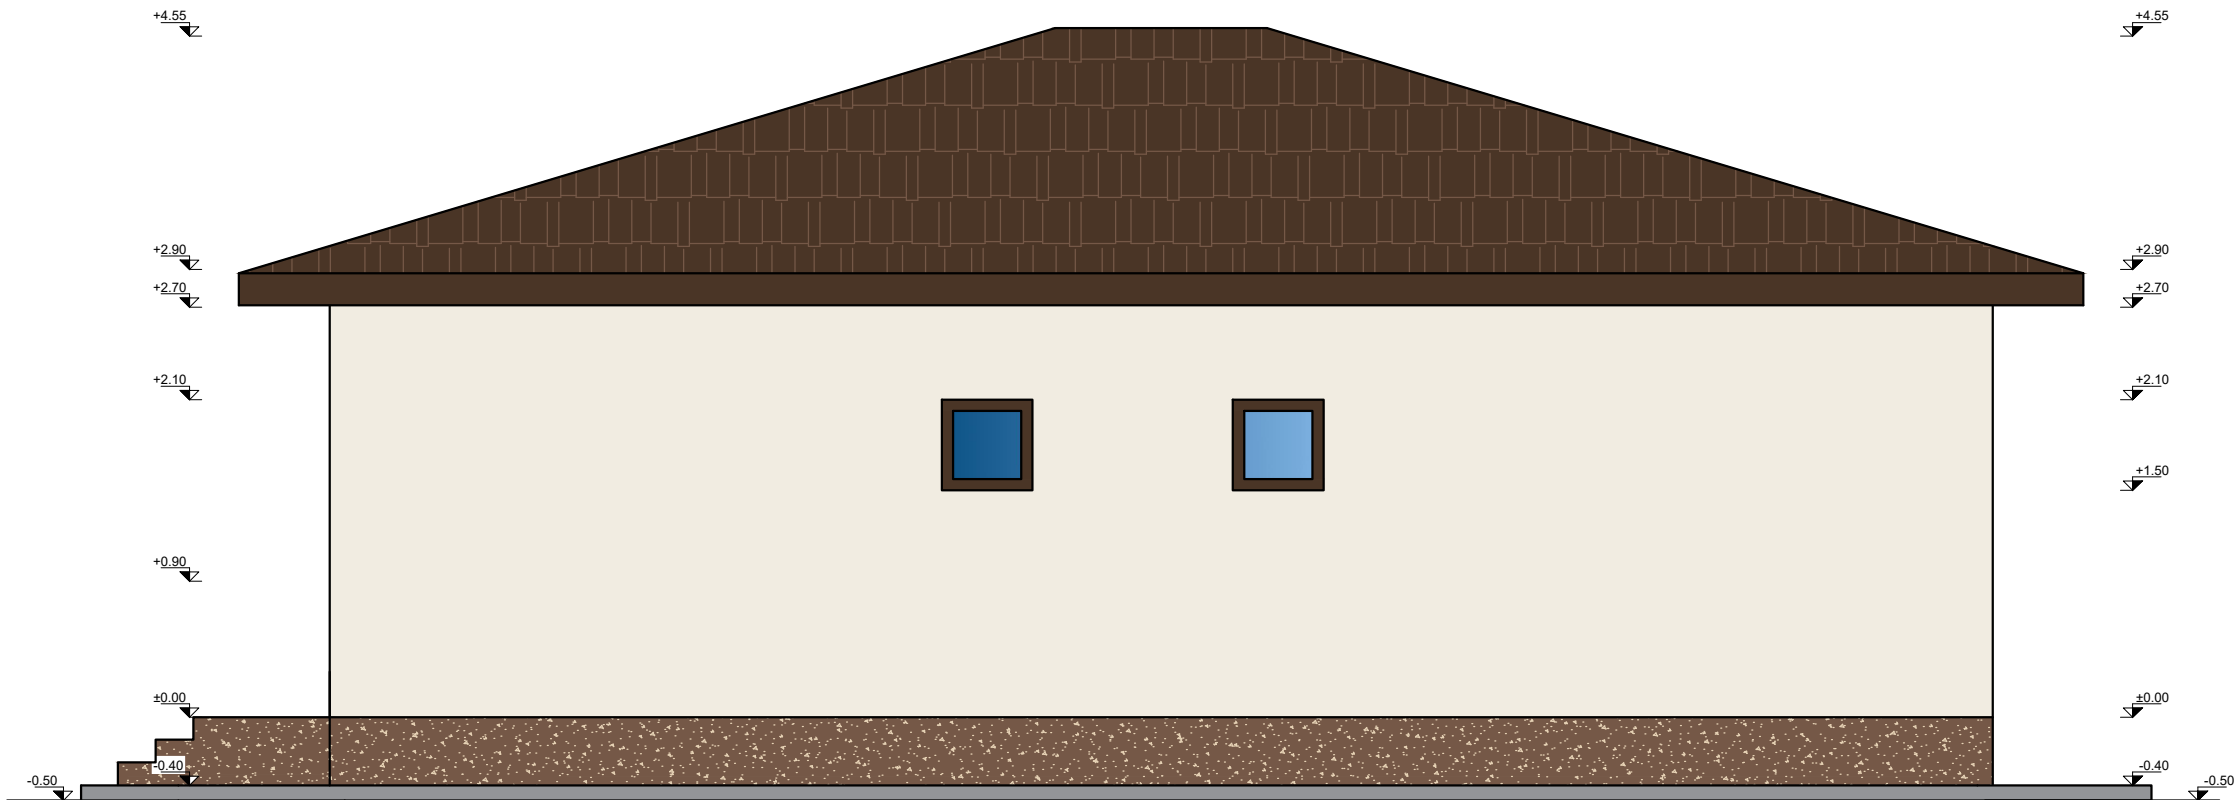

- Trotuar perimetral
- Tencuiala decorativa culoare crem
- Tencuiala decorativa
- Tamplarie PVC culoare maro, cu geam termopan
- Burlane si streasina
- Invelitoare din tabla profilata, culoare maro


Conform zonarii tarii, respectiv a normativelor in vigoare constructia a fost incadrata in:	
- Zona de vant	qref=0.4 daN/mp (CR1-1-4-2012)
- Zona de zapada	Sok=1.5 kN/mp (CR1-1-3-2012)
- Zona de seismica de calcul	ae=0.10 g (P100/1-2016)
- Clasa de importanta	IV (P100/1-2013)
- Categoria de importanta	D

S teren = 825 mp
S construita = 105.60 mp
S desfasurata = 105.60 mp
S utila = 83.77 mp
Regim de inaltime P
P.O.T = 12.80 %
C.U.T = 0.128

Verificator Expert	Nume	Semantura	Cerinta	Referat /Expertiza nr./data	
				Beneficiar:	Proiect: nr:
	Nume	Semnatura	Scara: 1:50	Obiectiv: CONSTRUIRE CASA FAMILIALA P, IMPREJMUIRE, BRANSAMENTE UTILITATI	Faza: DTAC
Sef proiect:					
Proiectat:			Data:	FATADA NORD-VEST	Plansa: nr: A5
Desenat:					

FATADA SUD-EST

SCARA 1:50

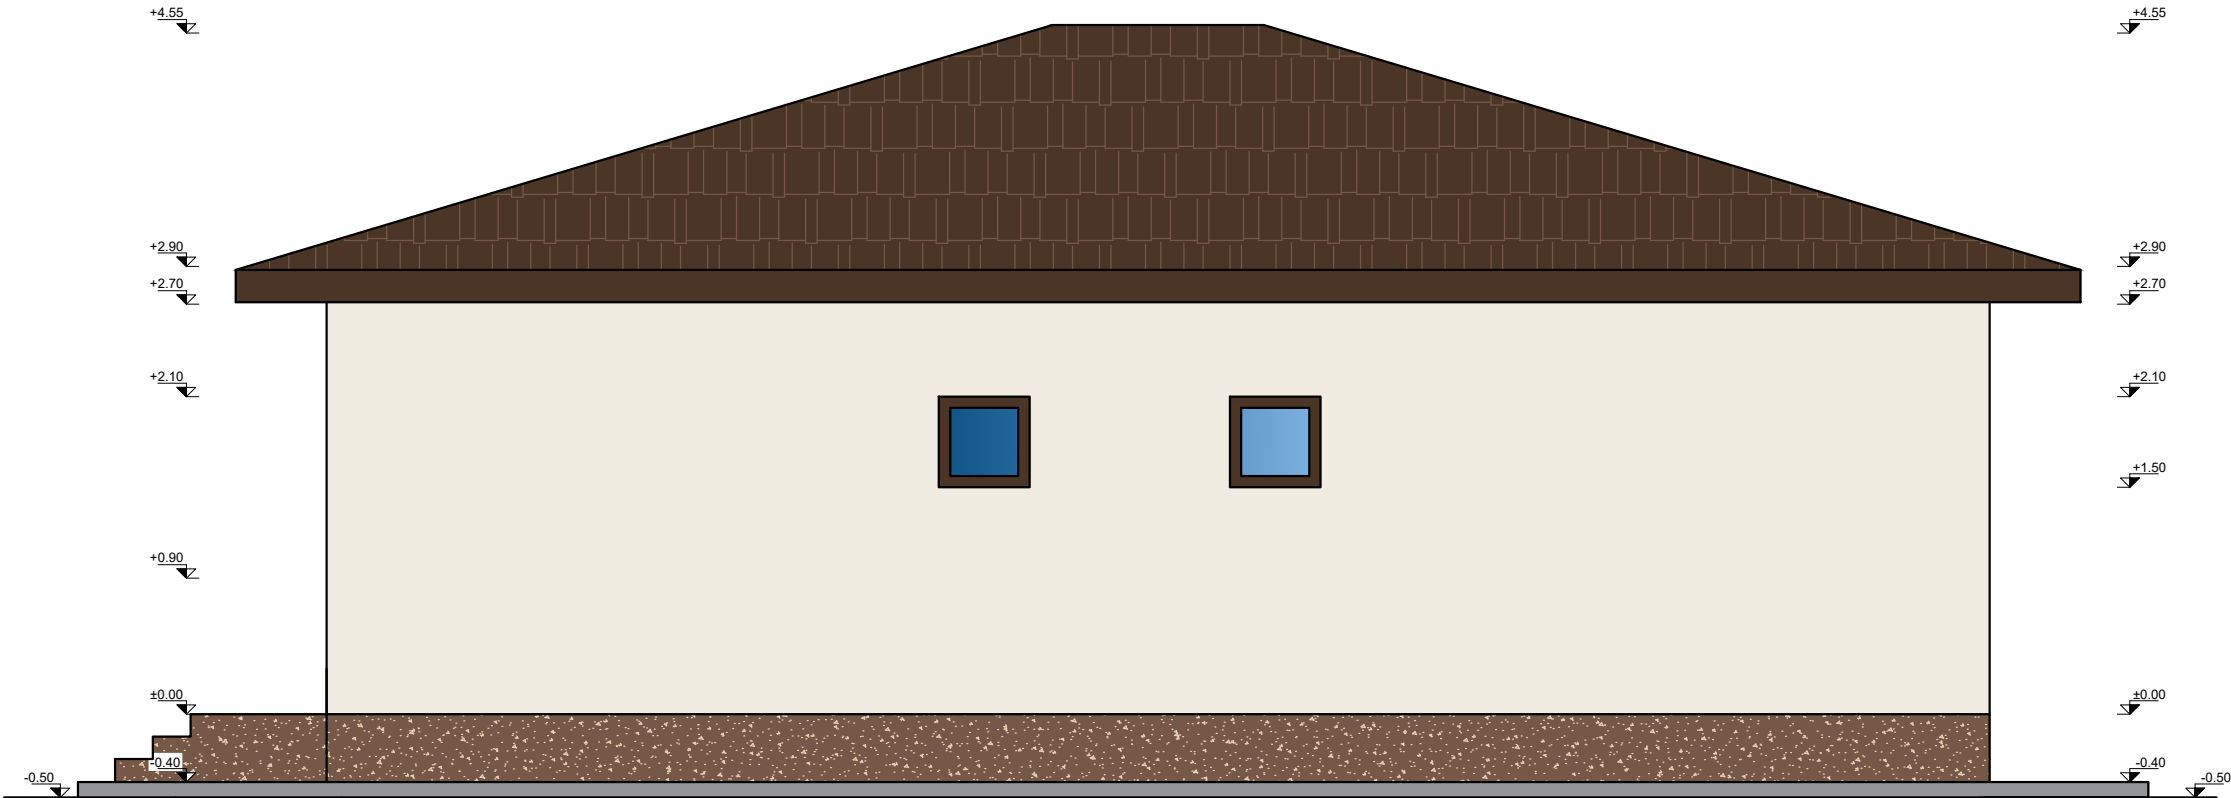




- Trotuar perimetral
- Tencuiala decorativa culoare crem
- Tencuiala decorativa
- Tamplarie PVC culoare maro, cu geam termopan
- Burlane si streasina
- Invelitoare din tabla profilata, culoare maro

Conform zonarii tarii, respectiv a normativelor in vigoare constructia a fost incadrata in:	
- Zona de vant	q _{ref} =0.4 daN/mp (CR1-1-4-2012)
- Zona de zapada	S _{ok} =1.5 kN/mp (CR1-1-3-2012)
- Zona de seismica de calcul	a _g =0.10 g (P100/1-2016)
- Clasa de importanta	IV (P100/1-2013)
- Categoria de importanta	D

S teren = 825 mp
S construita = 105.60 mp
S desfasurata = 105.60 mp
S utila = 83.77 mp
Regim de inaltime P
P.O.T = 12.80 %
C.U.T = 0.128

Verificator Expert	Nume	Semantura	Cerinta	Referat /Expertiza nr./data	
				Beneficiar:	Proiect: nr:
	Nume	Semnatura	Scara: 1:50	Obiectiv: CONSTRUIRE CASA FAMILIALA P, IMPREJMUIRE, BRANSAMENTE UTILITATI	Faza: DTAC
Sef proiect:					
Proiectat:			Data:	FATADA SUD-EST	Plansa: nr:
Desenat:					A6

PLAN FUNDATII
SCARA 1:50

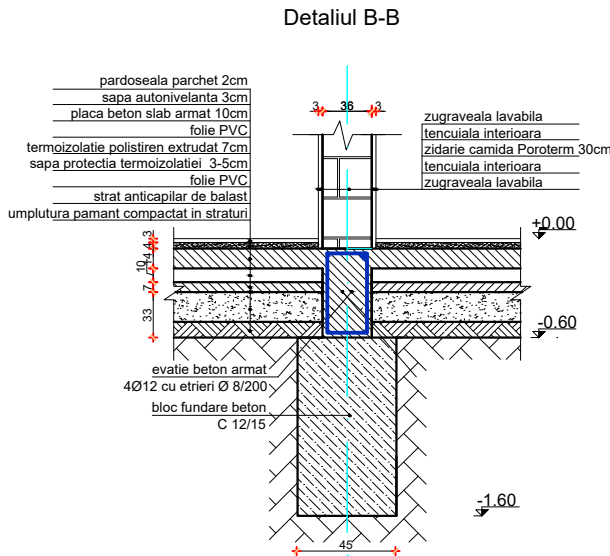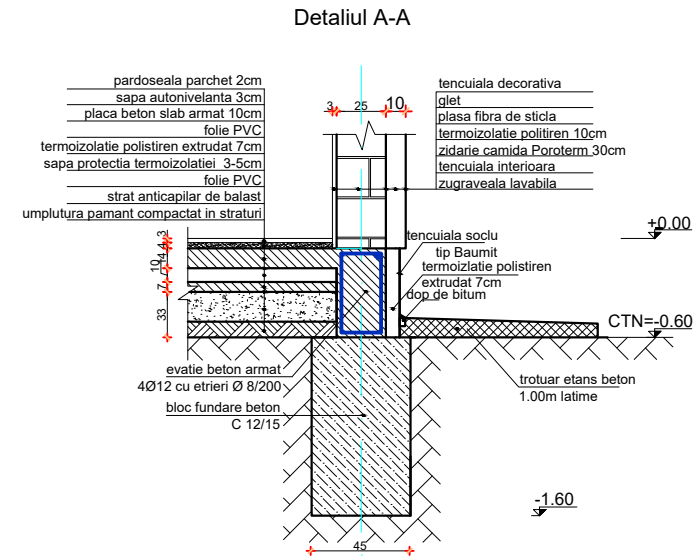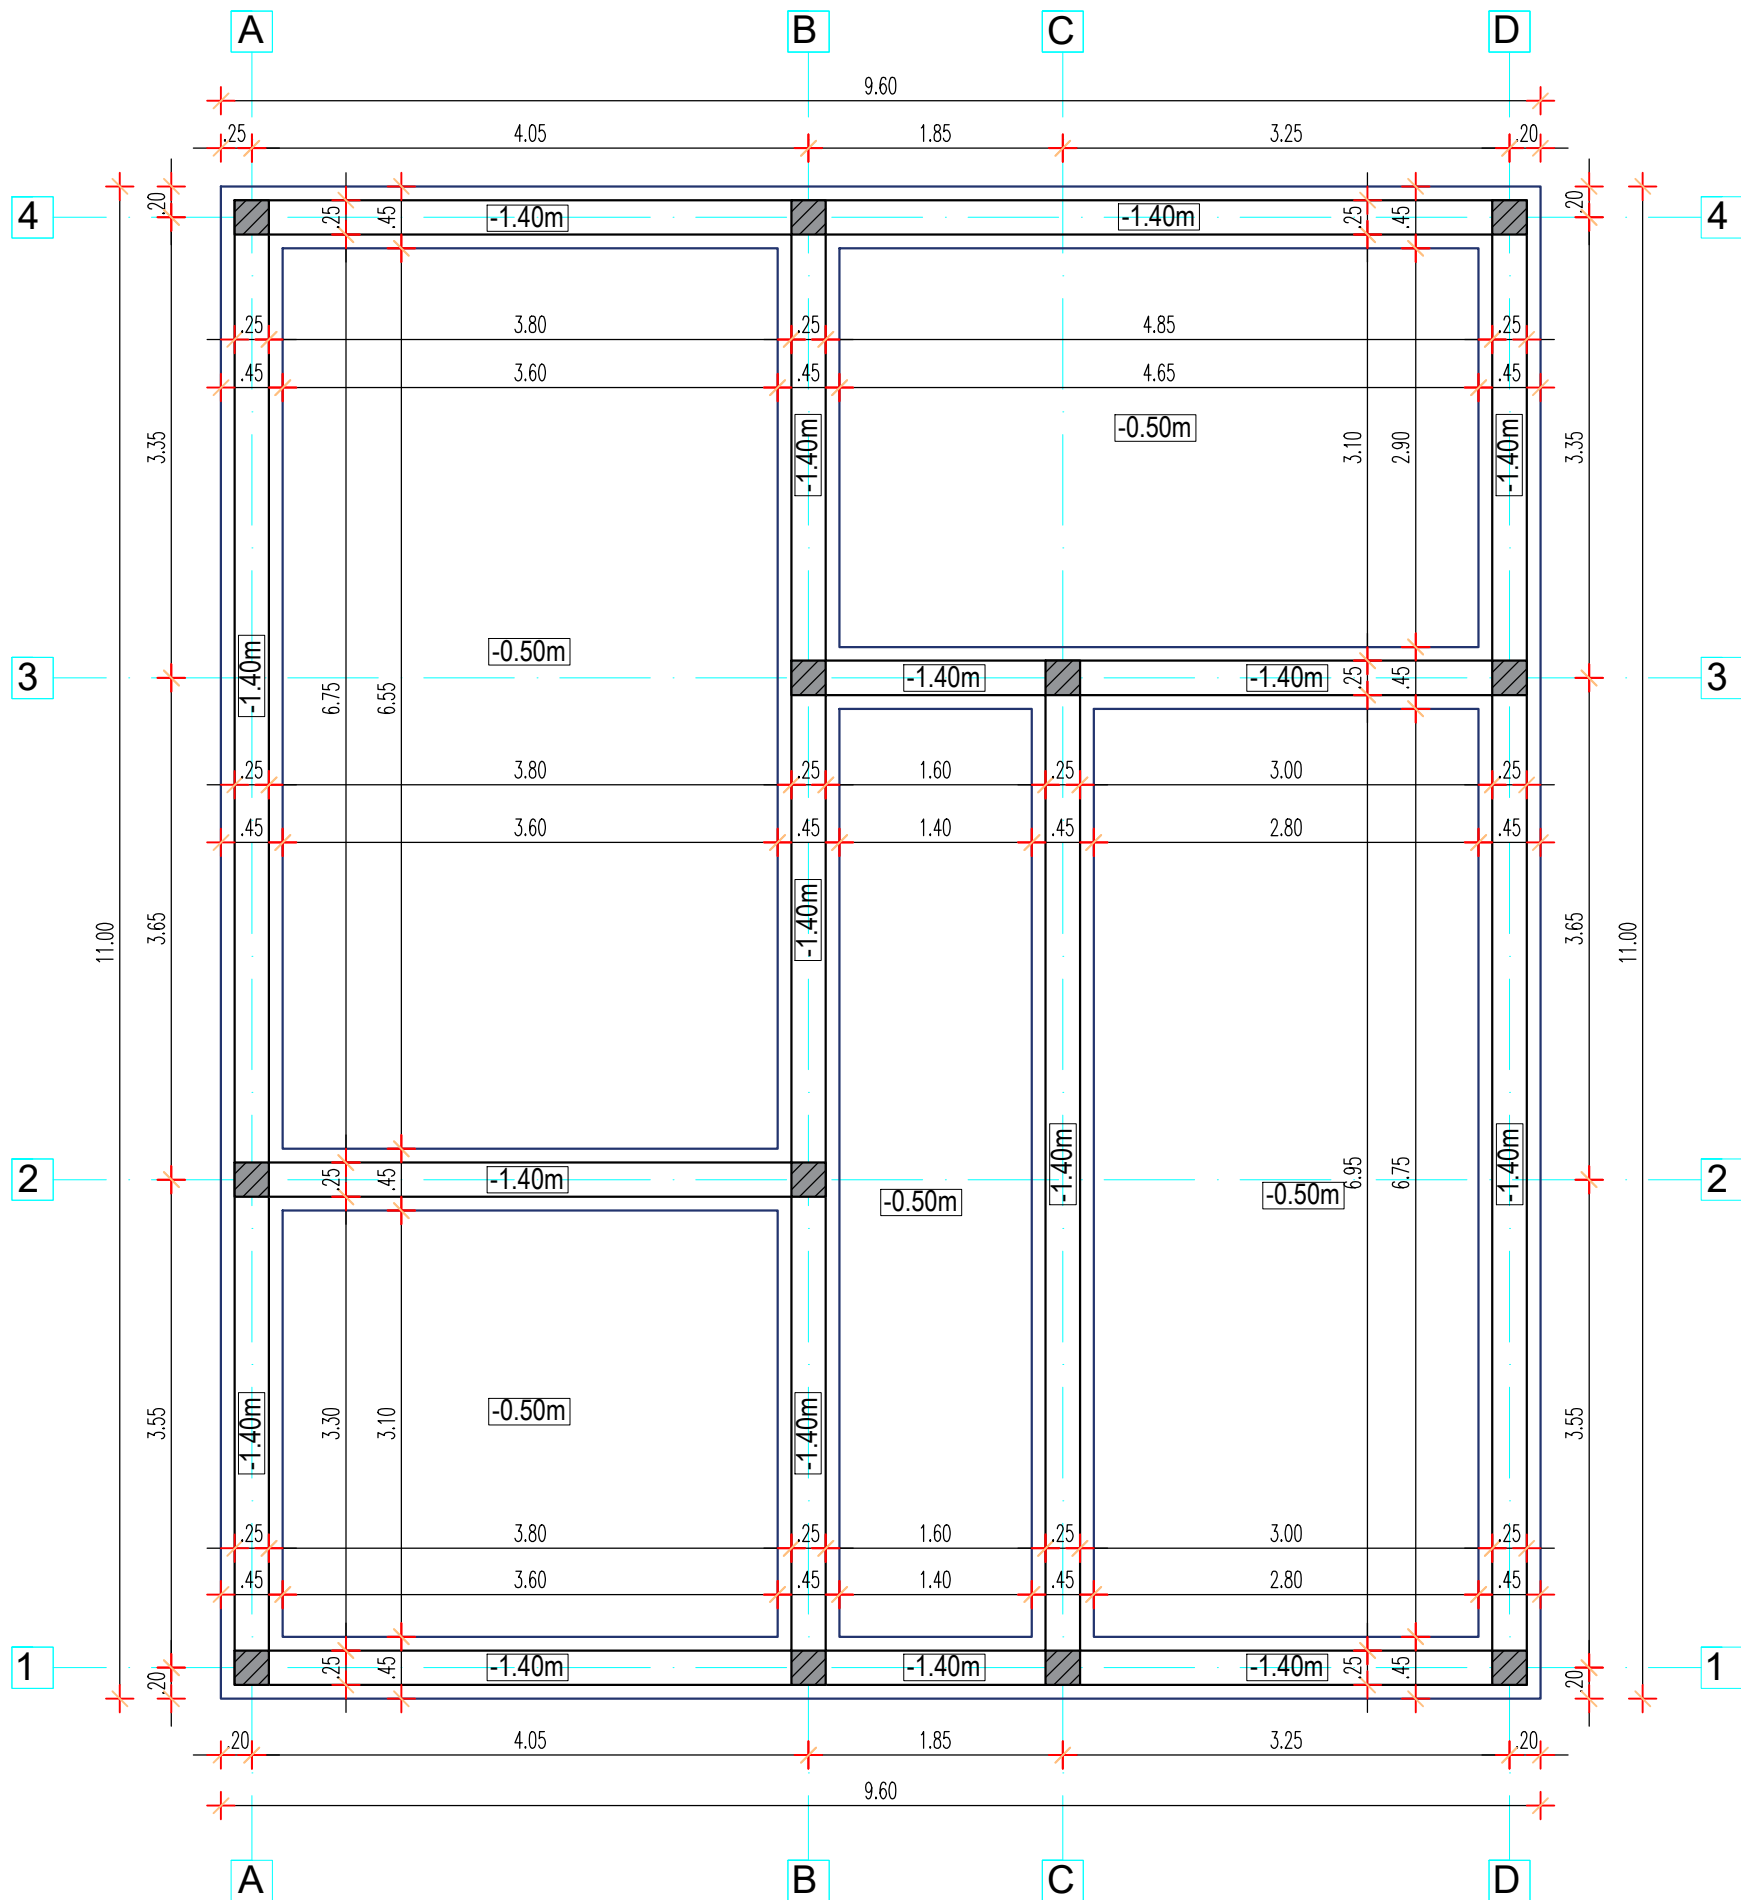

NOTA:
- FUNDATIILE NOU PROIECTATE VOR AVEA ADANCIMEA DE FUNDARE DE MIN 0.90m FATA DE COTA TERENULUI NATURAL
- SE VA ASIGURA EVACUAREA APELOR PLUVIALE
- SE VA PREVEDEA UN TROTUAR ETANS IN JURUL CONSTRUCTIEI DE MINIM 0.900m
- SE VA EVITA PLANTAREA ARBORILOR LA O DISTANTA MAI MICA DE 5 METRI FATA DE FUNDATIILE CLADIRII
- ULTIMII 20cm DE SAPATURA SE VOR SAPA NUMAI INAINTE DE TURNAREA BETONULUI
- Pconv = 265 KPa
- BETON C12/15
- ARMATURI PC52 CU ETRIERI OB37

BETON C 25/30 XC1
Otel S500
Cnom=30 mm
Cv=24mm
Ciment CEMII A-S 32.5R

S teren = 825 mp
S construita = 105.60 mp
S desfasurata = 105.60 mp
S utila = 83.77 mp
Regim de inaltime P
P.O.T = 12.80 %
C.U.T = 0.128

Verificator Expert	Nume	Semantura	Cerinta	Referat /Expertiza nr./data	
				Beneficiar:	Proiect: nr:
				Obiectiv: CONSTRUIRE CASA FAMILIALA P, IMPREJMUIRE, BRANSAMENTE UTILITATI	Faza: DTAC
Sef proiect:			Scara: 1:50	PLAN FUNDATII	Plansa: nr: R1
Proiectat:			Data:		
Desenat:					


PLAN PARTER

SCARA 1:50


DETALIU PERETE INTERIOR
DE COMPARTIMENTARE
sc 1:25



DETALIU PERETE INTERIOR
DE REZISTENTA
sc 1:25

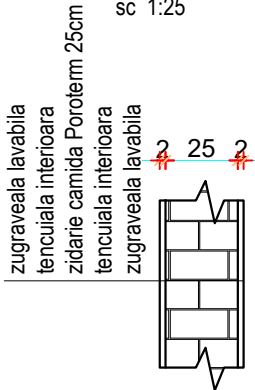

DETALIU PERETE EXTERIOR
sc 1:25

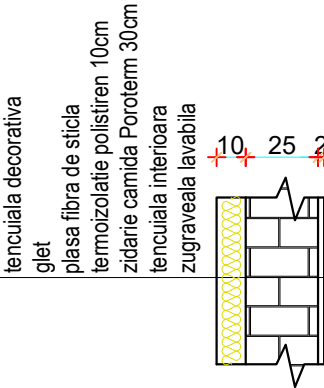


S teren = 825 mp
S construita = 105.60 mp
S desfasurata = 105.60 mp
S utila = 83.77 mp
Regim de inaltime P
P.O.T = 12.80 %
C.U.T = 0.128

Conform zonarii tarii, respectiv a normativelor in vigoare constructia a fost incadrata in:	
- Zona de vant	$q_{ref}=0.4$ daN/mp (CR1-1-4-2012)
- Zona de zapada	$S_{sk}=1.5$ kN/mp (CR1-1-3-2012)
- Zona de seismica de calcul	$a_g=0.10$ g (P100/1-2016)
- Clasa de importanta	IV (P100/1-2013)
- Categoria de importanta	D

LEGENDA :	
	ZIDARIE CARAMIDA PLINA EXISTENTA 30-50cm
	ZIDARIE CARAMIDA CU GOLURI 13-25cm
	STALPISOR BETON ARMAT 25x25cm
	OBIECTE MOBILIER

Verificator Expert	Nume	Semantura	Cerinta	Referat /Expertiza nr./data	
				Beneficiar:	Proiect: nr:
				Obiectiv: CONSTRUIRE CASA FAMILIALA P, IMPREJMUIRE, BRANSAMENTE UTILITATI	Faza: DTAC
Sef proiect:	Nume	Semnatura	Scara: 1:50	PLAN PARTER	Plansa: nr: A1
Proiectat:			Data:		
Desenat:					

PLAN INVELITOARE
SCARA 1:50

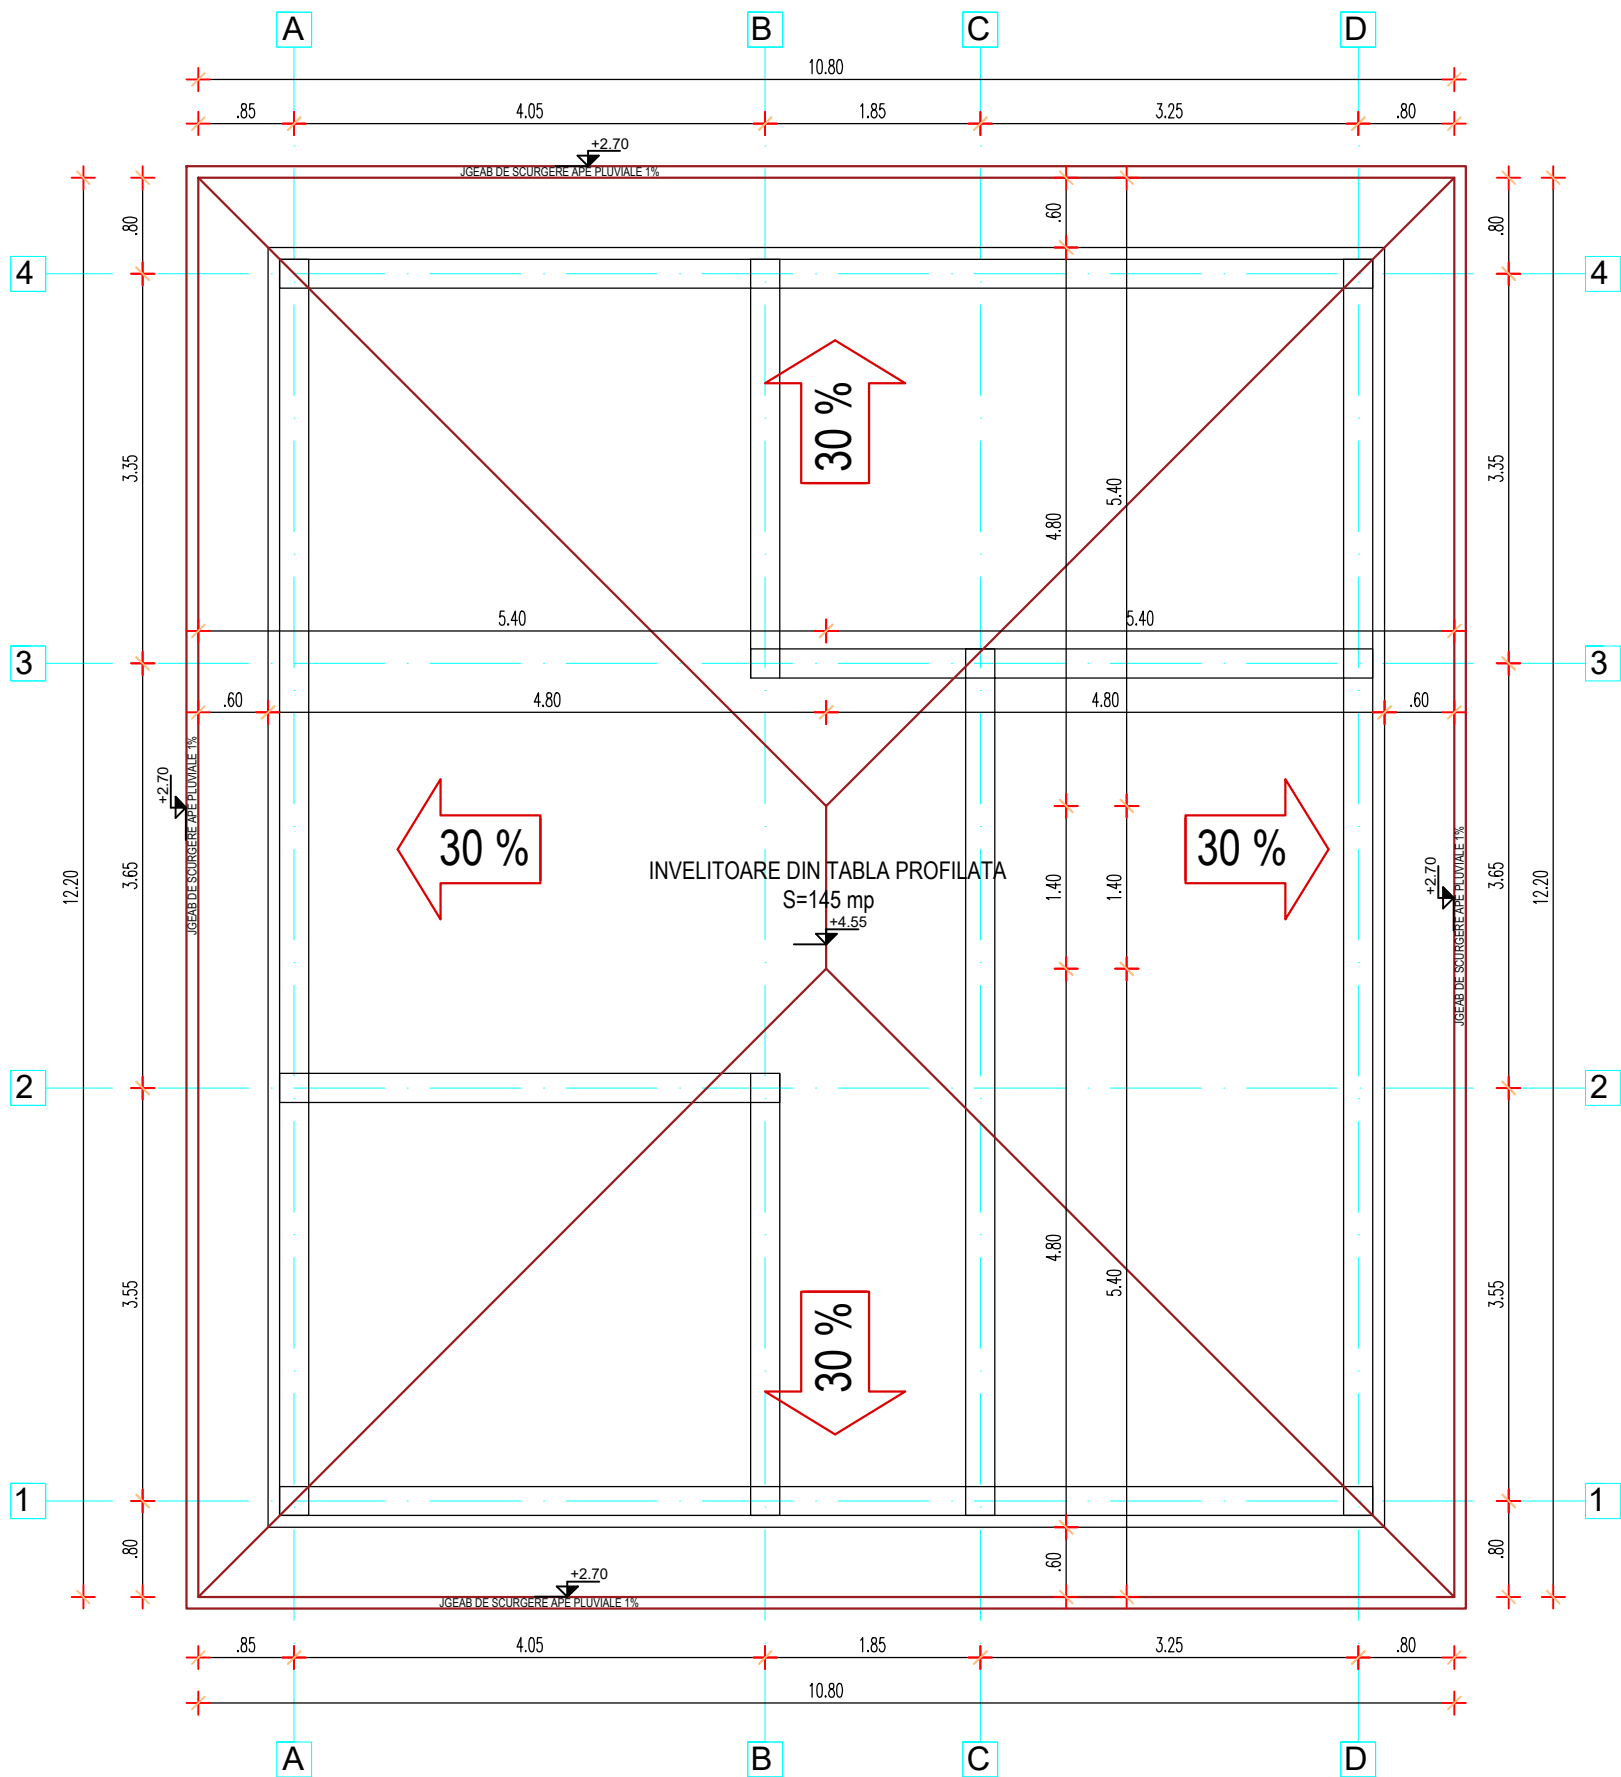


Conform zonarii tarii, respectiv a normativelor in vigoare constructia a fost incadrata in:	
- Zona de vant	q _{ref} =0.4 daN/mp (CR1-1-4-2012)
- Zona de zapada	S _{0,k} =1.5 kN/mp (CR1-1-3-2012)
- Zona de seismica de calcul	a _s =0.10 g (P100/1-2016)
- Clasa de importanta	IV (P100/1-2013)
- Categoria de importanta	D

S teren = 825 mp
S construita = 105.60 mp
S desfasurata = 105.60 mp
S utila = 83.77 mp
Regim de inaltime P
P.O.T = 12.80 %
C.U.T = 0.128

Verificator Expert	Nume	Semantura	Cerinta	Referat /Expertiza nr./data	
				Beneficiar:	Proiect: nr:
	Nume	Semnatura	Scara: 1:50	Obiectiv: CONSTRUIRE CASA FAMILIALA P, IMPREJMUIRE, BRANSAMENTE UTILITATI	Faza: DTAC
Sef proiect:					
Proiectat:			Data:	PLAN INVELITOARE	Plansa: nr: A7
Desenat:					

PLAN SARPANTA
SCARA 1:50

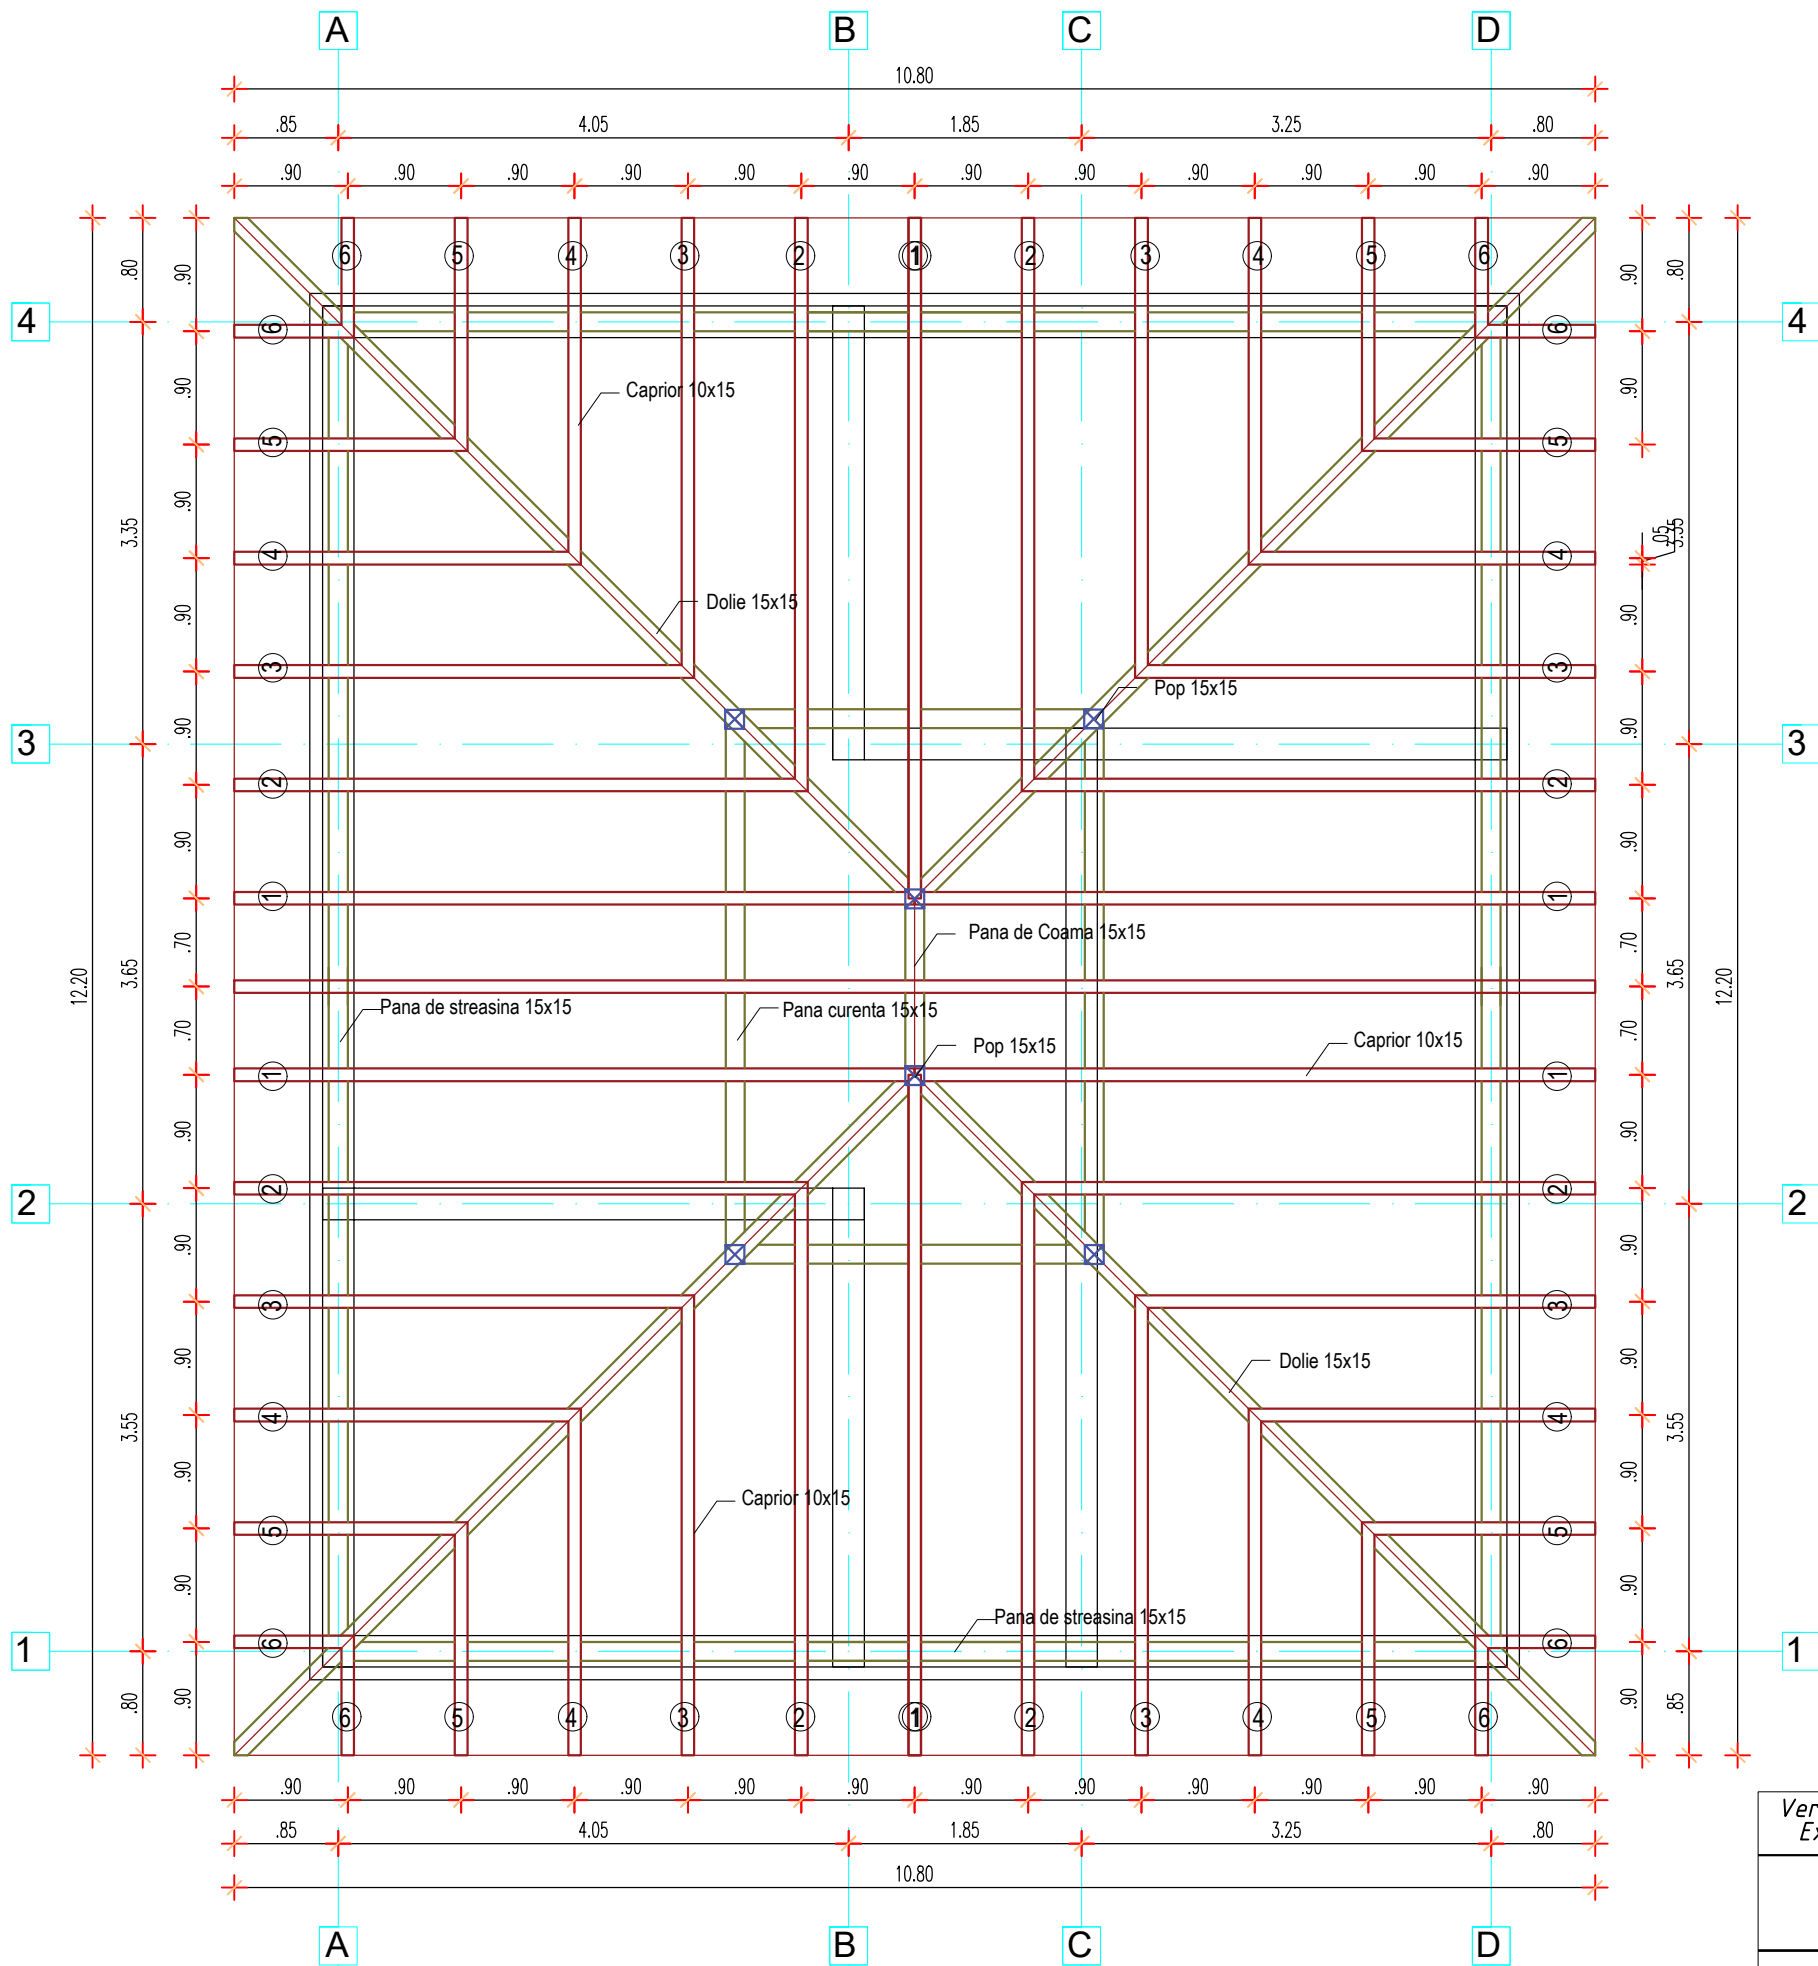


Conform zonarii tarii, respectiv a normativelor in vigoare constructia a fost incadrata in:	
- Zona de vant	$q_{ref}=0.4$ daN/mp (CR1-1-4-2012)
- Zona de zapada	$S_{sk}=1.5$ kN/mp (CR1-1-3-2012)
- Zona de seismica de calcul	$a_g=0.10$ g (P100/1-2016)
- Clasa de importanta	IV (P100/1-2013)
- Categoria de importanta	D

S teren = 825 mp
S construita = 105.60 mp
S desfasurata = 105.60 mp
S utila = 83.77 mp
Regim de inaltime P
P.O.T = 12.80 %
C.U.T = 0.128

Verificator Expert	Nume	Semantura	Cerinta	Referat /Expertiza nr./data	
				Beneficiar:	Proiect: nr:
				Obiectiv: CONSTRUIRE CASA FAMILIALA P, IMPREJMUIRE, BRANSAMENTE UTILITATI	Faza: DTAC
Sef proiect:			Scara: 1:50	PLAN SARPANTA CASA	
Proiectat:			Data:		
Desenat:					

SECTIONE
 TRANSVERSALA
 SCARA 1:50

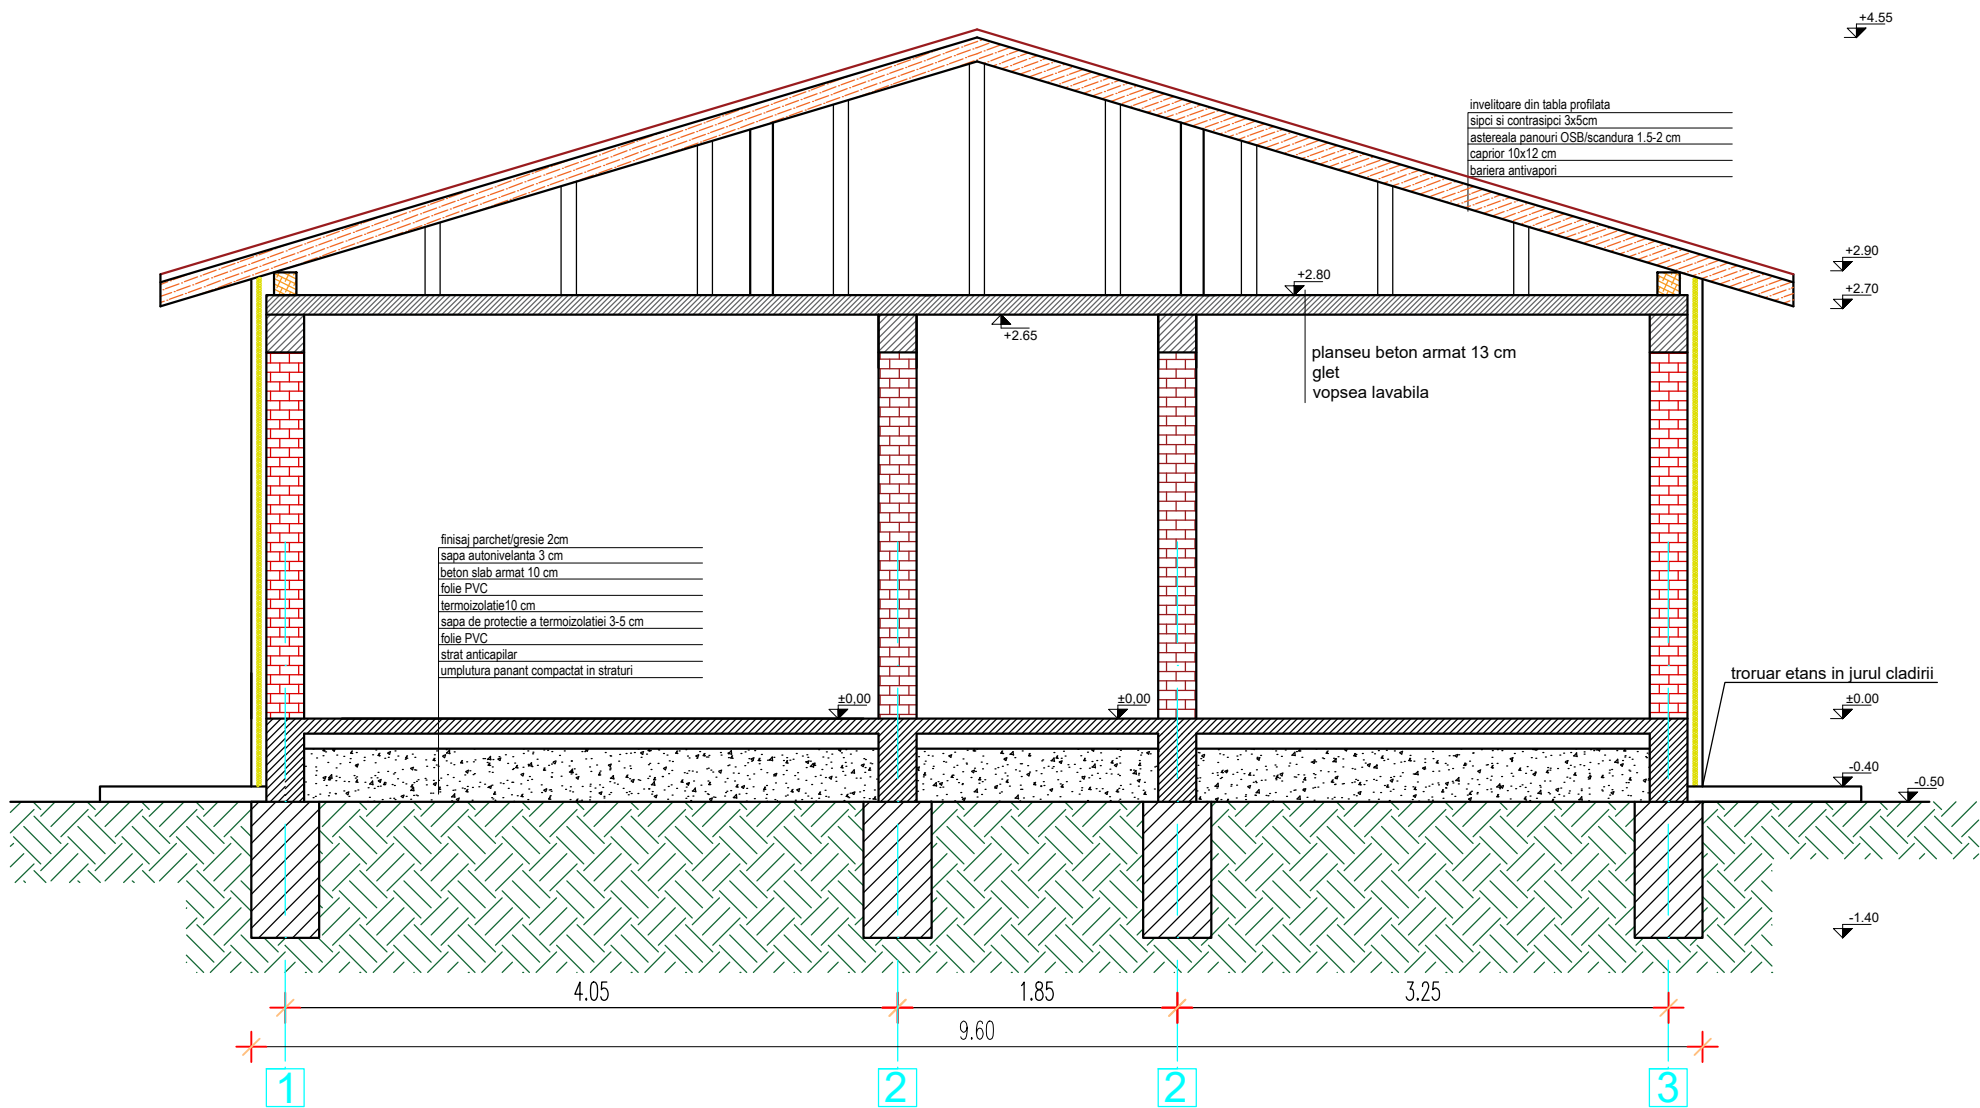

Conform zonarii tarii, respectiv a normativelor in vigoare constructia a fost incadrata in:	
- Zona de vant	$q_{ref}=0.4$ daN/mp (CR1-1-4-2012)
- Zona de zapada	$S_{sk}=1.5$ kN/mp (CR1-1-3-2012)
- Zona de seismica de calcul	$a_g=0.10$ g (P100/1-2016)
- Clasa de importanta	IV (P100/1-2013)
- Categoria de importanta	D

S teren = 825 mp
 S construita = 105.60 mp
 S desfasurata = 105.60 mp
 S utila = 83.77 mp
 Regim de inaltime P
 P.O.T = 12.80 %
 C.U.T = 0.128

Verificator Expert	Nume	Semantura	Cerinta	Referat /Expertiza nr./data	
				Beneficiar:	Proiect: nr:
	Nume	Semnatura	Scara: 1:50	Obiectiv: CONSTRUIRE CASA FAMILIALA P, IMPREJMUIRE, BRANSAMENTE UTILITATI	Faza: DTAC
Sef proiect:					
Proiectat:			Data:	SECTIONE TRANSVERSALA	Plansa: nr: A2
Desenat:					